



CORWILARCHITECTS
4210 LA GUÑA ST. CORAL GABLES FL 33146
LIC. NO. AA-C002151 T.305.448.7383

PROJECT:



Casa Familia
Exceptional Housing for Exceptional People

OWNER:



10951 SW 84th ST,
MIAMI-DADE, FLORIDA 33173

PHASE:

PERMIT SET

**ENLARGED KITCHENETTE (NO
COOKING), BREAK ROOM, &
COPY/FILE ROOM**


REVISIONS		
Rev #	Revision Description	Date
1	Bldg Review Cmt	09/30/20
2	County Comments	11/20/20
3	County Comments	01/08/21
5	County Comments/ Owner VE	04/03/23
7	Pre-con RFIs/Coord.	05/03/24
9	Coordin.	07/19/24
10	Coordin./Bulletin #6	09/20/24

SEAL:


THIS DRAWING IS THE PROPERTY OF CORWIL ARCHITECTS INC.
UNLESS OTHERWISE PROVIDED FOR BY CONTRACT, THE
CONTENTS OF THIS DRAWING ARE CONFIDENTIAL AND
SHALL NOT BE TRANSMITTED TO ANY OTHER PARTY
EXCEPT AS AGREED TO BY THE ARCHITECT/ENGINEERS.

DATE: 5-18-2020
JOB No.: 2019-20
DRAWN BY: MA, CM, JM, JW, FG
APPR BY: AMC
PRINTED: 11/25/2024


A-5.08

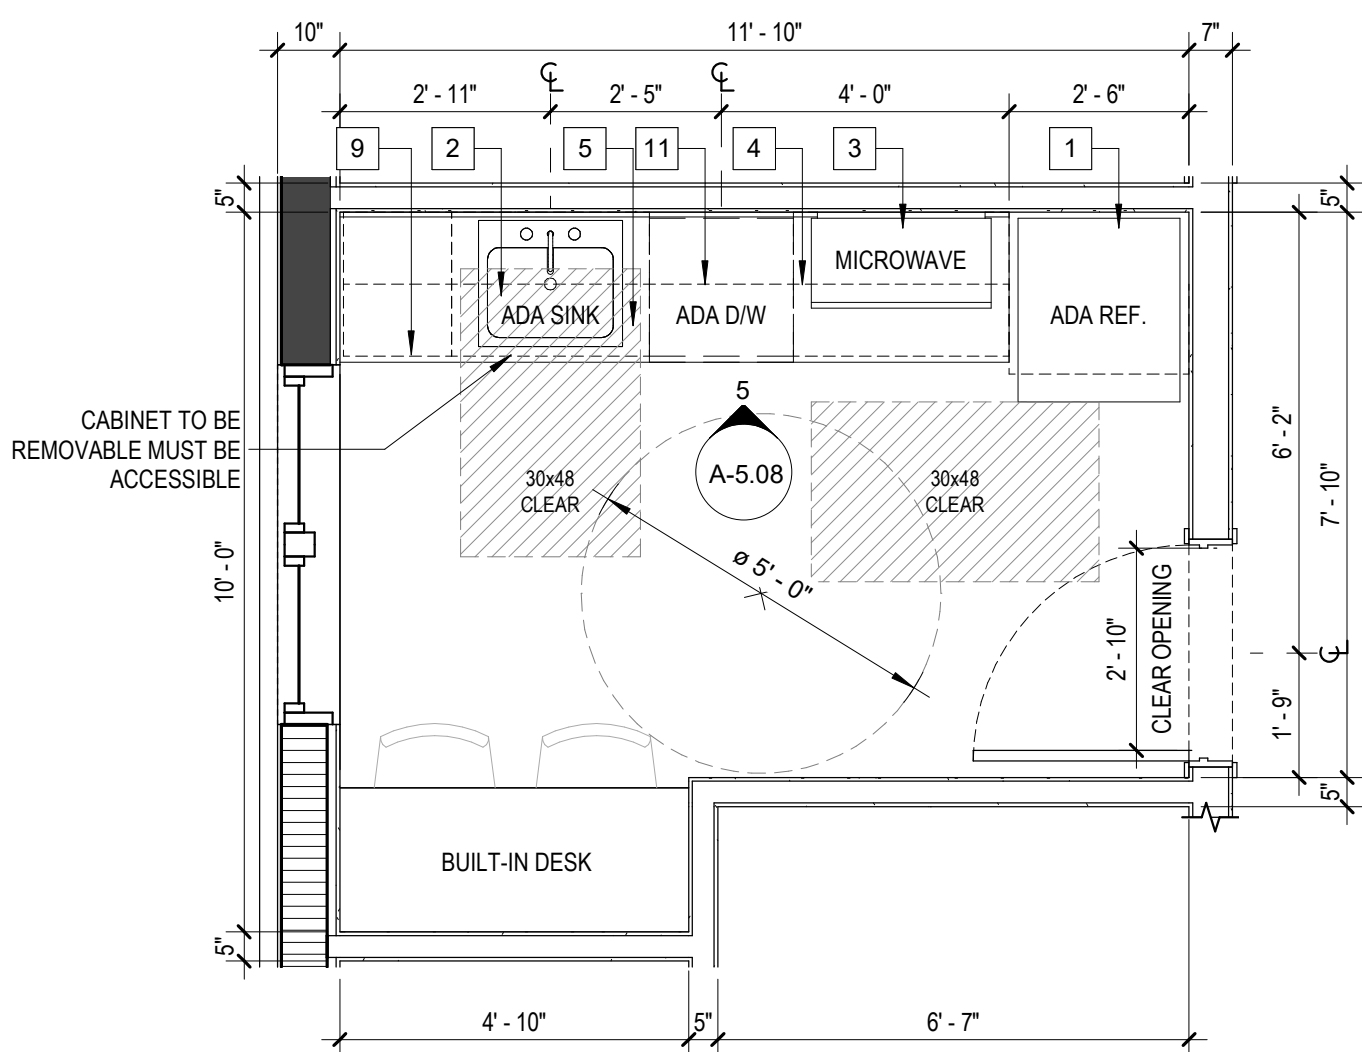


3 COMMUNITY CENTER BREAK ROOM
SCALE: 3/8" = 1'-0"

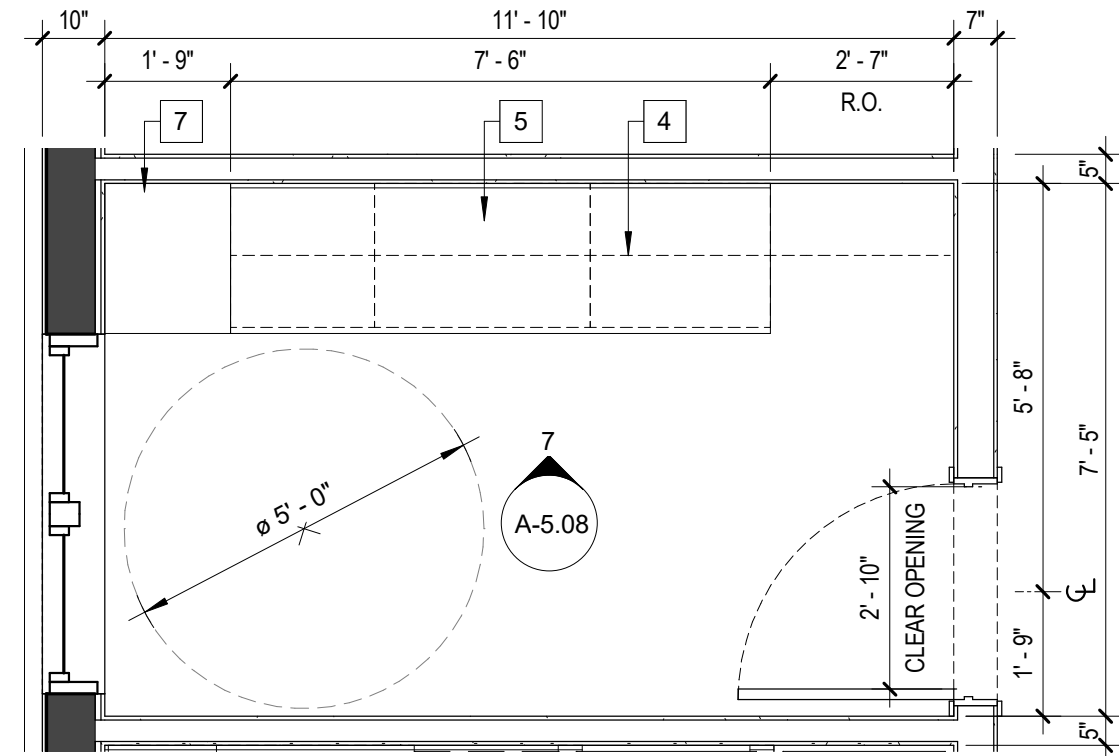


4 COMMUNITY CENTER COPY/FILE ROOM
SCALE: 3/8" = 1'-0"

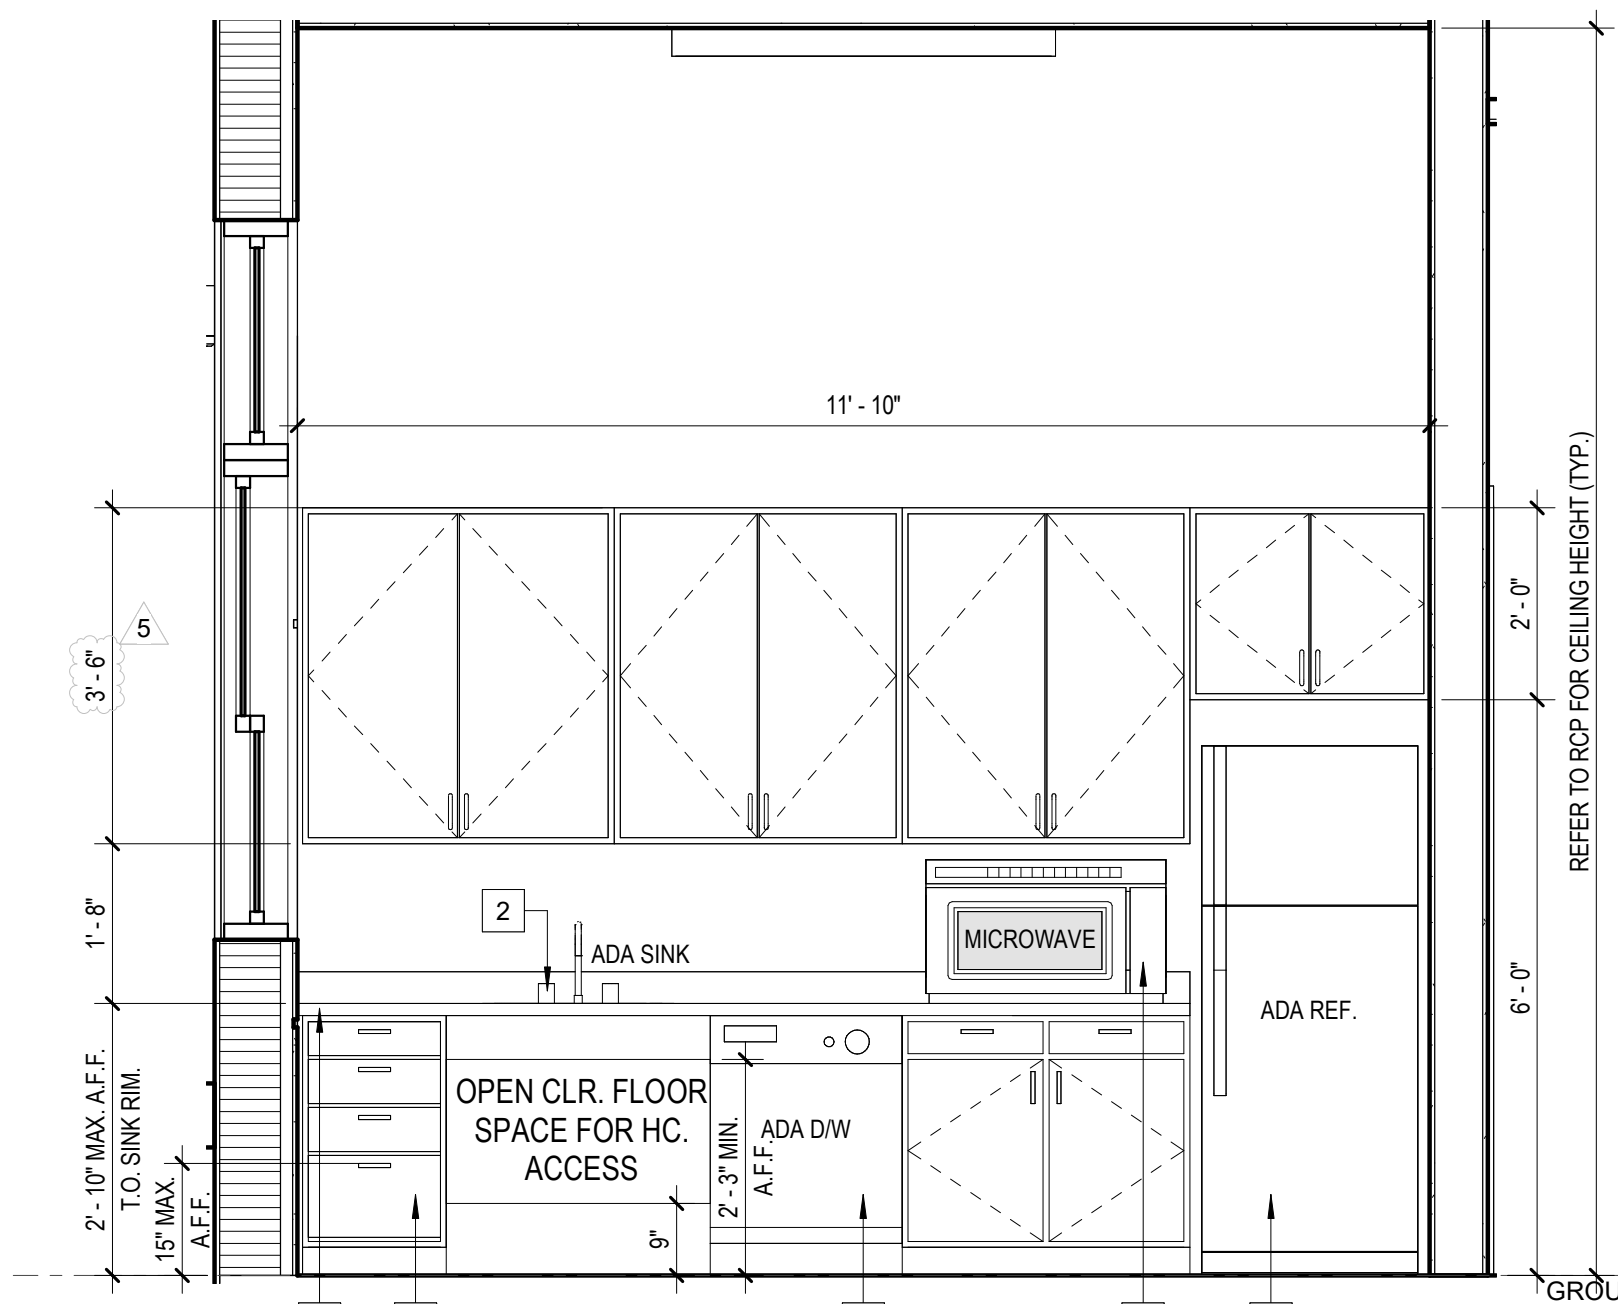

5 BREAK ROOM NORTH ELEVATION
SCALE: 1/2" = 1'-0"

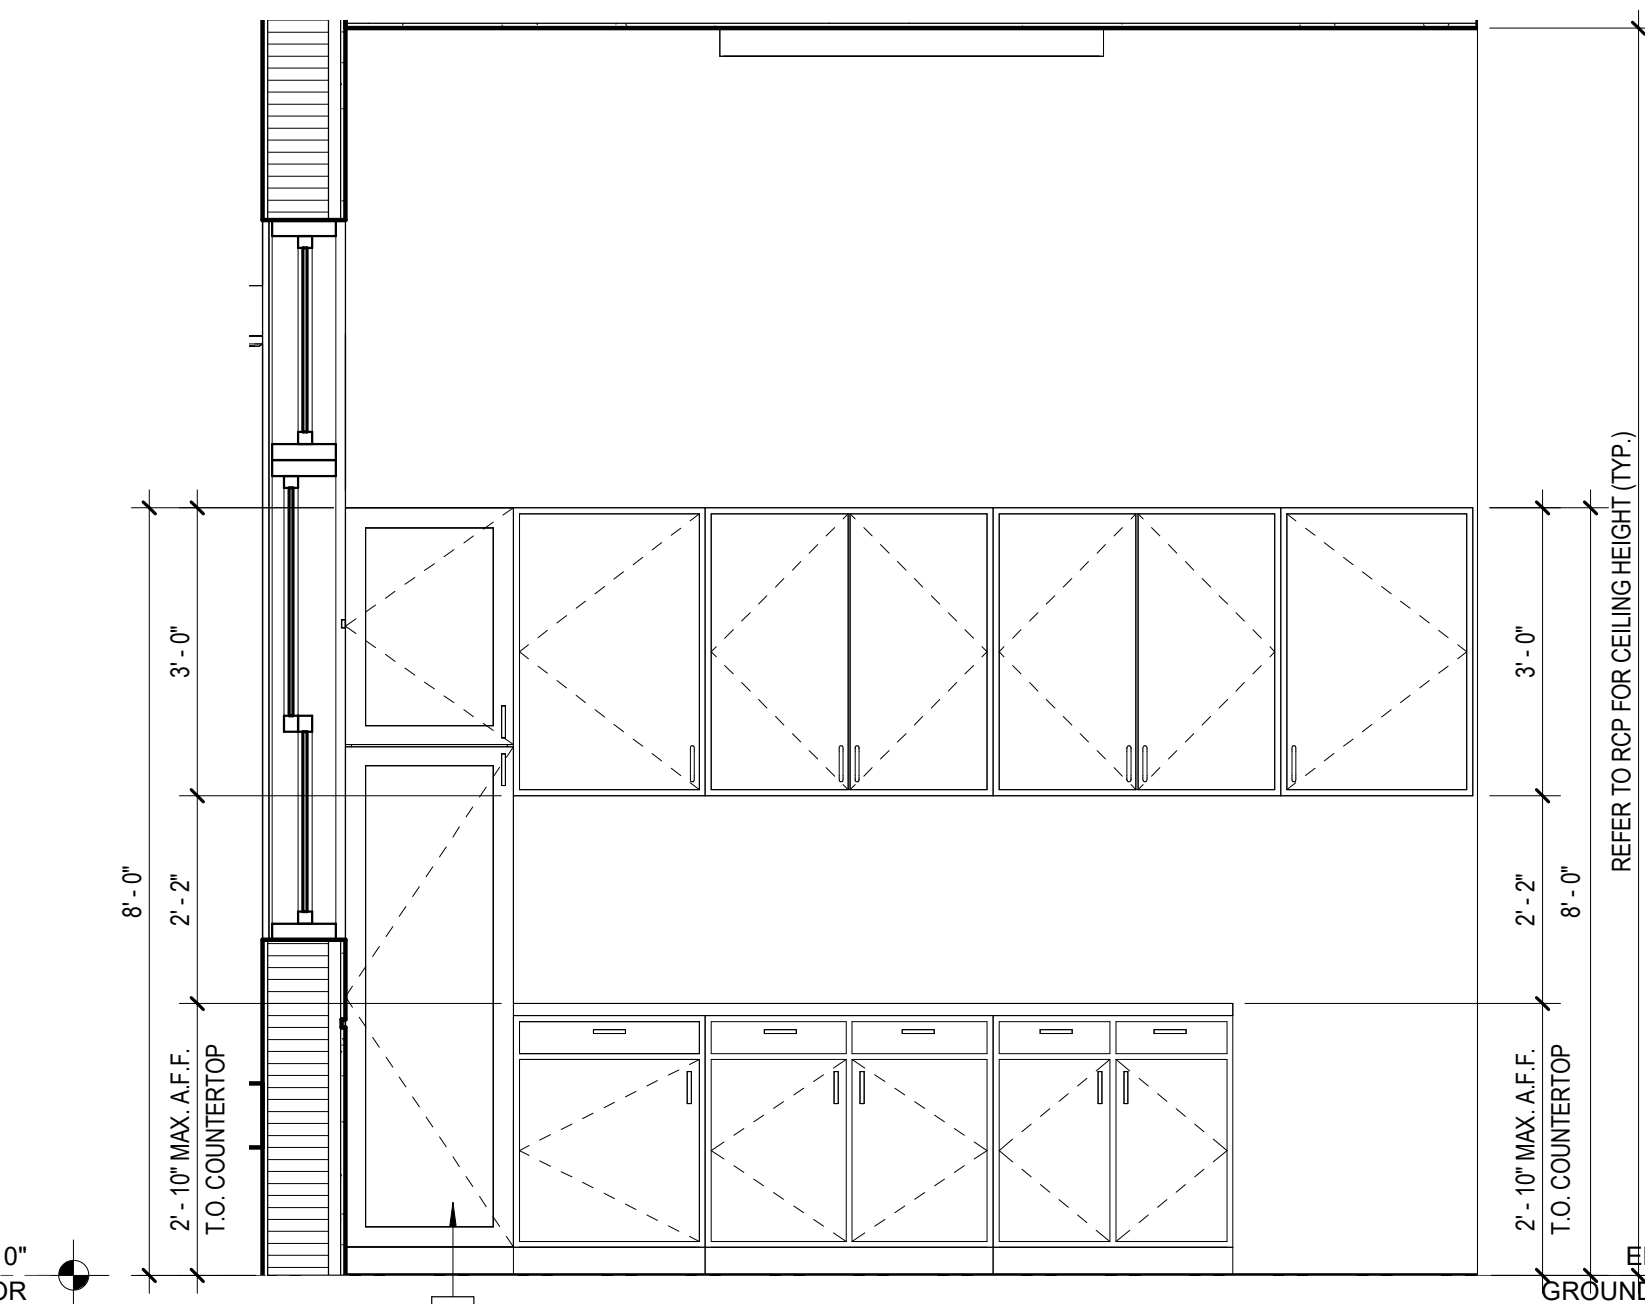

7 COPY/FILE ROOM ELEVATIONS
SCALE: 1/2" = 1'-0"

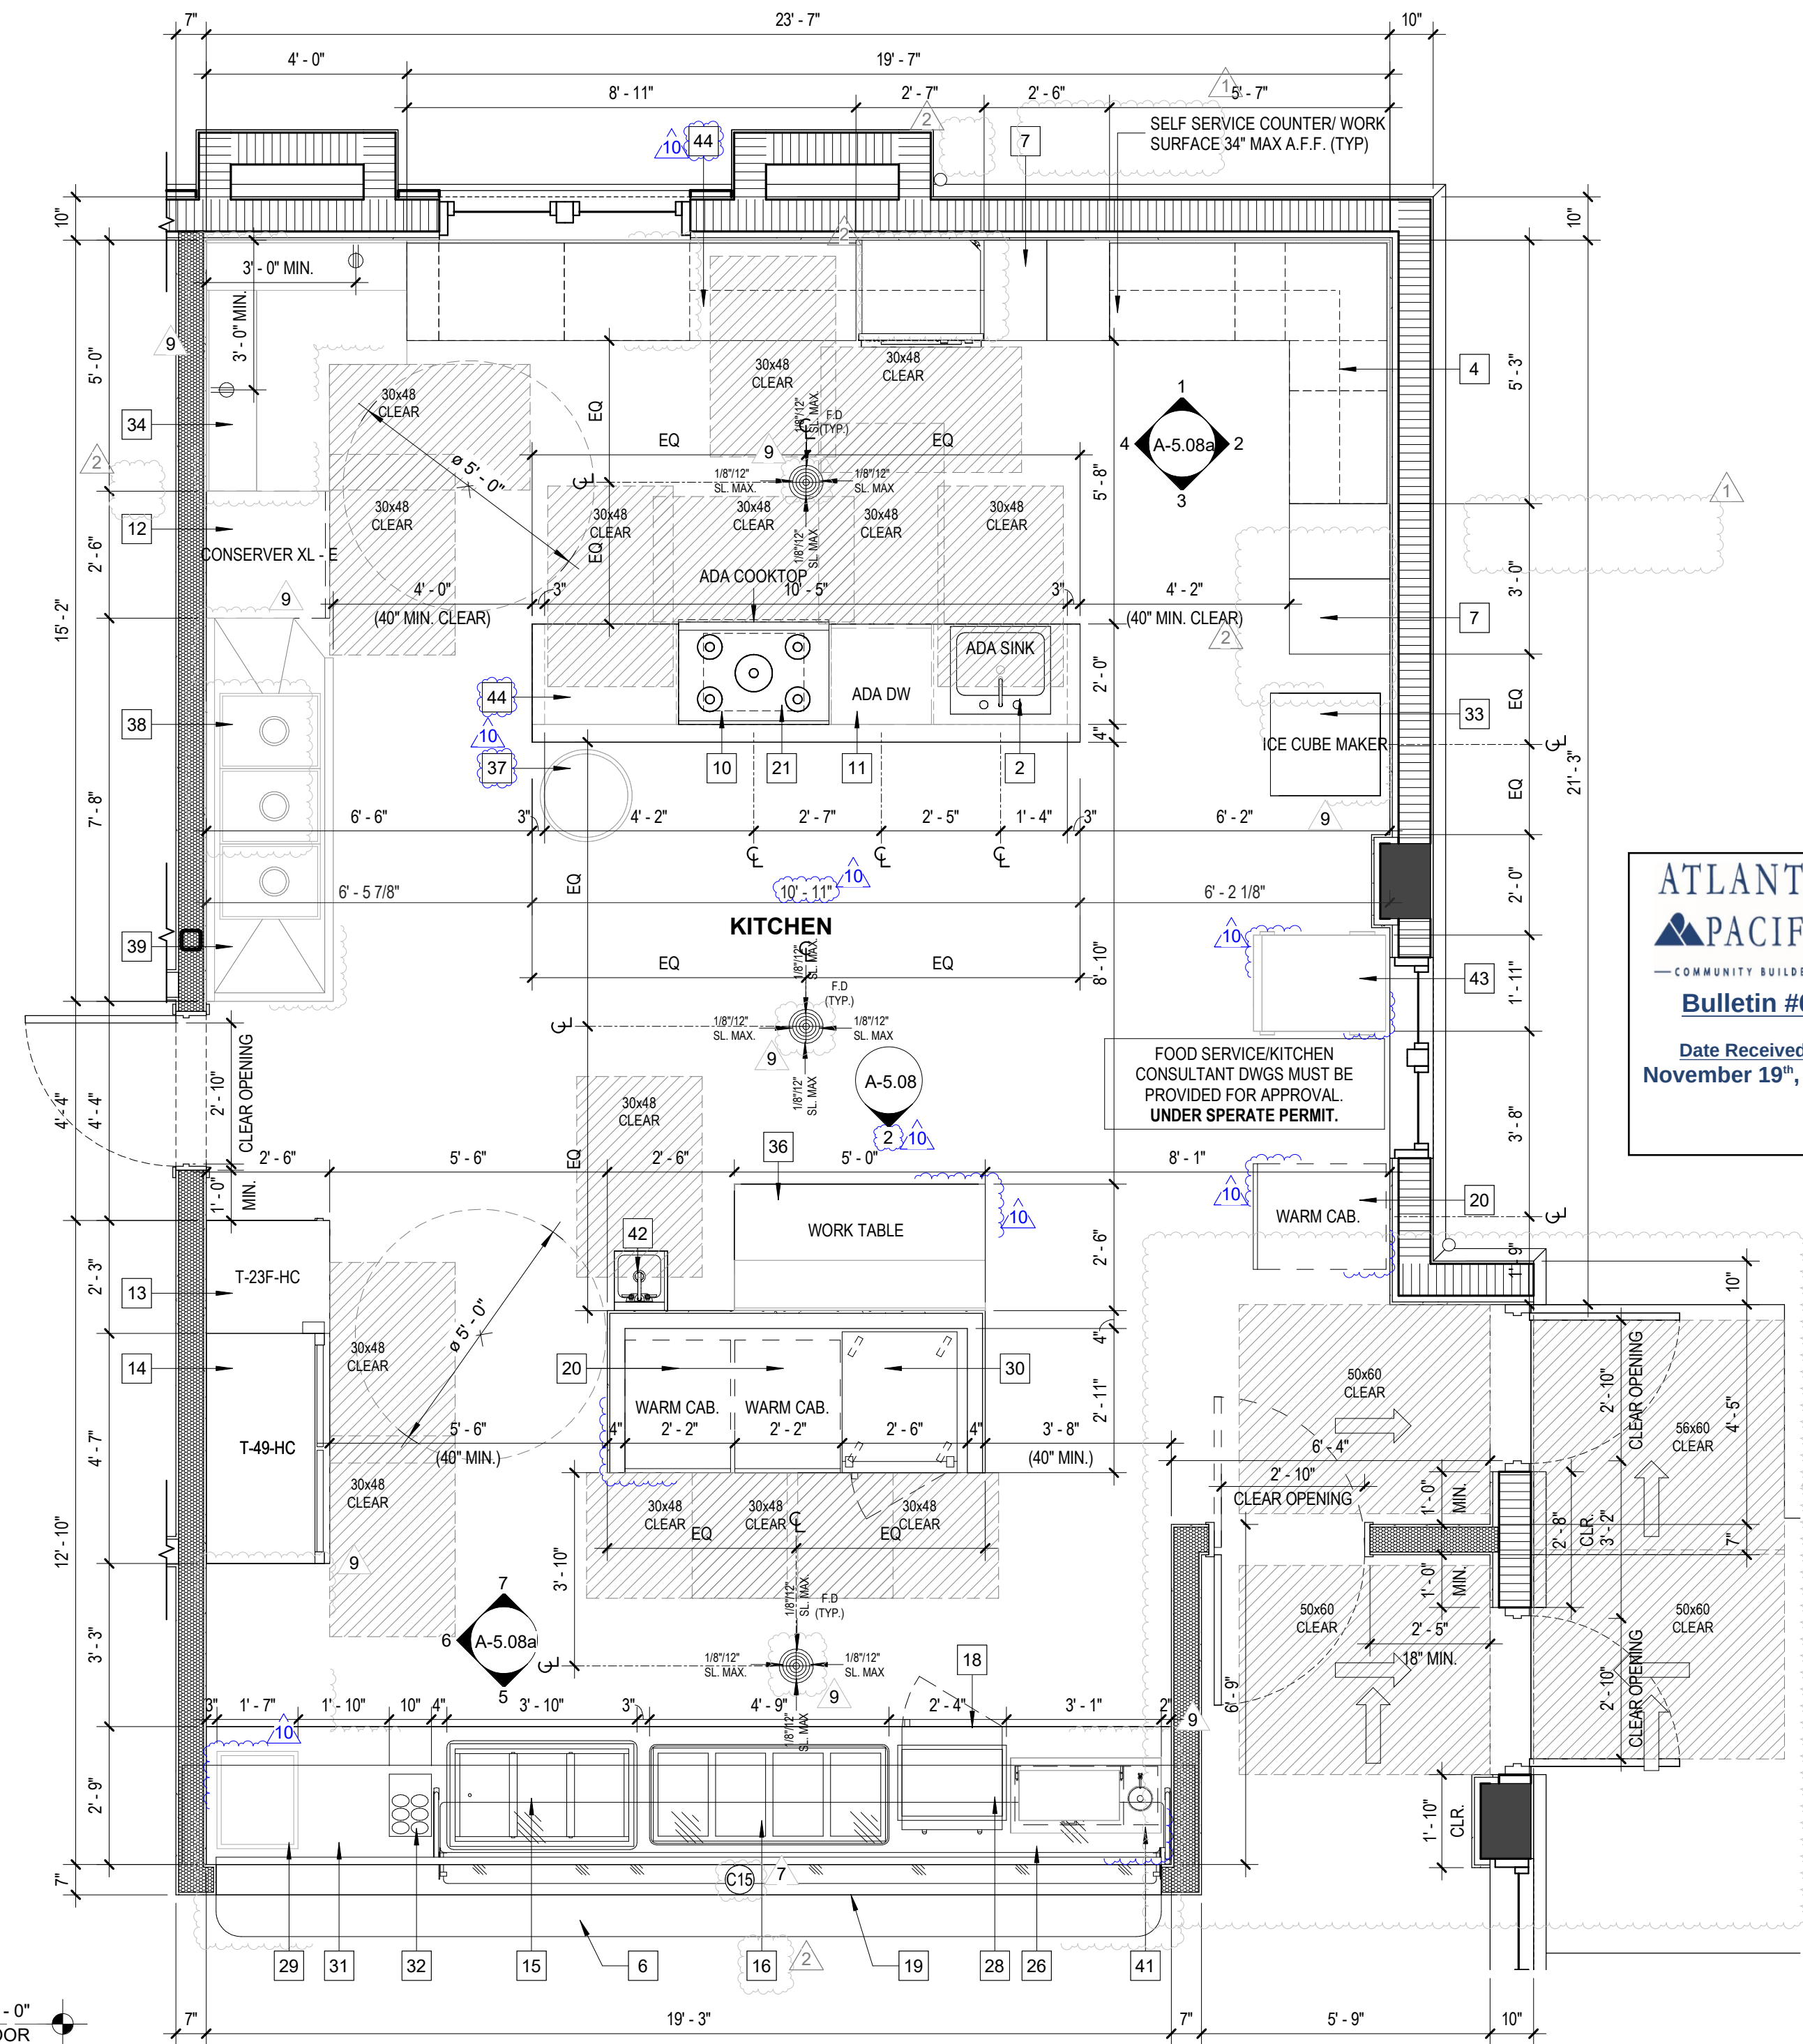


1 COMMUNITY CENTER KITCHEN
SCALE: 3/8" = 1'-0"

LEGEND	
1. (ENERGY STAR) ADA REFRIGERATOR (PROVIDE CONNECTION FOR ICE MAKER).	15. ATLAS COLD PAN RM-3.
2. ADA UNDERMOUNT SINK SELF RIM W/ GARBAGE DISPOSAL @ 34" MAX. A.F.F. & 6.5" DEEP MAX.	16. ATLAS HOT PAN WIH-4.
3. (ENERGY STAR) COUNTERTOP MICROWAVE.	17. CARVING REFRIGERATOR.
4. LINE OF CABINETS ABOVE. REFER TO ID FOR ADDITIONAL INFO.	18. REFRIGERATOR, UNDERCOUNTER (TUC-24-HC).
5. 34" MAX. A.F.F. HIGH COUNTERTOP W/ 4" HIGH BACKSPLASH.	19. FIRE RATED METAL OVERHEAD ROLLER DOOR. SUBMIT SHOP-DRAWINGS FOR APPROVAL PRIOR TO FABRICATION.
6. BUFFET/CAFETERIA, COUNTER WITH TRAY SLIDE.	20. CABINET, MOBILE, WARMING & HOLDING (VP18).
7. 24" DEPTH TALL CABINET.	21. ADA COOKTOP. TBD BY OWNER.
8. 12" WIDTH PANTRY CABINET W/ DEPTH TO MATCH INSTALLED REFRIGERATOR DEPTH & ALLOW FOR FULL SWING OF REFRIGERATOR DOORS.	22. SHELF, WALL MOUNT (BHS1272).
9. ROLL-OUT DRAWER/SHELF, BOTTOM HANDLE 15" MAX. A.F.F.	23. SHELF, WALL MOUNT (BHS1272PR).
10. ISLAND EXHAUST. REFER TO MEP FOR MORE INFO.	24. PROVIDE ADJUSTABLE SHELVING, LOWEST SHELF @ 15" A.F.F. AND @ LEAST ONE SHELF AT 48" A.F.F. ALL CLOSETS TO HAVE (5) SHELVES.
11. (ENERGY STAR) ADA DISHWASHER.	25. LINE DENOTES CABINETS OVER WORK SURFACE AREA @ 48" TO TOP OF SHELF.
12. WAREWASHER, DOOR TYPE, LOW TEMP CONSERVER XL-E.	26. BUFFET/CAFETERIA, SNEEZE GUARD.
13. REACH IN FREEZER (T-23F-HC).	27. SWITCHABLE WHITE LED UNDERCABINET.
14. REACH IN REFRIGERATOR (T-49-HC).	28. CARVING STATION, PORTABLE (IFW-61-GL-10PN).
29. DISPENSER, SELF-LEVELING GLASS/CUP (976).	44. WORK AREA.
30. REFRIGERATOR, REACH-IN, GLASS DOOR (STA1R-1G-HC).	
31. PLATE LAYDOWN AREA.	
32. FLATWARE HOLDER (CTFWH-6B).	
33. ICE MAKER WITH BIN, CUBE STYLE (ICE-U220FA).	
34. DISHTABLES L-SHAPE (CDT6-K6048SBK-R).	
35. STANDARD 16GA "D13PB" SINK (D13PB18244-2D18L).	
36. TABLE, WORK 16/300, 5" BACKSPLASH (STGR5-3072SBK).	
37. TRASH CAN, WITH CASTERS (PTC-32G).	
38. FAUCET, WALL MOUNT W/ PRE-RINSE SPR-8W14.	
39. DISHTABLE, STRAIGHT (DT3PB18244-2D18L).	
40. PROVIDE DOUBLE TOGGLE SWITCH FOR EXHAUST HOOD AT EDGE OF COUNTERTOP.	
41. DROP-IN, ICE CREAM FREEZER (DI-FR36-DW).	
42. SINK, HAND, WALL MOUNT (HS-30L).	
43. CART, ICE TRANSPORT (IIC-29).	

KITCHEN NOTE: REFER TO FOOD SERVICE OR KITCHEN CONSULTANT DWG. FOR DETAILS AND ADDITIONAL INFORMATION.

NOTE: REFER TO I.D. DWG. FOR DETAILS AND ADDITIONAL INFORMATION.

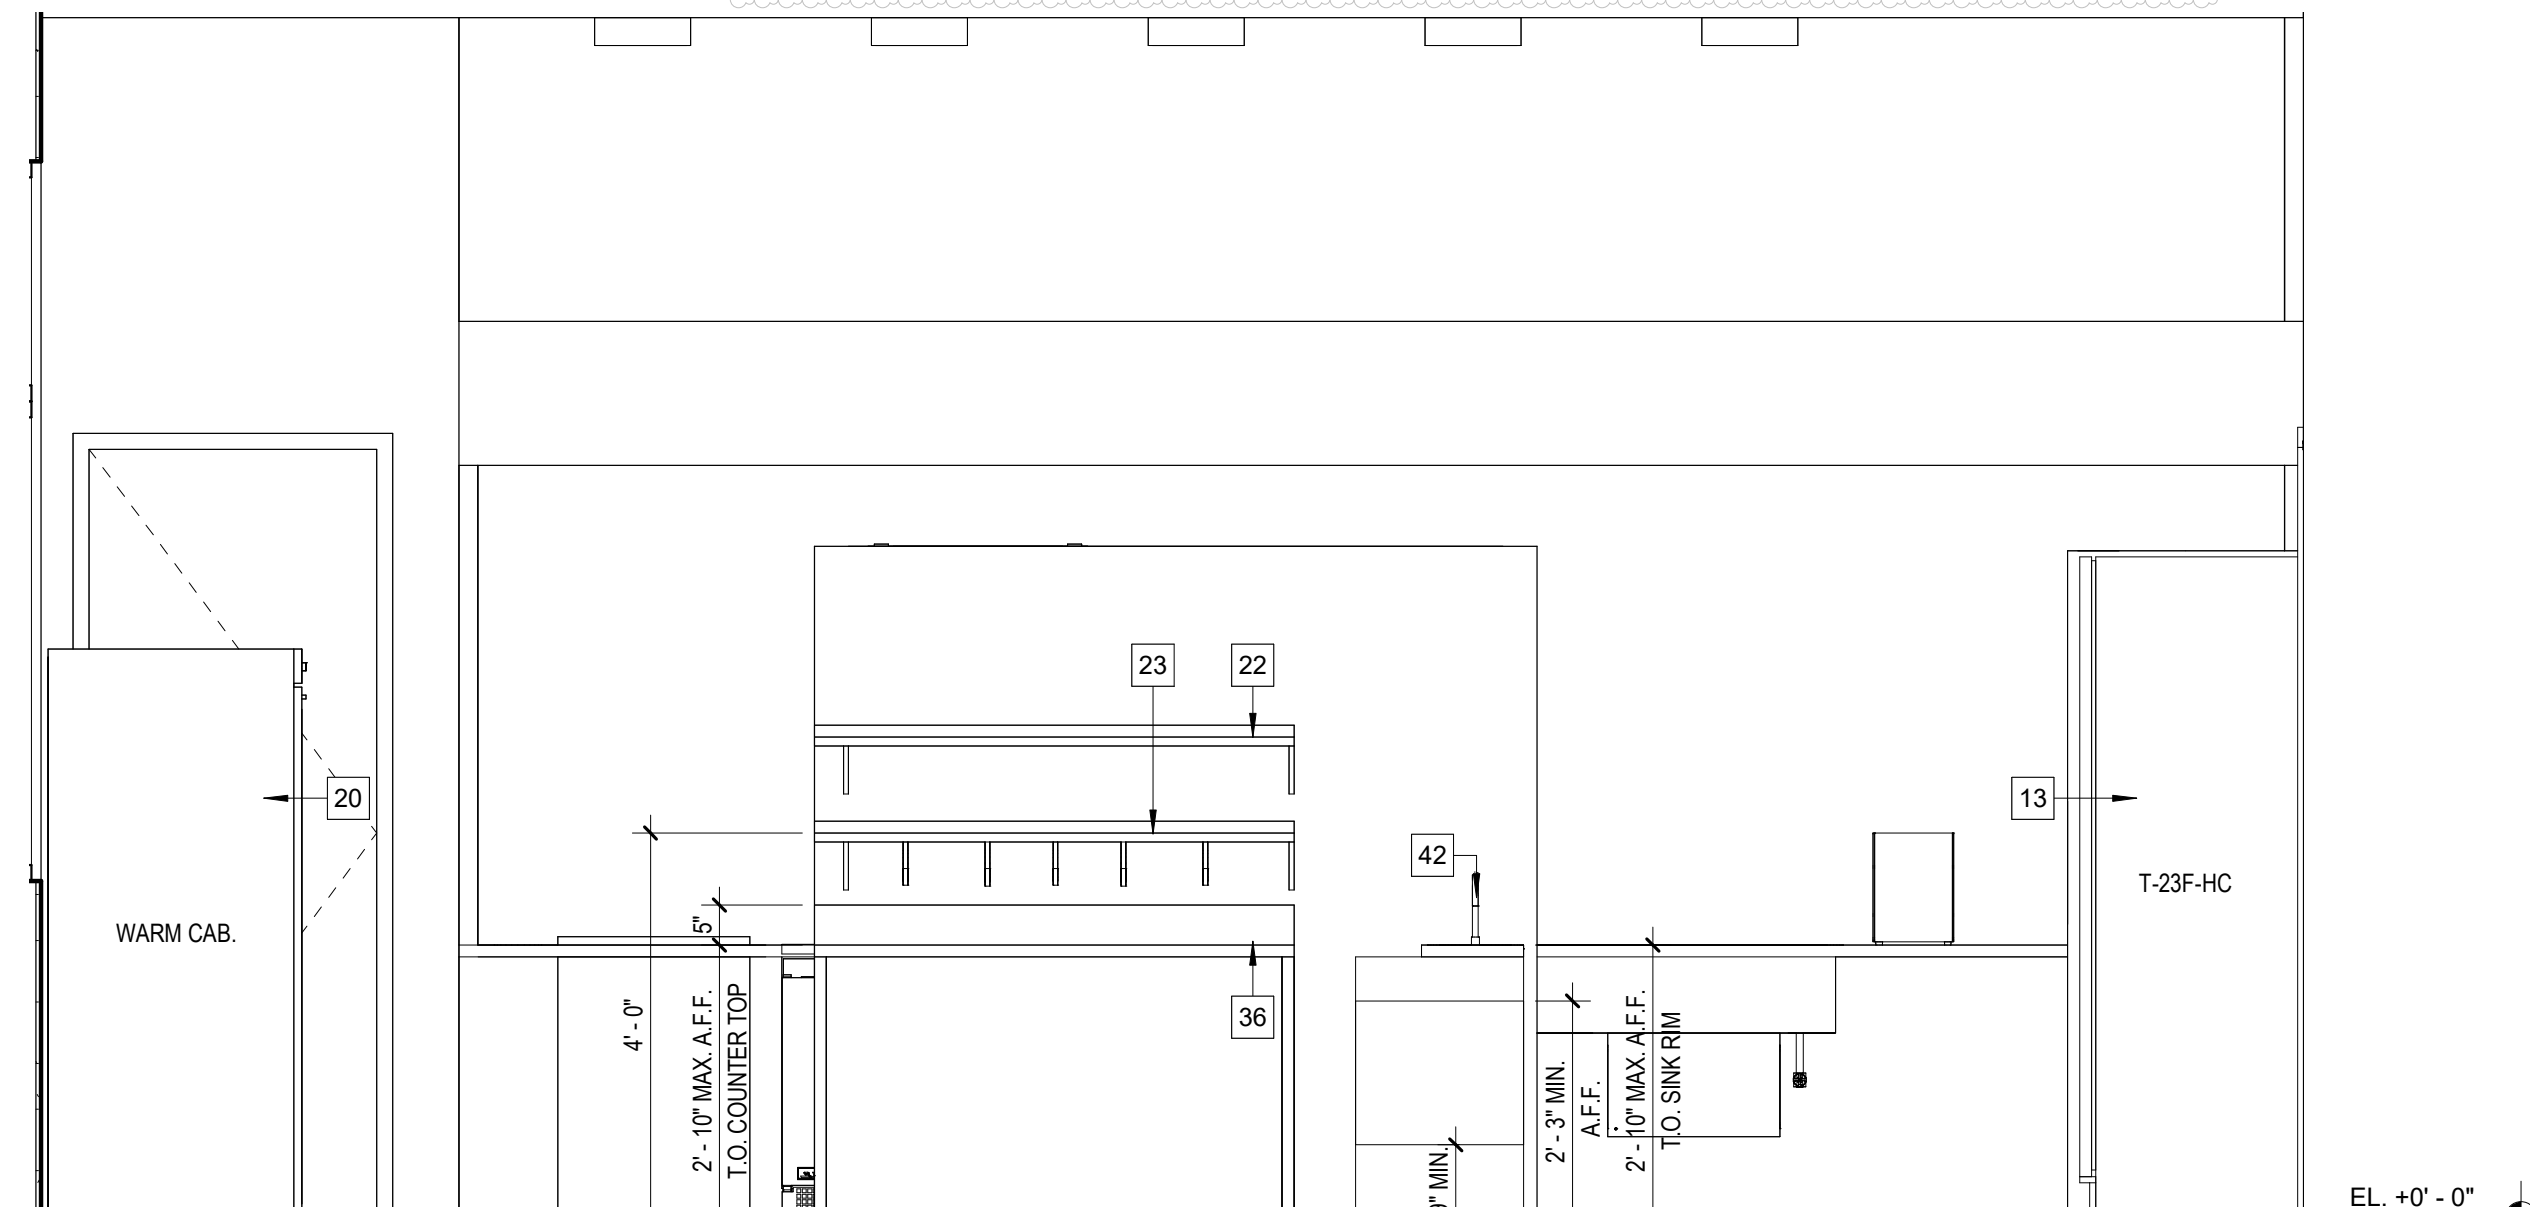

2 KITCHENETTE ELEVATION 8
SCALE: 1/2" = 1'-0"