



CORWILARCHITECTS
4210 LAGUNA ST. CORAL GABLES FL 33146
LIC. NO. AA-C002151 T.305.448.7383

PROJECT:



10951 SW 84th ST,
MIAMI-DADE, FLORIDA 33173

OWNER:



161 NW 6th ST, Ste. 1020
Miami, Florida 33136

PHASE:

PERMIT SET


ENLARGED KITCHENETTE (NO
COOKING)



Date Received:
November 19th, 2024

REVISIONS		
Rev #	Revision Description	Date
2	County Comments	11/20/20
7	Pre-con RFIs/Coord.	05/03/24
9	Coordin.	07/19/24
10	Coordin./Bulletin #6	09/20/24


SEAL:

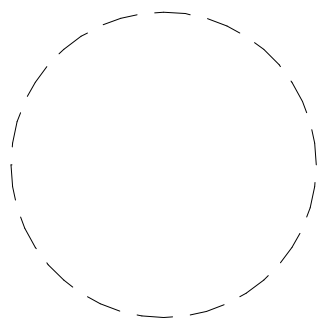

THIS DRAWING IS THE PROPERTY OF CORWIL ARCHITECTS INC.
UNLESS OTHERWISE PROVIDED FOR BY CONTRACT, THE
CONTENTS OF THIS DRAWING ARE CONFIDENTIAL AND
SHALL NOT BE TRANSMITTED TO ANY OTHER PARTY
EXCEPT AS AGREED TO BY THE ARCHITECT/ENGINEERS.

DATE: 5-18-2020
JOB No.: 2019-20
DRAWN BY: MA, CM, JM, JW, FG
APPR BY: AMC
PRINTED: 11/25/2024


A-5.08a

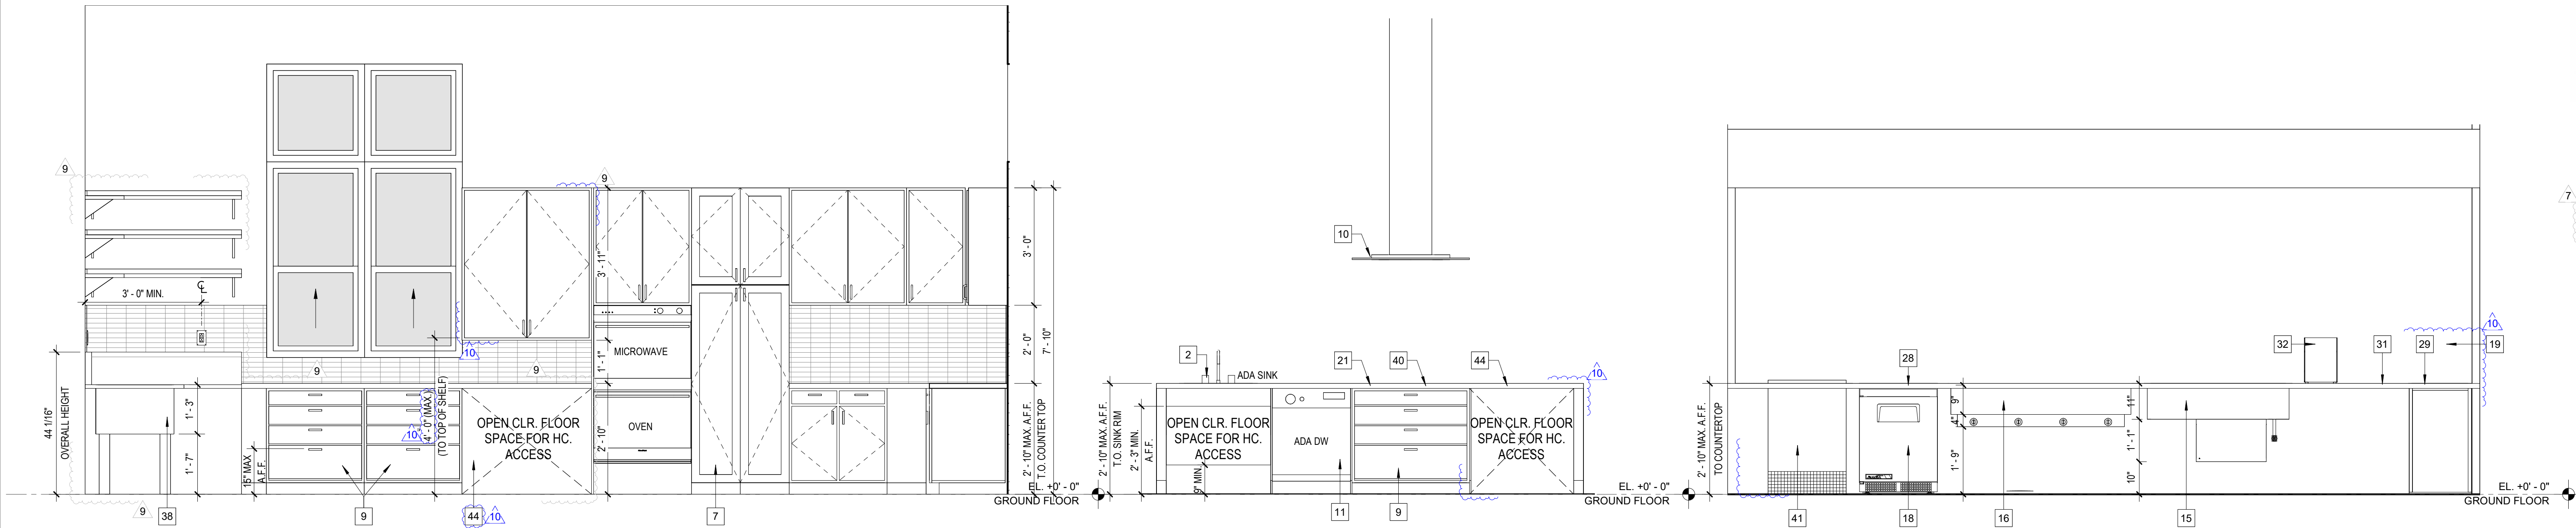

1 KITCHENETTE ELEVATION 1
SCALE: 1/2" = 1'-0"

3 KITCHENETTE ELEVATION 3
SCALE: 1/2" = 1'-0"

5 KITCHENETTE ELEVATION 5
SCALE: 1/2" = 1'-0"

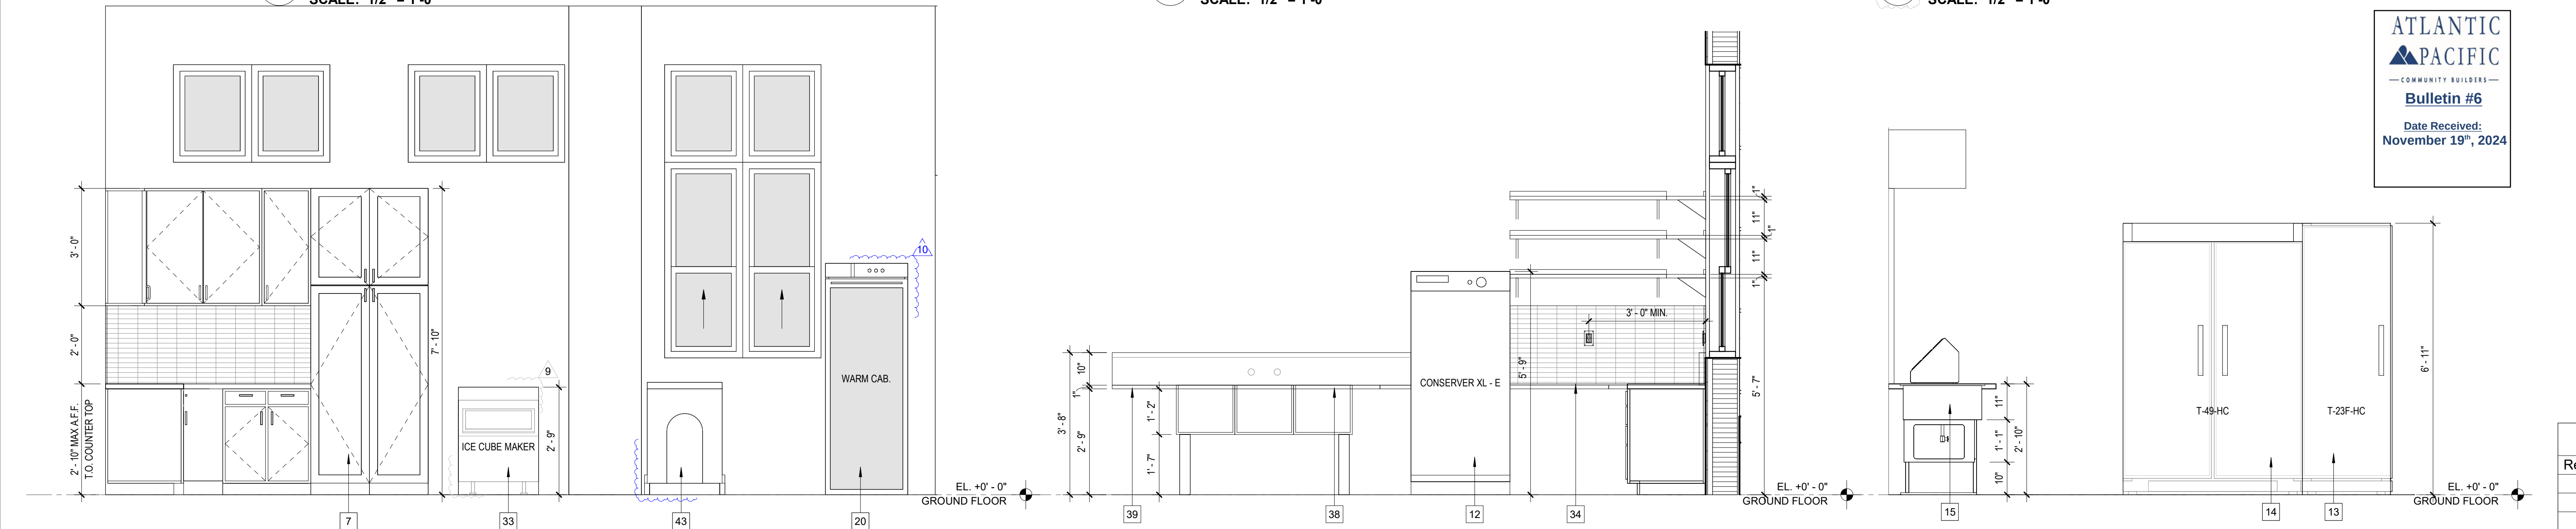


2 KITCHENETTE ELEVATION 2
SCALE: 1/2" = 1'-0"

4 KITCHENETTE ELEVATION 4
SCALE: 1/2" = 1'-0"

6 KITCHENETTE ELEVATION 6
SCALE: 1/2" = 1'-0"

LEGEND		
1. (ENERGY STAR) ADA REFRIGERATOR (PROVIDE CONNECTION FOR ICE MAKER).	15. ATLAS COLD PAN RM-3.	29. DISPENSER, SELF-LEVELING GLASS/CUP (976).
2. ADA UNDERMOUNT SINK SELF RIM W/ GARBAGE DISPOSAL @ 34" MAX. A.F.F. & 6.5" DEEP MAX.	16. ATLAS HOT PAN WH-4.	30. REFRIGERATOR, REACH-IN, GLASS DOOR (STA1R-1G-HC).
3. (ENERGY STAR) COUNTERTOP MICROWAVE.	17. CARVING REFRIGERATOR.	31. PLATE LAYDOWN AREA.
4. LINE OF CABINETS ABOVE. REFER TO ID FOR ADDITIONAL INFO.	18. REFRIGERATOR, UNDERCOUNTER (TUC-24-HC).	32. FLATWARE HOLDER (CTFWH-6B).
5. 34" MAX. A.F.F. HIGH COUNTERTOP W/ 4" HIGH BACKSPLASH.	19. FIRE RATED METAL OVERHEAD ROLLER DOOR. SUBMIT SHOP-DRAWINGS FOR APPROVAL PRIOR TO FABRICATION.	33. ICE MAKER WITH BIN, CUBE STYLE (ICE-U220FA).
6. BUFFET/CAFETERIA COUNTER WITH TRAY SLIDE.	20. CABINET, MOBILE, WARMING & HOLDING (VP18).	34. DISHTABLES L-SHAPE (CDT6-K6048SBK-R).
7. 24" DEPTH TALL CABINET.	21. ADA COOKTOP. TBD BY OWNER.	35. STANDARD 16GA "D13PB" SINK (D13PB18244-2D18L).
8. 12" WIDTH PANTRY CABINET W/ DEPTH TO MATCH INSTALLED REFRIGERATOR DEPTH & ALLOW FOR FULL SWING OF REFRIGERATOR DOORS.	22. SHELF, WALL MOUNT (BHS1272).	36. TABLE, WORK 16/300, 5" BACKSPLASH (ST6R5-3072SBK).
9. ROLL-OUT DRAWER/SHELF, BOTTOM HANDLE 15" MAX. A.F.F.	23. SHELF, WALL MOUNT (BHS1272PR).	37. TRASH CAN, WITH CASTERS (PTC-32G).
10. ISLAND EXHAUST. REFER TO MEP FOR MORE INFO.	24. PROVIDE ADJUSTABLE SHELVING, LOWEST SHELF @ 15" A.F.F. AND @ LEAST ONE SHELF AT 48" A.F.F. ALL CLOSETS TO HAVE (5) SHELVES.	38. FAUCET, WALL MOUNT W/ PRE-RINSE SPR-8W14.
11. (ENERGY STAR) ADA DISHWASHER.	25. LINE DENOTES CABINETS OVER WORK SURFACE AREA @ 48" TO TOP OF SHELF.	39. DISHTABLE, STRAIGHT (DT3PB18244-2D18L).
12. WAREWASHER, DOOR TYPE, LOW TEMP CONSERVER XL-E.	26. BUFFET/CAFETERIA, SNEEZE GUARD.	40. PROVIDE DOUBLE TOGGLE SWITCH FOR EXHAUST HOOD AT EDGE OF COUNTERTOP.
13. REACH IN FREEZER (T-23F-HC).	27. SWITCHABLE WHITE LED UNDERCABINET.	41. DROP-IN, ICE CREAM FREEZER (DI-FR36-DW).
14. REACH IN REFRIGERATOR (T-49-HC).	28. CARVING STATION, PORTABLE (IFW-61-GL-10PN).	42. SINK, HAND, WALL MOUNT (HS-30L).
		43. CART, ICE TRANSPORT (IIC-29).
		44. WORK AREA.
KITCHEN NOTE: REFER TO FOOD SERVICE OR KITCHEN CONSULTANT DWG. FOR DETAILS AND ADDITIONAL INFORMATION.		
NOTE: REFER TO I.D. DWG. FOR DETAILS AND ADDITIONAL INFORMATION.		

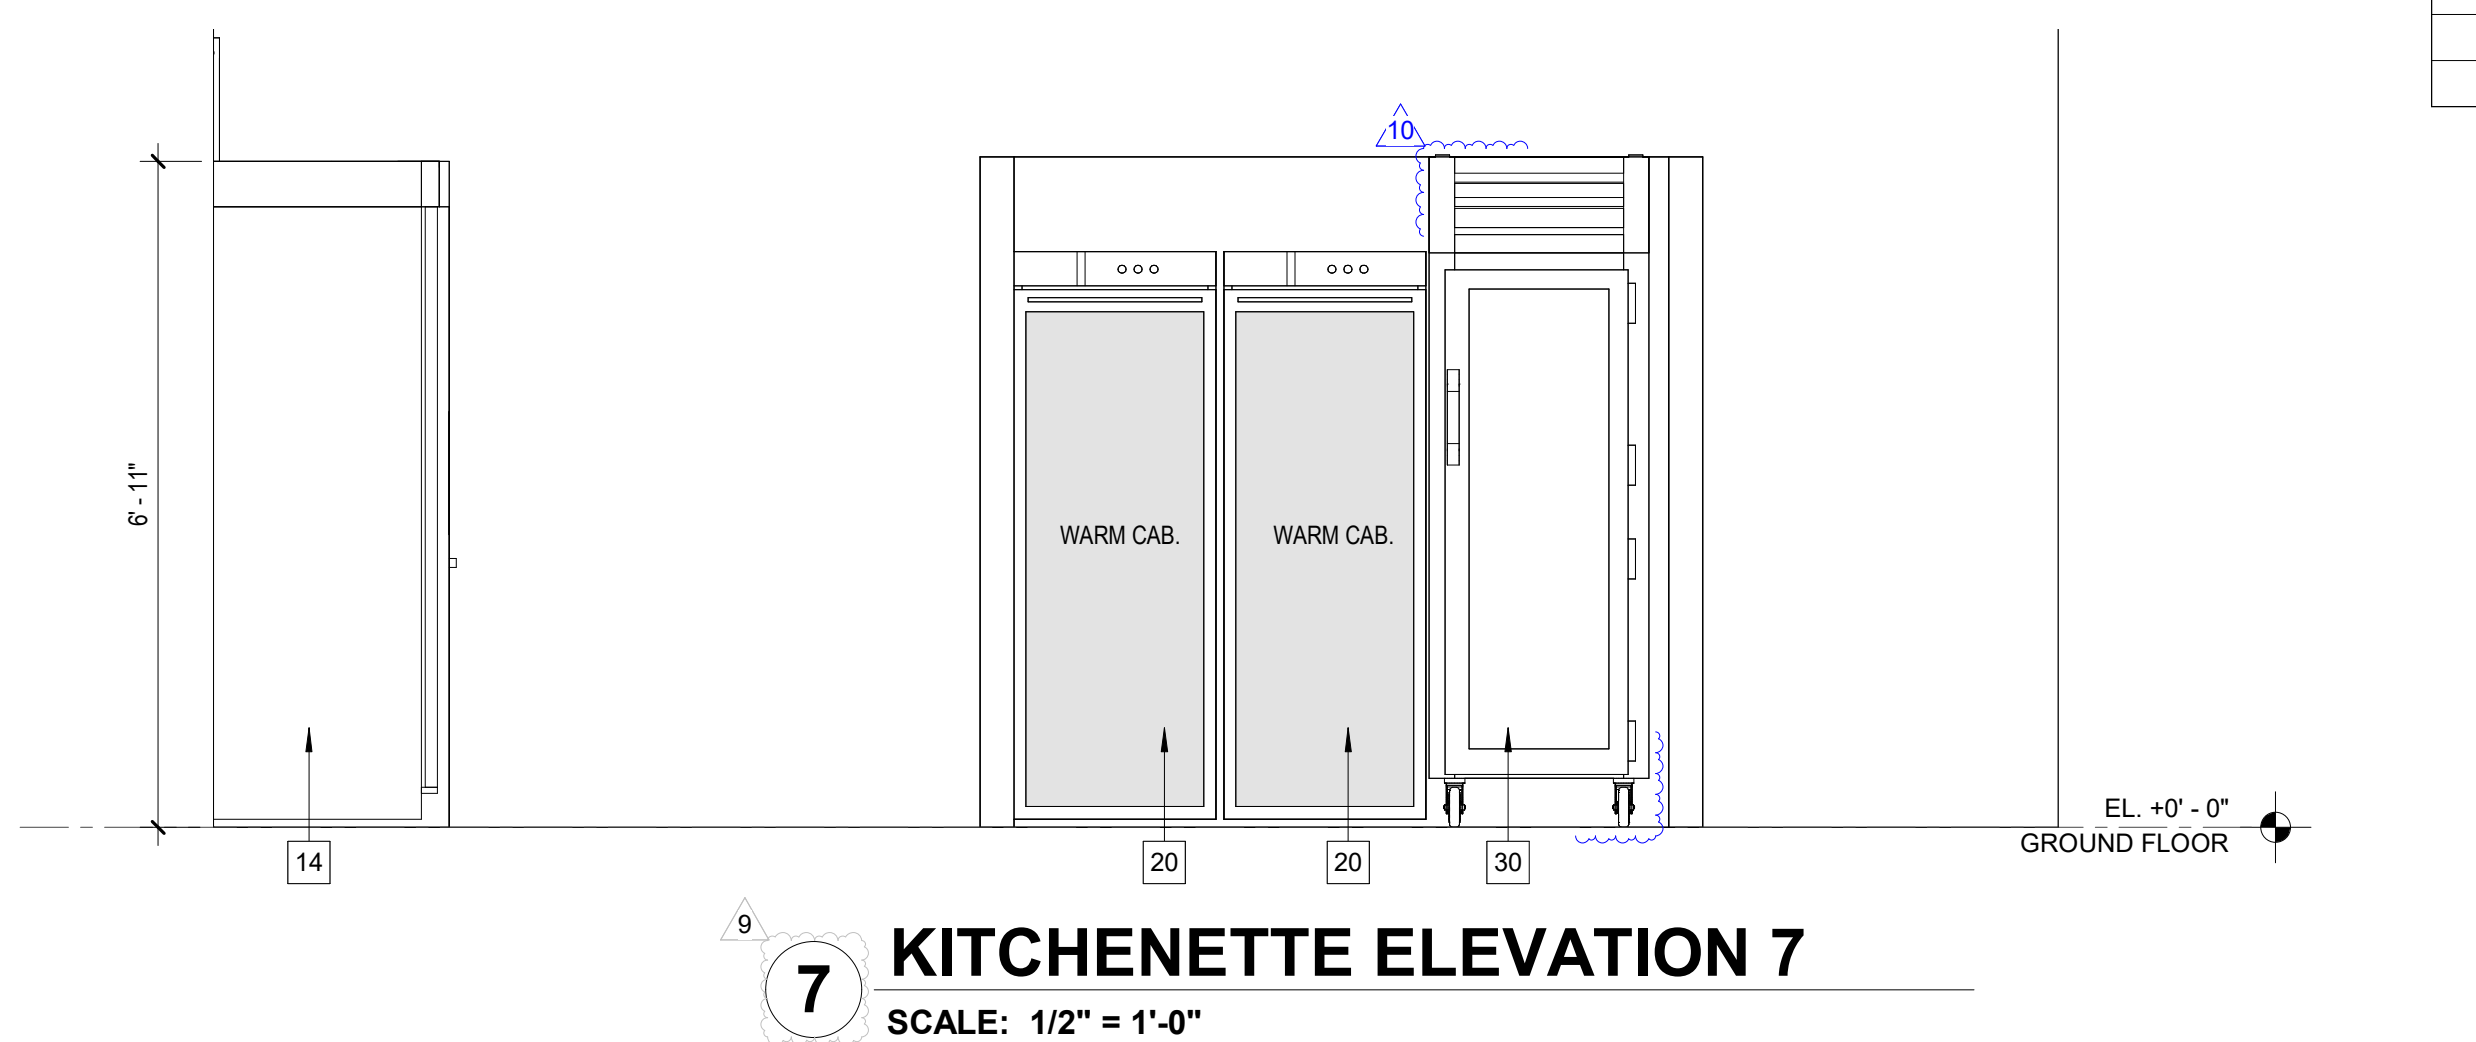

7 KITCHENETTE ELEVATION 7
SCALE: 1/2" = 1'-0"