



CORWILARCHITECTS
4210 LAGUNA ST. CORAL GABLES FL 33146
LIC. NO. AA-C002151 T.305.448.7383

PROJECT:



10951 SW 84th ST,
MIAMI-DADE, FLORIDA 33173

OWNER:



161 NW 6th ST, Ste. 1020
Miami, Florida 33136

PHASE:

PERMIT SET

BLDG A - 3RD FLOOR PLAN

REVISIONS

Rev #	Revision Description	Date
1	Bldg Review Cmt	09/30/20
2	County Comments	11/20/20
3	County Comments	01/08/21
7	Pre-con RFIs/Coord.	05/03/24
8	Bulletin #4	05/29/24
9	Coordin.	07/19/24
10	Coordin./Bulletin #6	09/20/24

SEAL:

THIS DRAWING IS THE PROPERTY OF CORWIL ARCHITECTS INC.
UNLESS OTHERWISE PROVIDED FOR BY CONTRACT, THE
CONTENTS OF THIS DRAWING ARE CONFIDENTIAL AND
SHALL NOT BE TRANSMITTED TO ANY OTHER PARTY
EXCEPT AS AGREED TO BY THE ARCHITECT/ENGINEERS.

DATE: 5-18-2020
JOB No.: 2019-20
DRAWN BY: MAC, CM, JM, JW, FG
APPR BY: AMC
PRINTED: 11/13/2024

A-2.02

WATERPROOFING LEGEND


- (A) STEGO WRAP 15-MIL VAPOR BARRIER BELOW SLAB
(B) POLYIMIDE HS EPOXY COATING (WALLS) AND EUCLID CHEMICAL EUCOPOXY TUF COAT ON FLOORS
(C) EUCLID TAMOSEAL CEMENTITIOUS WATERPROOFING
(D) PROVIDED PROTECTIVE COATING (VULKEM 350/351 OVER MSUP PRIMER SANDED TO REDUCE SKID. SYSTEM TRANSITION 6" UP PERIMETER WALLS) PROVIDE TREMCO'S DYMONIC 100 CANT BEAD AT ALL SUBSTRATE TRANSITIONS.
(E) TREMCO VULKEM 350/351 COATING, SANDED TO REJECTION. TERMINATE 6" UP, PERIMETER WALLS.
(F) TREMCO AMPHIBIA MEMBRANE WATERPROOFING ENCAPSULATING ELEVATOR PIT
(G) TREMCO TREMPLY SINGLE PLY ROOFING MEMBRANE OVER LIGHT WEIGHT CONCRETE 60 MILS MIN.
(H) XYPEX CRYSTALLINE CEMENTITIOUS WATERPROOFING
(I) MASTERPROTECH H1000 BASF CLEAR SEALER

WALL & SYMBOL LEGEND

- REINF. CMU WALL W/O FURRING
REINF. CMU WALL W/O FURRING (2 HOUR RATED)
REINF. CMU WALL W/O FURRING (3 HOUR RATED)
REINF. SHEAR WALL (2 HOUR RATED)
8" LOW WALL @ 42" MIN.
TYP. METAL STUD PARTITION WALL
TYP. 1 HOUR TENANT SEPARATION/SMOKE BARRIER METAL STUD PARTITION WALL - REFER TO OVERALL FLOOR PLAN FOR WALL
2 HOUR UL RATED SHAFT WALL
DENOTES AREA OF GYPSUM WALLBOARD DROP DOWN CEILING OR GWB SOFFIT AREA 7'-6" MIN. (UNLESS OTHERWISE NOTED)
- WINDOW TYPE. REFER TO WINDOW SCHEDULE
DOOR NUMBER. REFER TO DOOR SCHEDULE
KEYNOTE NUMBER. REFER TO KEYNOTE LEGEND
STOREFRONT TYPE / LOUVER TYPE
CENTER LINE
WALL TYPE. SEE SHEET A-8.01
PAVEMENT STRIPED ZONE- NO PARKING, NO DRIVING & NO STANDING AREA
DENOTES QUANTITY
DENOTES 1/2" MAX. F.F. THRESHOLD

BUILDING A 3RD FLR UNIT BREAKDOWN

UNIT TYPE	# OF UNITS
A1	5
A2 FA	1
A3	1
B1	1
B2 FA	1
TOTAL	9

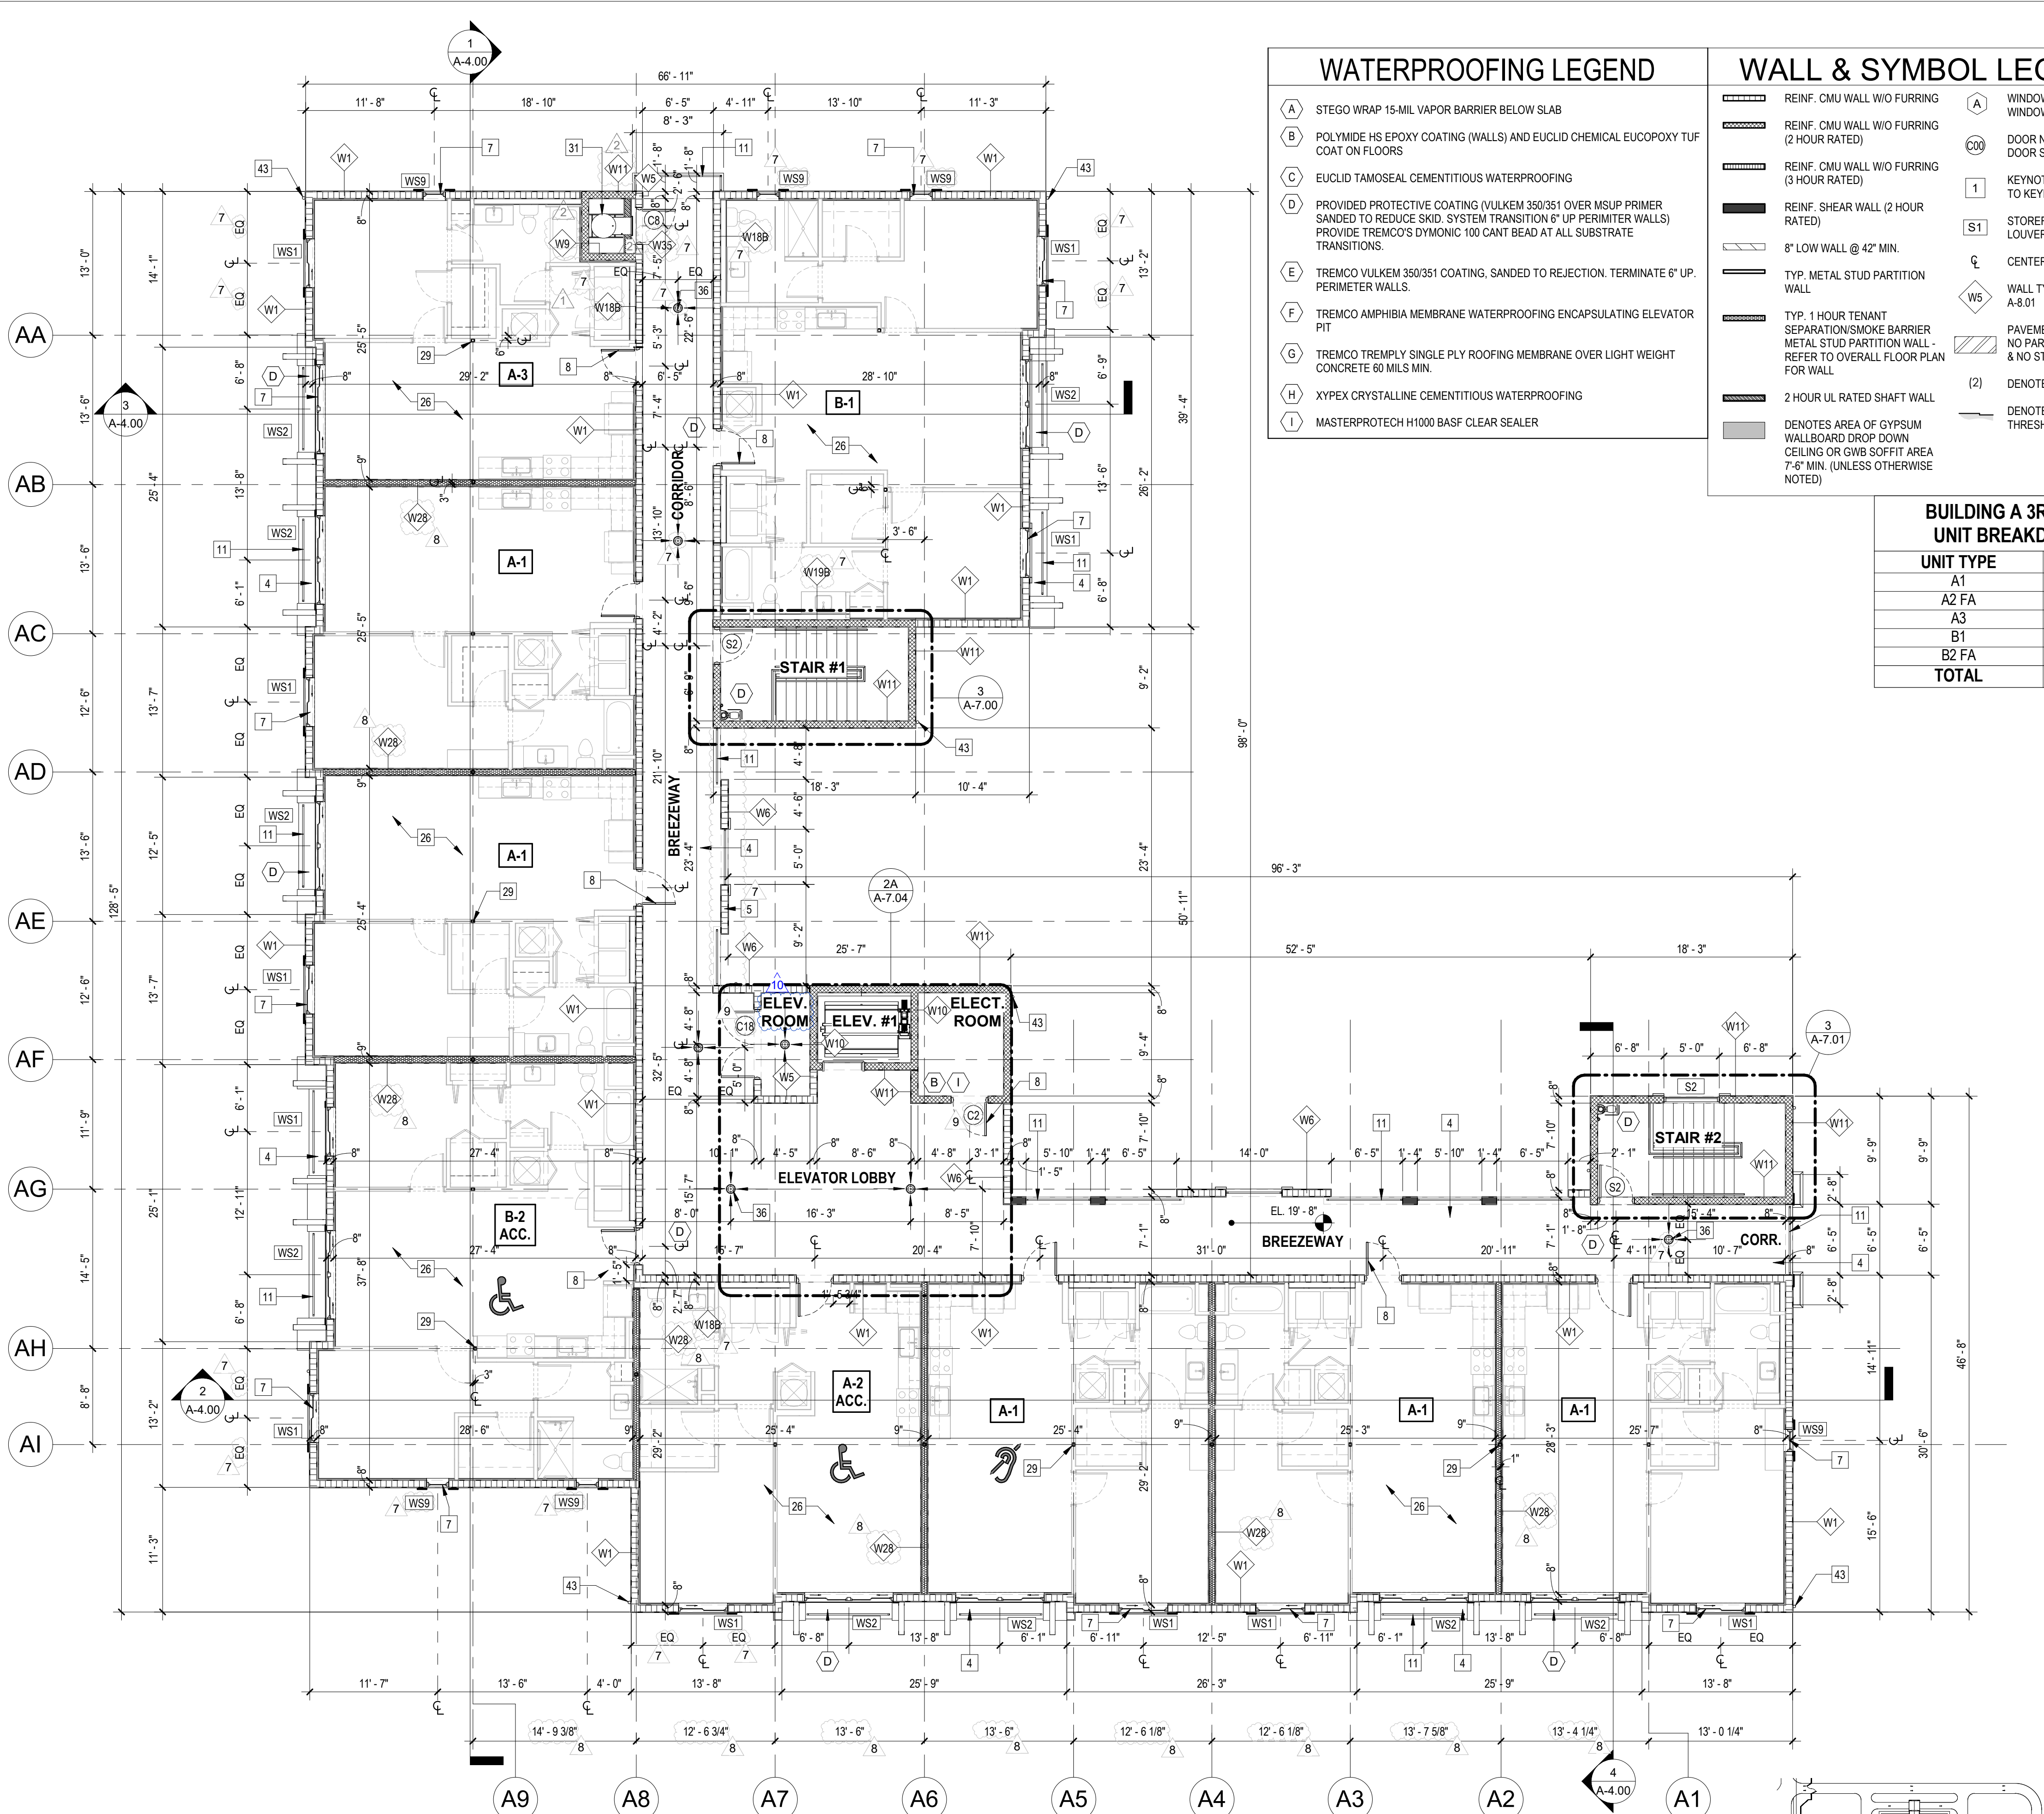

BLDG A - 3RD FLOOR

SCALE: 1/8" = 1'-0"



BUILDING A KEY PLAN

N.T.S.

