



CORWILARCHITECTS
4210 LAGUNA ST. CORAL GABLES FL 33146
LIC. NO. AA-C002151 T.305.448.7383

PROJECT:
Casa Familia
Exceptional Housing for Exceptional People


10951 SW 84th ST,
MIAMI-DADE, FLORIDA 33173

OWNER:
**ATLANTIC
PACIFIC**
COMMUNITIES


161 NW 6th ST, Ste. 1020
Miami, Florida 33136

PHASE:
PERMIT SET

BLDG A - LOW ROOF PLAN


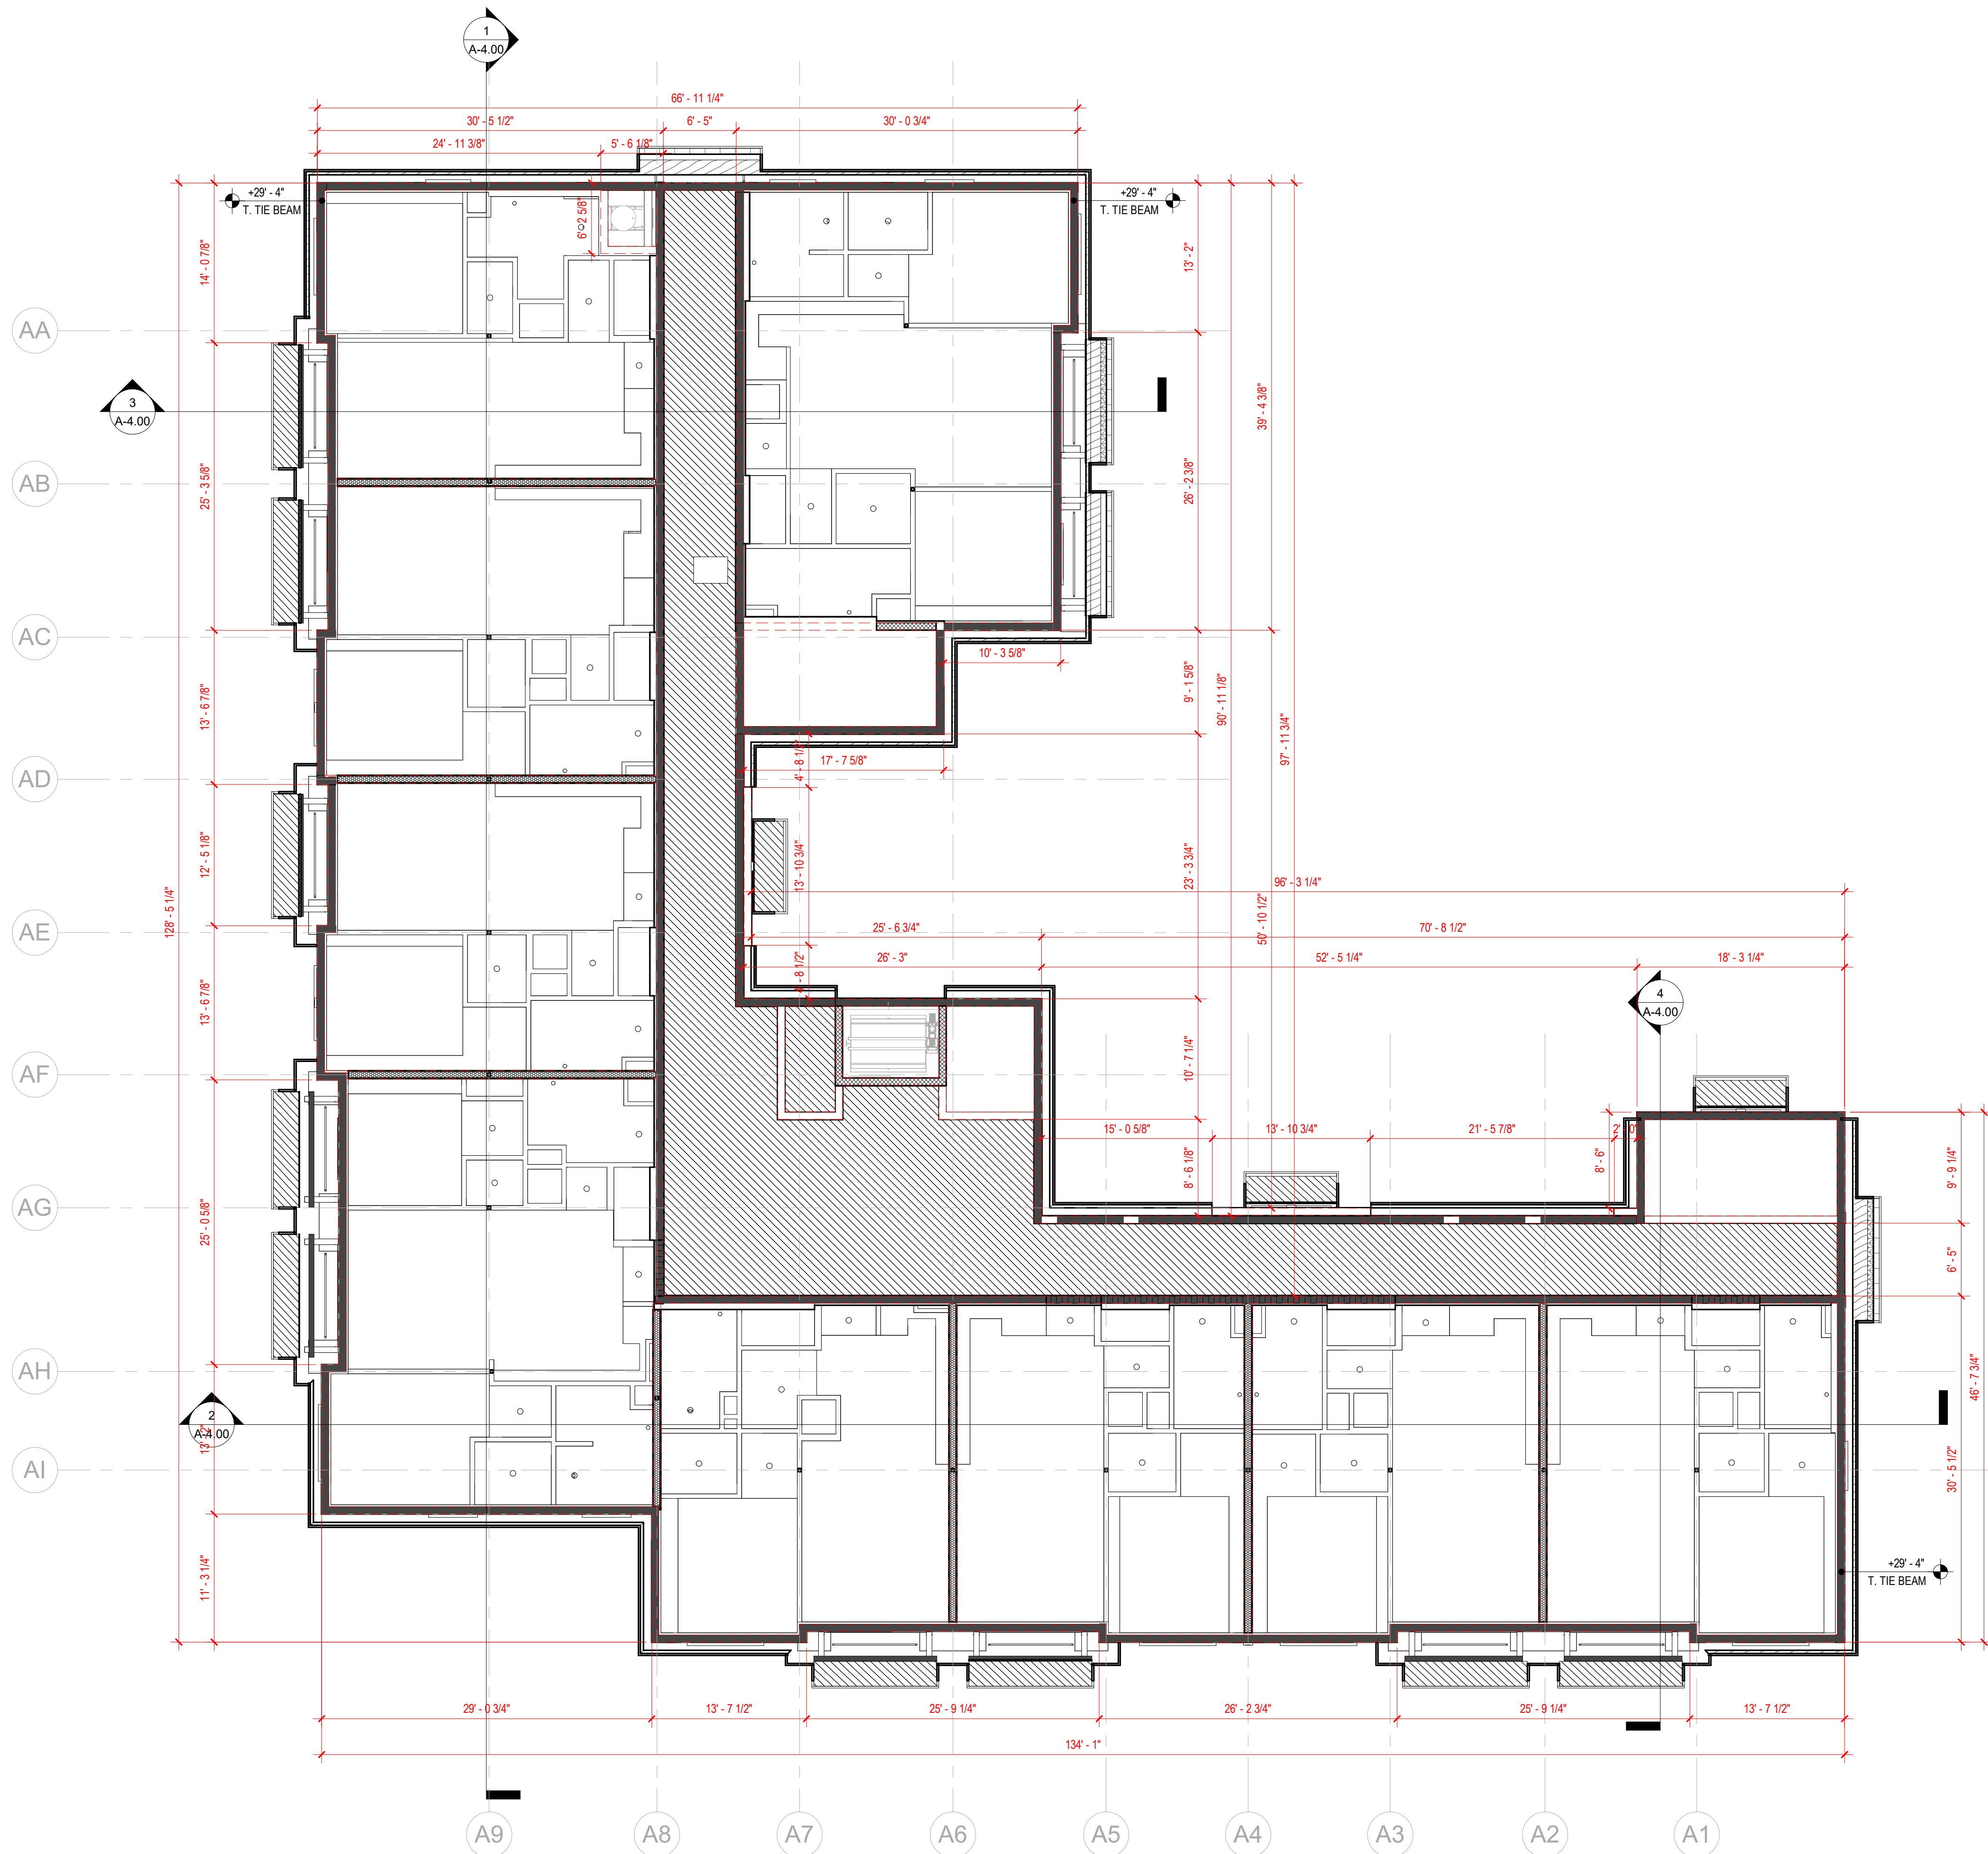


BLDG A - LOW ROOF PLAN
SCALE: 1/8" = 1'-0"

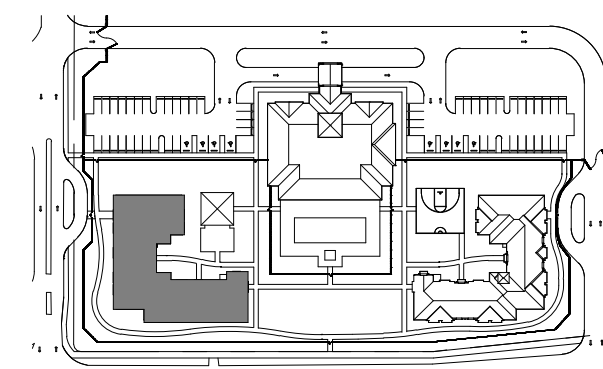

BUILDING A KEY PLAN
N.T.S.

REVISIONS		
Rev #	Revision Description	Date
10	Coordin./Bulletin #6	09/20/24

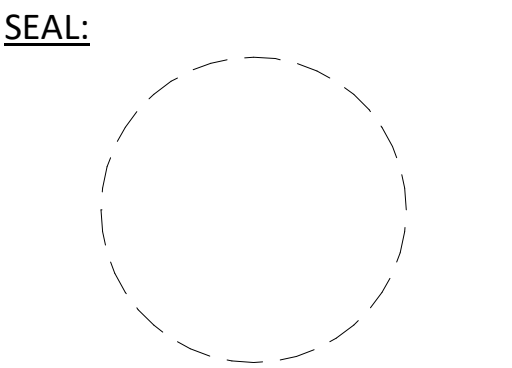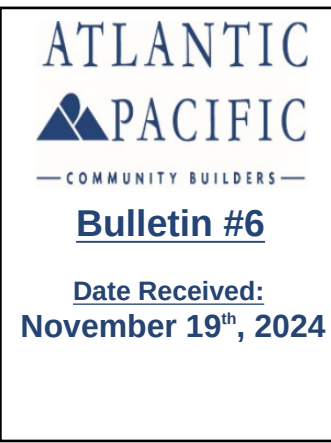

THIS DRAWING IS THE PROPERTY OF CORWIL ARCHITECTS INC.
UNLESS OTHERWISE PROVIDED FOR BY CONTRACT, THE
CONTENTS OF THIS DRAWING ARE CONFIDENTIAL AND
SHALL NOT BE TRANSMITTED TO ANY OTHER PARTY
EXCEPT AS AGREED TO BY THE ARCHITECT/ENGINEERS.

DATE: 5-18-2020
JOB No.: 2019-20
DRAWN BY: CDM
APPR BY: AMC
PRINTED: 11/13/2024

A-2.03A