



CORWILARCHITECTS
4210 LAGUNA ST. CORAL GABLES FL 33146
LIC. NO. AA-C002151 T.305.448.7383

PROJECT:



10951 SW 84th ST,
MIAMI-DADE, FLORIDA 33173

OWNER:




161 NW 6th ST, Ste. 1020
Miami, Florida 33136

PHASE:


PERMIT SET

GROUND SITE PLAN

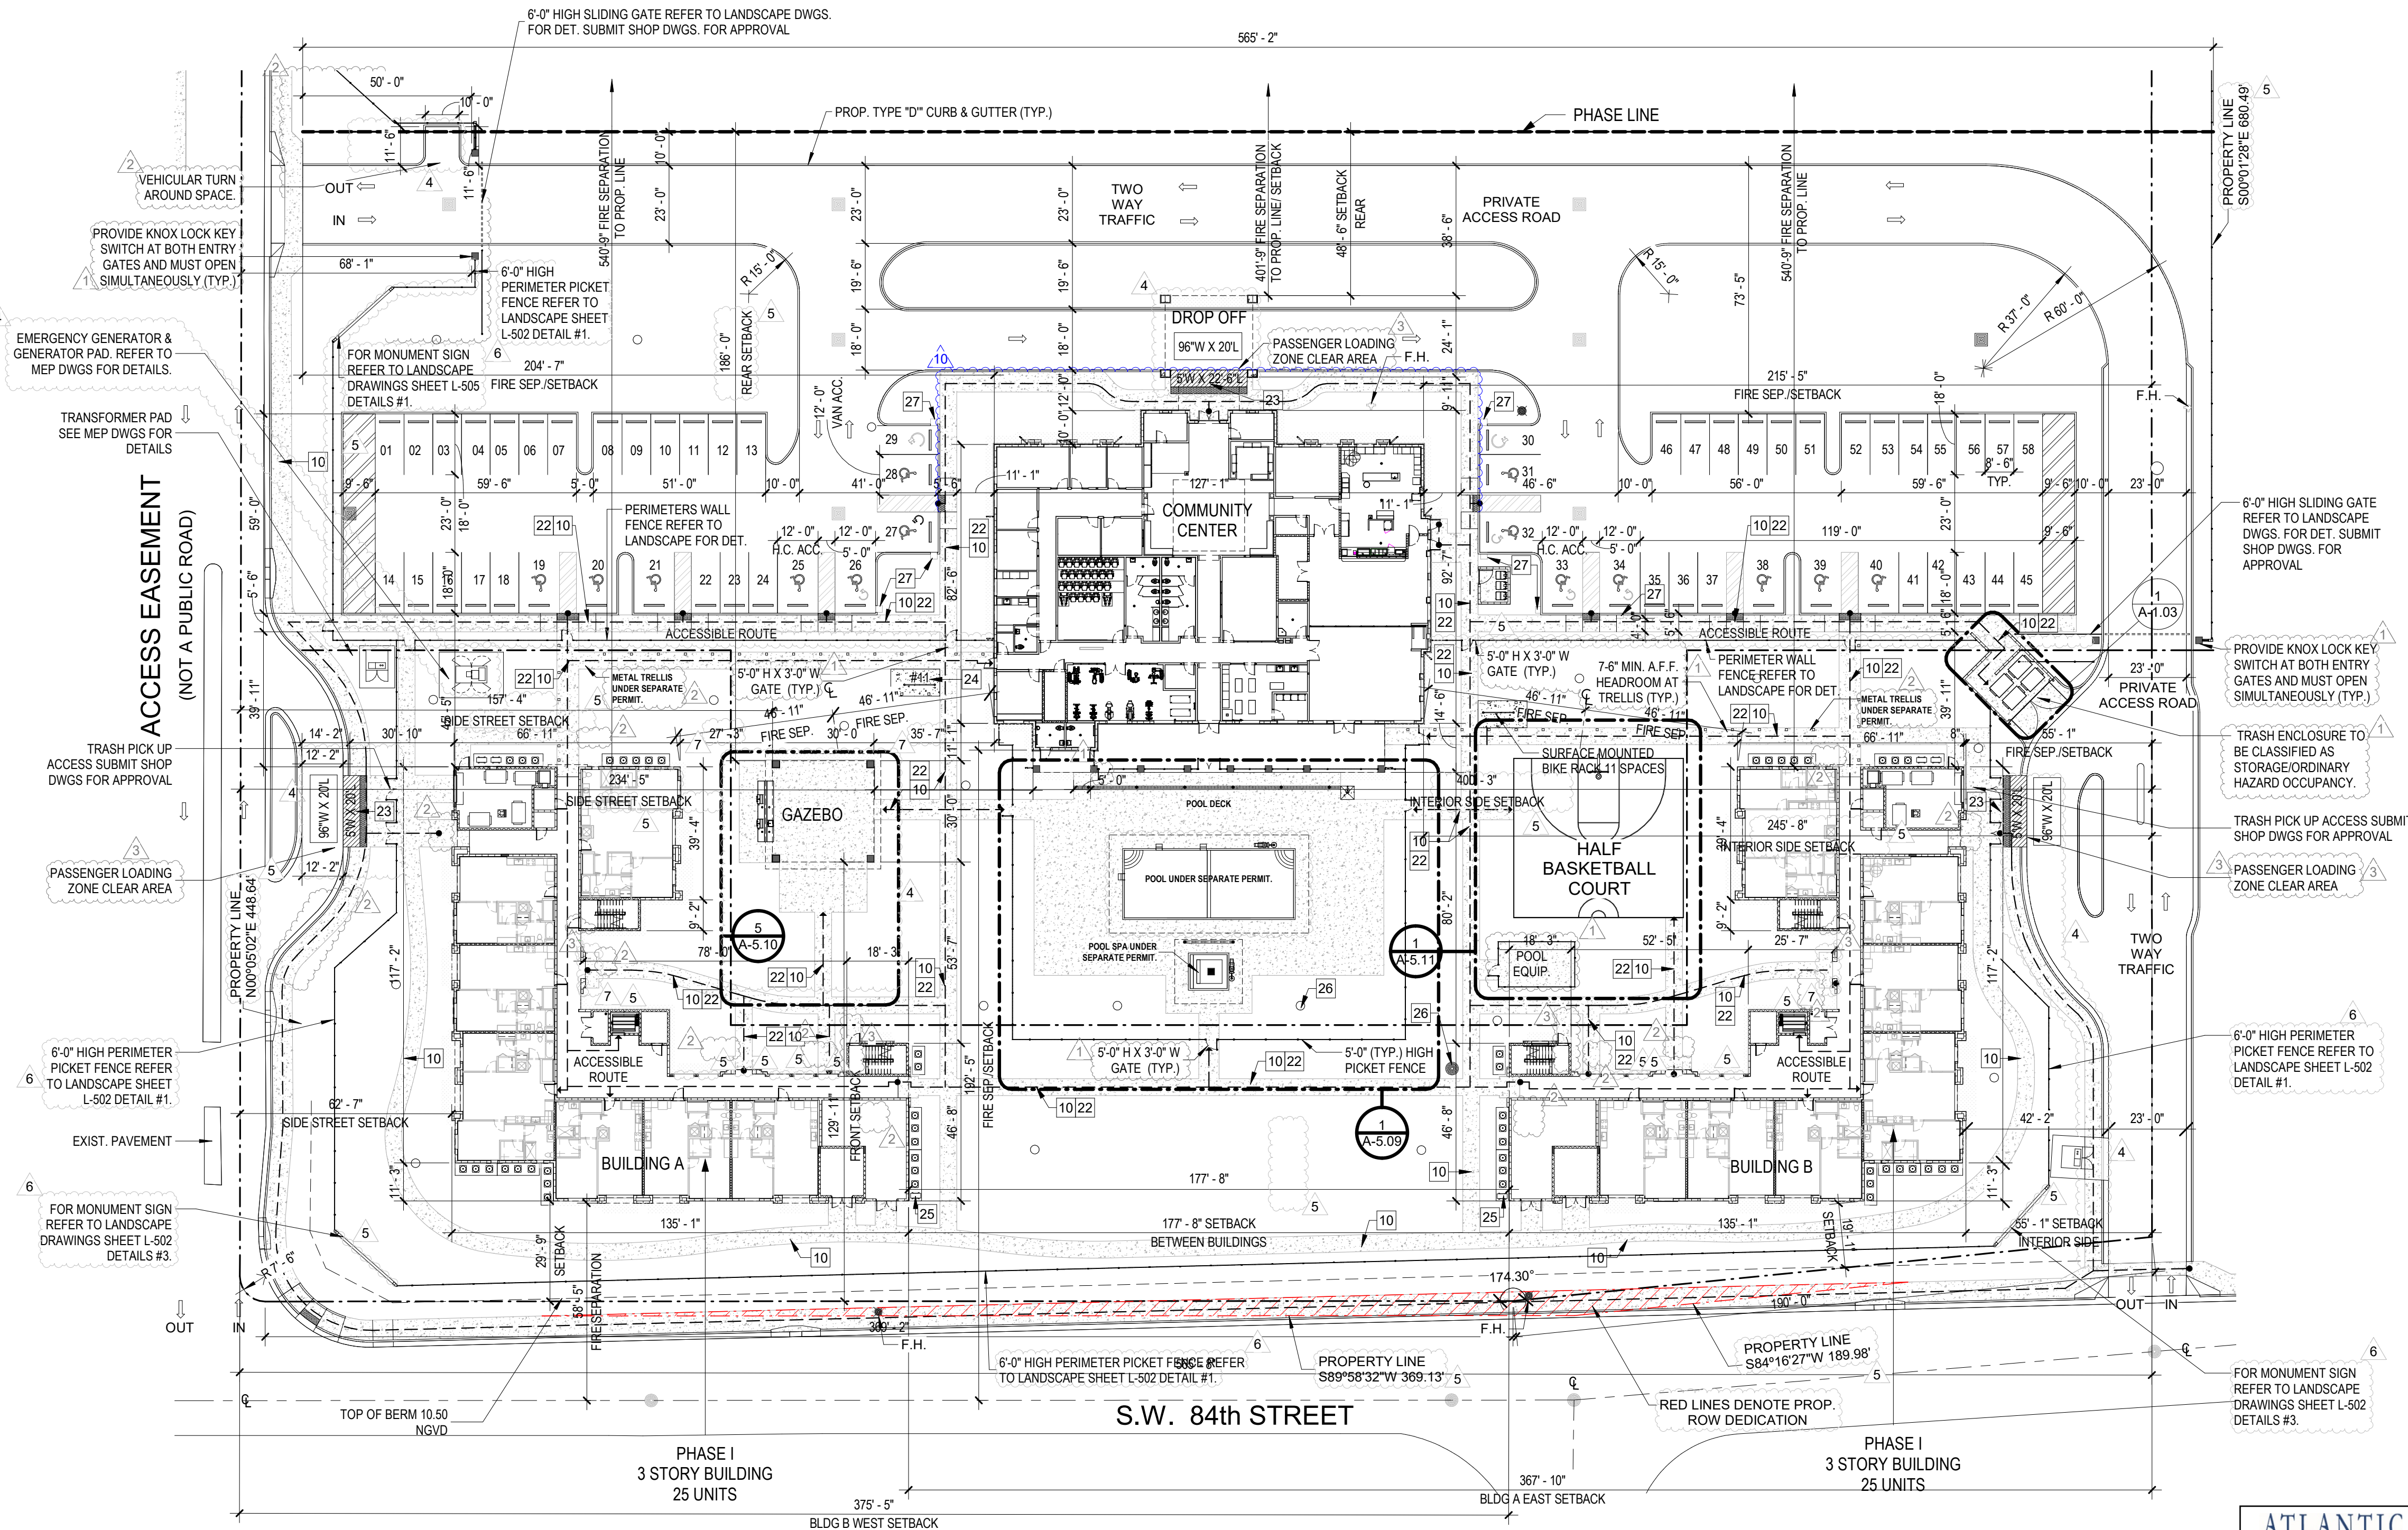

ENLARGED SITE PLAN


SCALE: 1" = 30'-0"

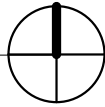

ATLANTIC
PACIFIC
COMMUNITY BUILDERS
Bulletin #6
Date Received:
November 19th, 2024

REVISIONS		
Rev #	Revision Description	Date
1	Bldg Review Cmt	09/30/20
2	County Comments	11/20/20
3	County Comments	01/08/21
4	County Comments	03/22/21
5	County Comments/ Owner VE	04/03/23
6	County Comments	08/11/23
7	Pre-con RFIs/Coord.	05/03/24
10	Coord./Bulletin #6	09/20/24

SEAL:

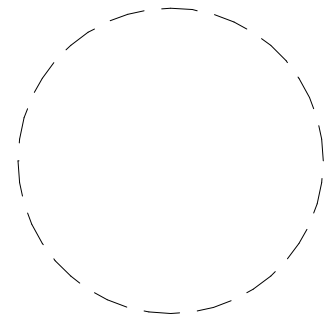

THIS DRAWING IS THE PROPERTY OF CORWIL ARCHITECTS INC.
UNLESS OTHERWISE PROVIDED FOR BY CONTRACT, THE
CONTENTS OF THIS DRAWING ARE CONFIDENTIAL AND
SHALL NOT BE TRANSMITTED TO ANY OTHER PARTY
EXCEPT AS AGREED TO BY THE ARCHITECT/ENGINEERS.

DATE: 5-18-2020
JOB No.: 2019-20
DRAWN BY: MAMA, CM, JM, JW, FG
APPR BY: AMC
PRINTED: 11/13/2024

A-1.01

GENERAL SITE NOTES

- LOT SHALL BE GRADED TO PREVENT DIRECT OVERLAND DISCHARGE OF STORM WATER ONTO ADJACENT PROPERTY. REFER TO CIVIL DRAWINGS.
- WATERPROOFING SHALL BE PROVIDED THROUGHOUT TO ENSURE A WATERTIGHT STRUCTURE. 15 MIL. MIN. WATER PROOFING SHALL BE PROVIDED UNDER ALL SLABS ON GRADE AND WALLS AGAINST EARTH/FILL. CONTRACTOR SHALL CONSULT WATER PROOFING AS NEEDED AND AS REQUIRED BY ALL CODES AND PROJECT SPECIFICATIONS.
- R DENOTES RADIUS TO BE PROVIDED. REFER TO CIVIL DRAWINGS FOR DETAILS.
- CONTRACTOR SHALL NOTIFY ARCHITECT/ENGINEER OF ANY AND ALL DISCREPANCIES PRIOR TO COMMENCING ANY WORK.
- CONTRACTOR SHALL REFER TO LANDSCAPE, CIVIL, AND IRRIGATION DRAWINGS FOR COMPLETE SITE REQUIREMENTS AND SHALL CONSULT ARCHITECT/OWNER FOR FINAL COORDINATION.
- CONTRACTOR SHALL COORDINATE ALL SITE WORK WITH SUBCONTRACTORS PRIOR TO COMMENCING ANY WORK UNDER THIS PERMIT.
- CONTRACTOR SHALL PROVIDE DETECTABLE WARNING MATERIALS WHERE SHOWN. PROVIDE SHOP DRAWINGS FOR APPROVAL.
- CONTRACTOR SHALL COORDINATE OFF ALL WORK AREAS FROM PUBLIC ACCESS AND INSURE A SAFE AND CLEAN WORK ZONE. IT SHALL BE THE RESPONSIBILITY OF THE CONTRACTOR TO SECURE WORK AREAS.
- ACTUAL LOCATION FOR DETECTABLE WARNING SHALL BE COORDINATED IN FIELD AND AS PER PREVAILING CODES AND STANDARDS.
- ALL PEDESTRIAN ROUTES SHALL HAVE A MAX. SLOPE OF 1:20 AND A MAX. CROSS SLOPE OF 1:50. PAVED/CONCRETE AREAS SHALL BE LEVELED AND SLOPED AWAY FROM STRUCTURES. THERE SHALL BE NO PONDING AREAS. REFER TO CIVIL DRAWINGS.
- BACKFLOW PREVENTER SHALL BE HIDDEN FROM VIEW BY THE USE OF LANDSCAPE. COORDINATE WITH ARCHITECT.
- CONTRACTOR AND SUBCONTRACTOR SHALL ENSURE PROPER INSTALLATION OF ALL STRUCTURES AND FIXTURES. ALL REQUIRED ACCESSORIES NOT SHOWN BUT REQUIRED BY CODES OR STANDARDS SHALL BE PROVIDED BY CONTRACTOR AND SUBCONTRACTOR AT NO ADDITIONAL COST TO THE OWNER/ARCHITECT.
- MANUFACTURER'S RECOMMENDATIONS AND/OR MIAMI DADE COUNTY PRODUCT APPROVALS FOR HIGH WIND VELOCITY HURRICANE ZONES SHALL BE STRICTLY ADHERED TO FOR ALL INSTALLATIONS AND MATERIALS.
- ALL EXISTING CURB CUTS IN RIGHT OF WAY WILL BE CLOSED OFF DURING CONSTRUCTION PROCESS AND REPLACED WITH NEW CURBS AND GUTTERS, IF NECESSARY AS PER ENGINEERING DEPARTMENT AND ITS SPECIFICATIONS.
- ALL NEW SIDEWALKS, CURBS AND GUTTER WILL BE DESIGNED TO BE CONTINUOUS AND TO MAINTAIN THE CONTINUITY WITH THE EXISTING SIDEWALKS, CURBS AND GUTTERS.
- ANY DAMAGE TO EXISTING SIDEWALK DURING CONSTRUCTION PROCESS SHALL BE REMOVED AND RECONSTRUCTED IN ACCORDANCE WITH THE PUBLIC WORKS DEPARTMENT AND ITS SPECIFICATIONS. THIS ALSO APPLIES TO ANY MISSING SIDEWALK WITH THE PROPERTY BOUNDARY.
- 1/2" MAX. THRESHOLD AT ALL EGREGES DOORS (TYP).
- COORDINATE ALL WORK WITH ALL OTHER TRADES.
- ALL GRADE SHALL SLOPE AWAY FROM BUILDING WALLS.
- SEE LANDSCAPE DRAWINGS FOR OPEN SPACES.
- SIGNAGE UNDER SEPARATE PERMIT.
- ACCESSIBLE ROUTE SHALL COMPLY WITH ELEVATION CHANGES 303 FBCA.
- VEHICLE PULL-UP SPACES AND ACCESS AISLES SERVING THEM SHALL COMPLY WITH 302. ACCESS AISLES SHALL BE AT THE SAME LEVEL AS THE VEHICLE PULL-UP SPACE THEY SERVE. CHANGES IN LEVEL ARE NOT PERMITTED. EXCEPTION: SLOPES NOT STEEPER THAN 1:48 SHALL BE PERMITTED.
- SURFACE MOUNTED BIKE RACKS.
- CONDENSING UNITS. REFER TO MECHANICAL DRAWINGS. FOR MORE INFO.
- SEWER MAINS AND MANHOLES. REFER TO CIVIL DRAWINGS FOR MORE INFO.
- WIRING PROVIDED FOR FUTURE ELECTRICAL VEHICLE PARKING (EV). (7) PROVIDED 2'-0"x2'-0" CONCRETE PAD FOR FUTURE INFRASTRUCTURE.

SITE PATTERN LEGEND

- DIAGONAL HATCH DENOTES 20' L X 5' W PASSENGER LOADING ZONE AREA
- LANDSCAPE/OPEN AREA (REFER TO LANDSCAPE DWGS.)
- ASPHALT/PAVEMENT
- ADA PARKING AISLE
- DETECTABLE WARNING PAVERS
- ELECTRIC VEHICLE
- PEDESTRIAN SIDEWALKS TO MEET ACCESSIBLE ROUTE REQUIREMENTS OF MAX. SLOPE OF 1:20 AND A MAX. CROSS SLOPE OF 1:50.