




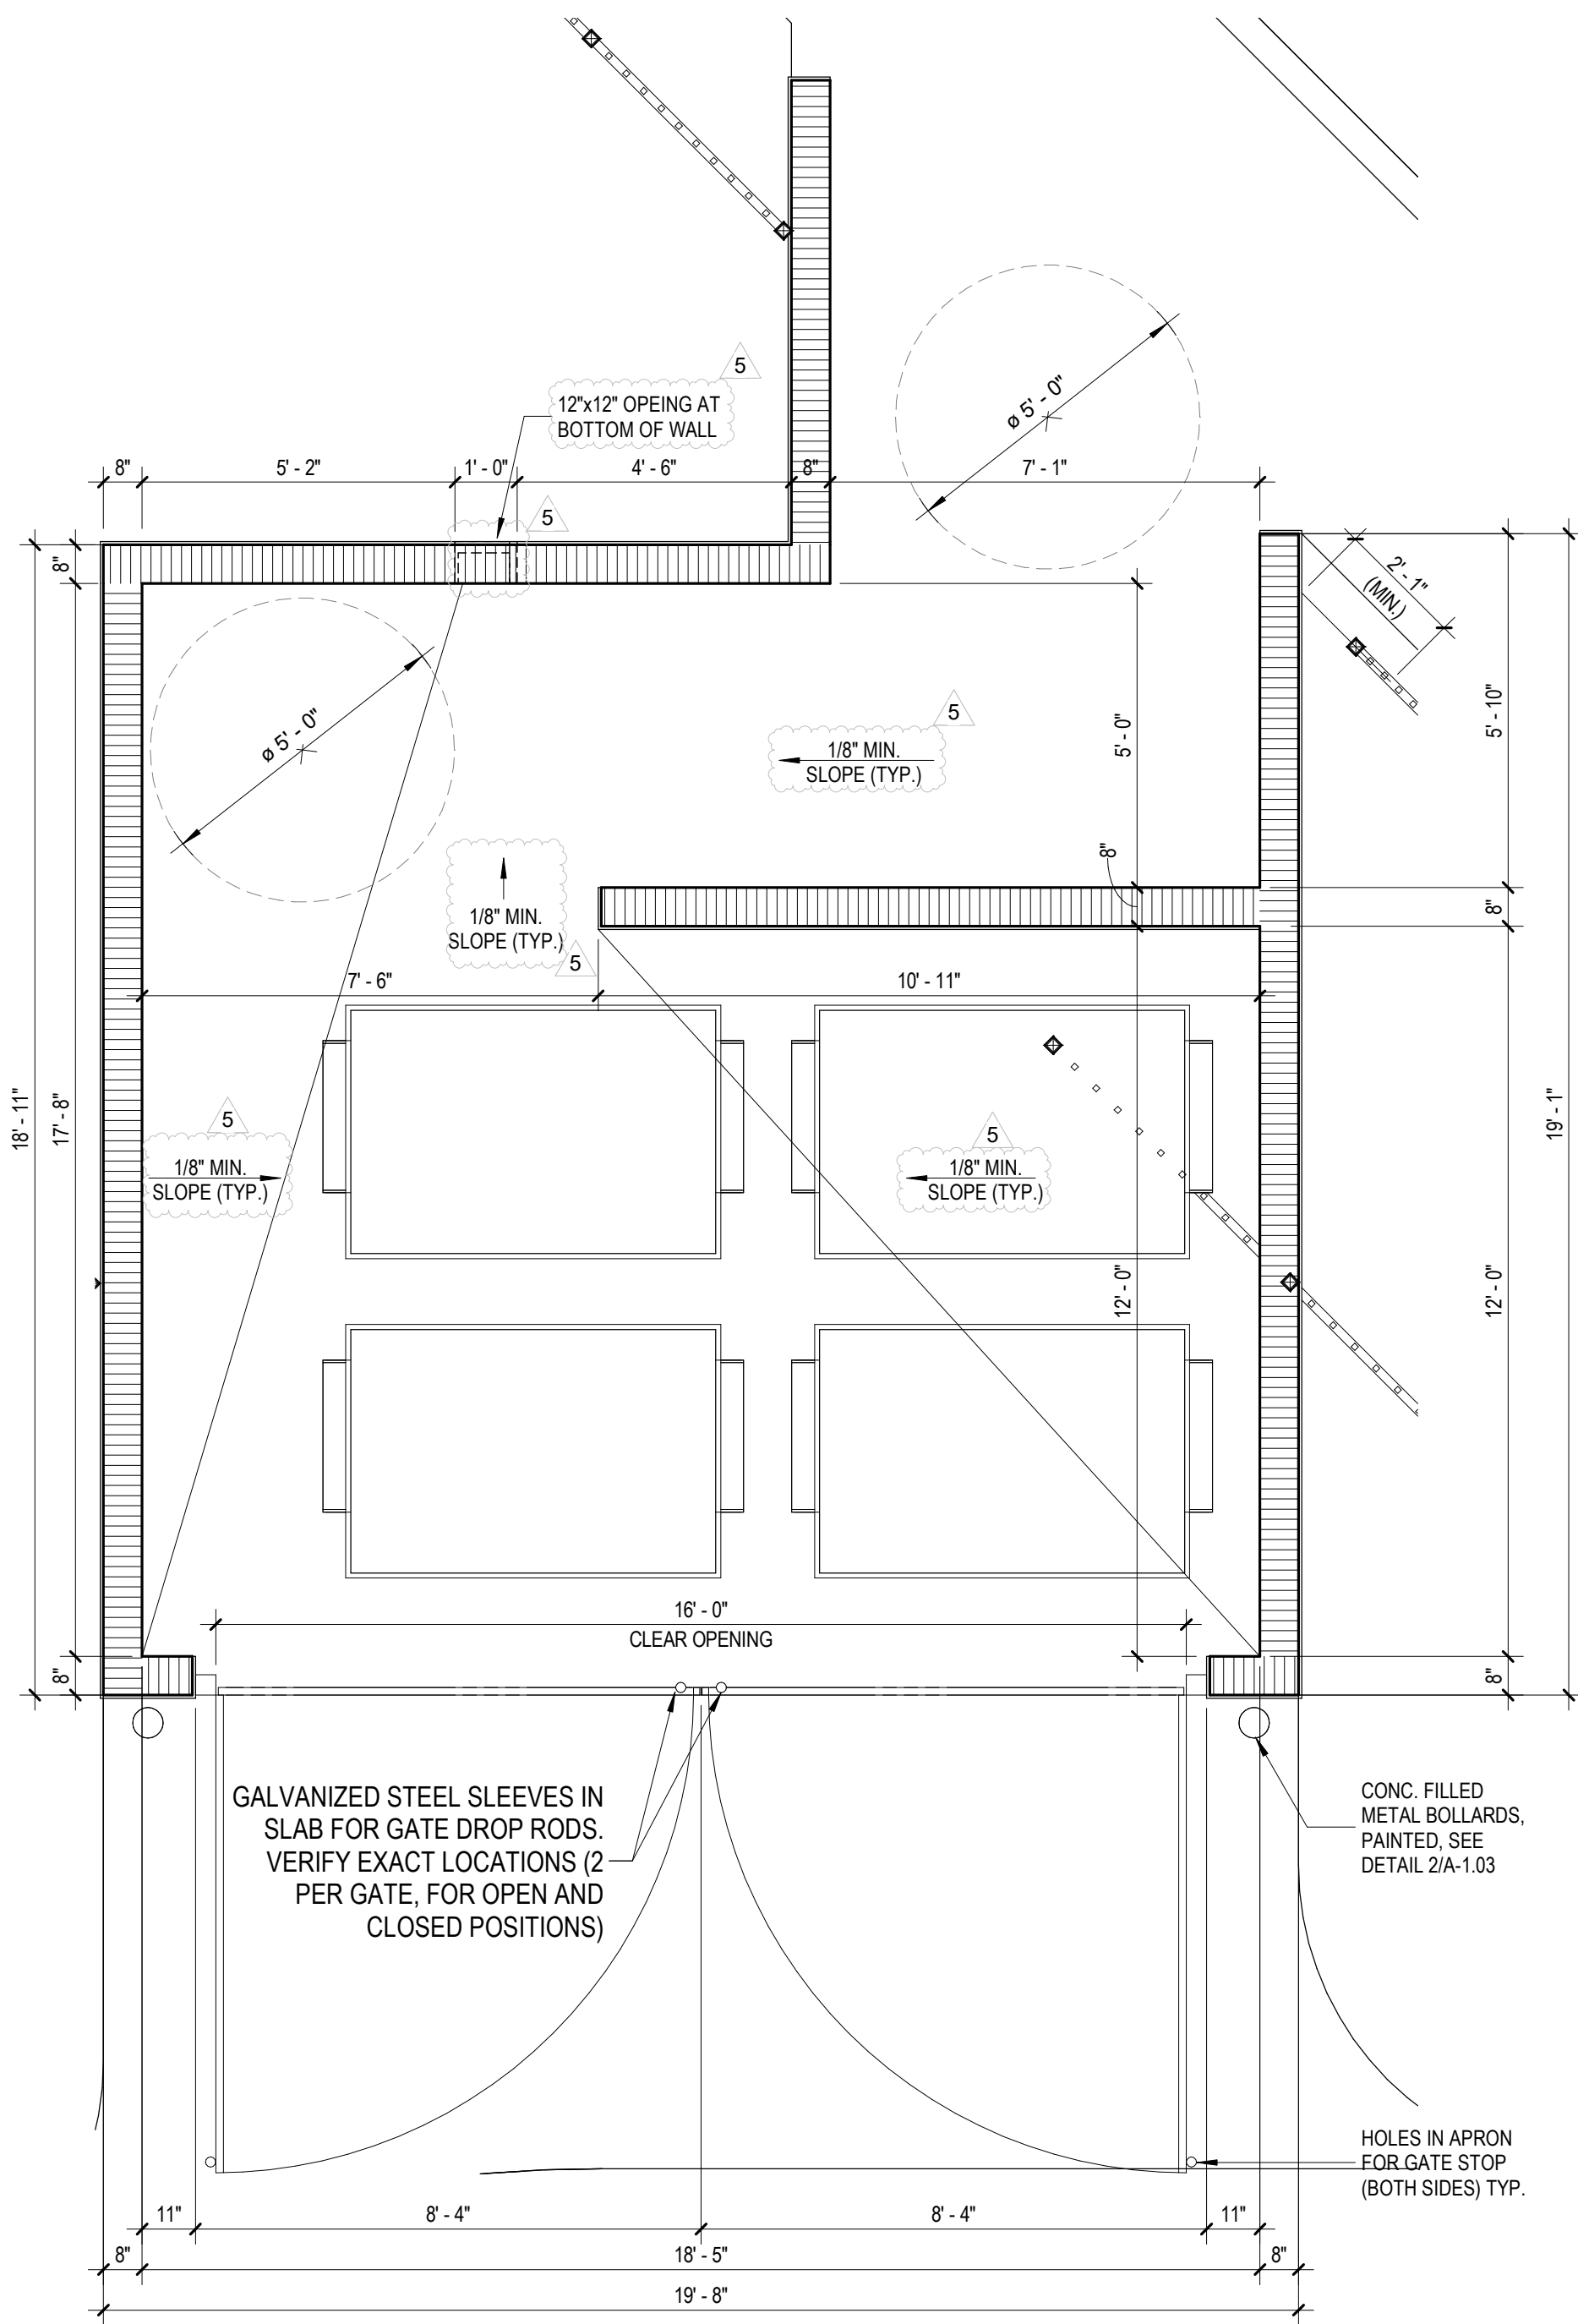


1 COMMUNITY CENTER TRASH ENCLOSURE
SCALE: 3/8" = 1'-0"

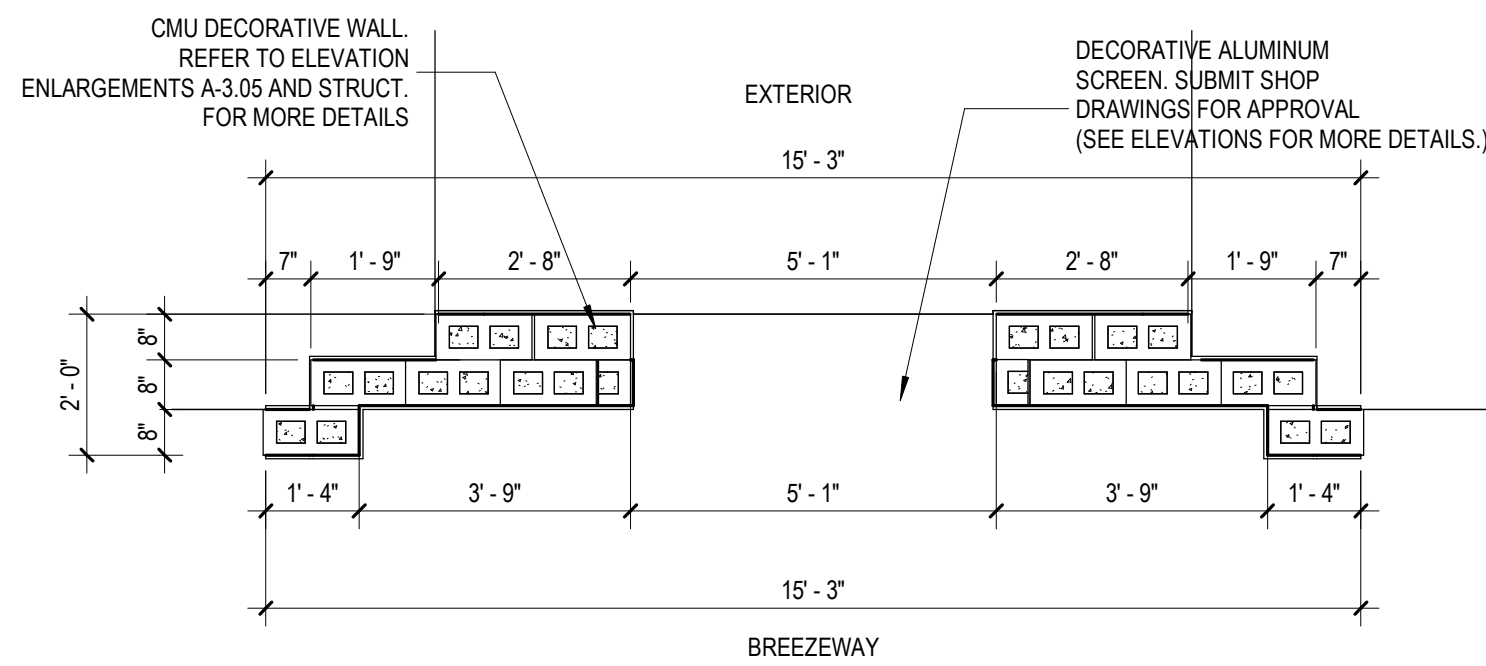



2 TYP. WALL FEATURE
SCALE: 3/8" = 1'-0" RESIDENTIAL BUILDING

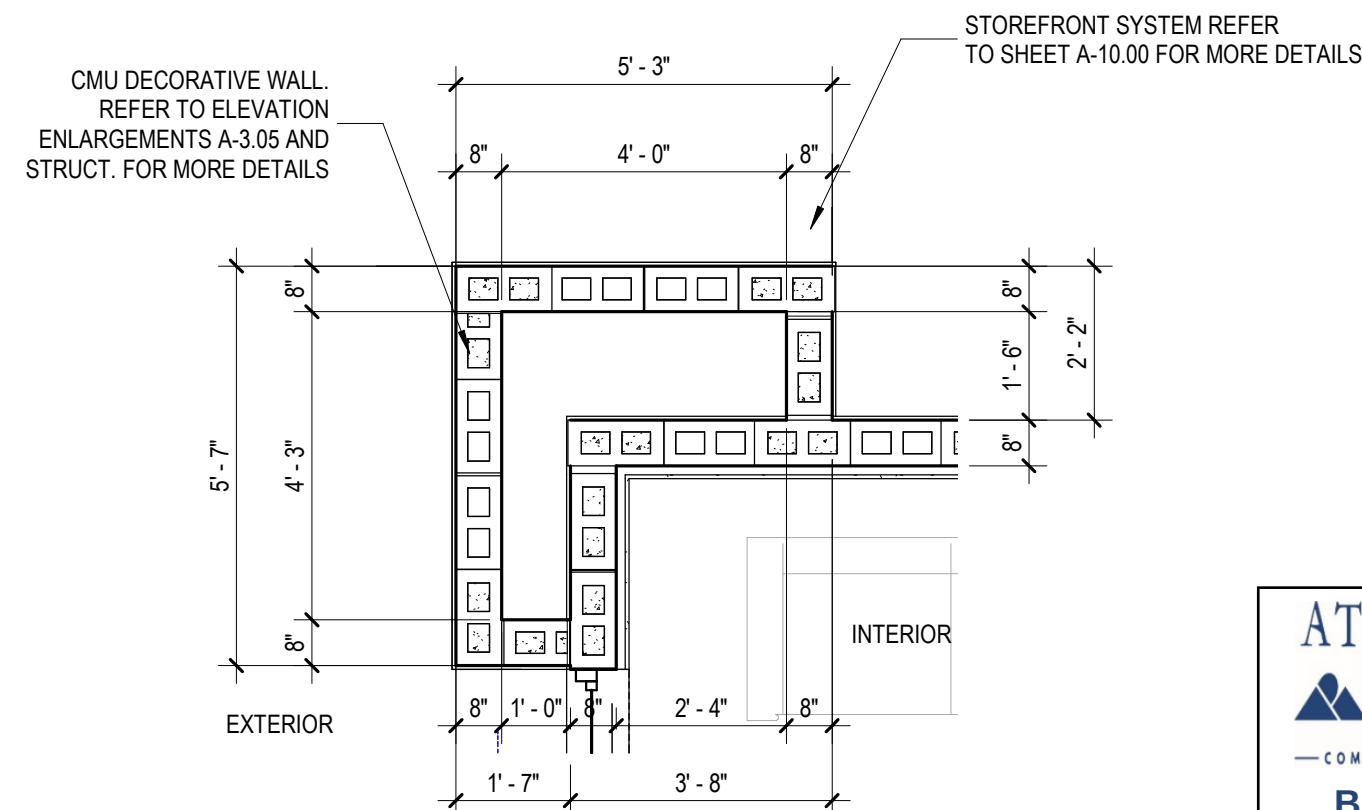


4 TYP. WALL FEATURE
SCALE: 3/8" = 1'-0" RESIDENTIAL BUILDING

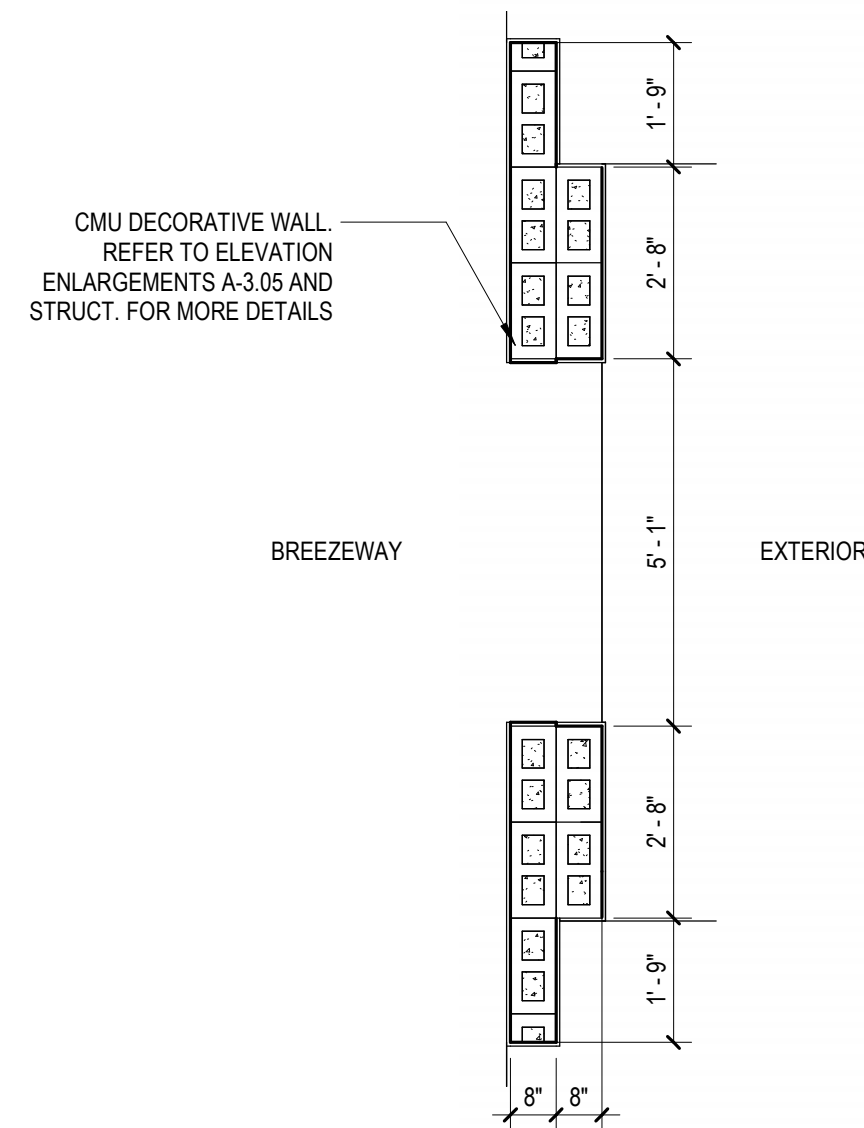


3 TYP. WALL FEATURE
SCALE: 3/8" = 1'-0" RESIDENTIAL BUILDING

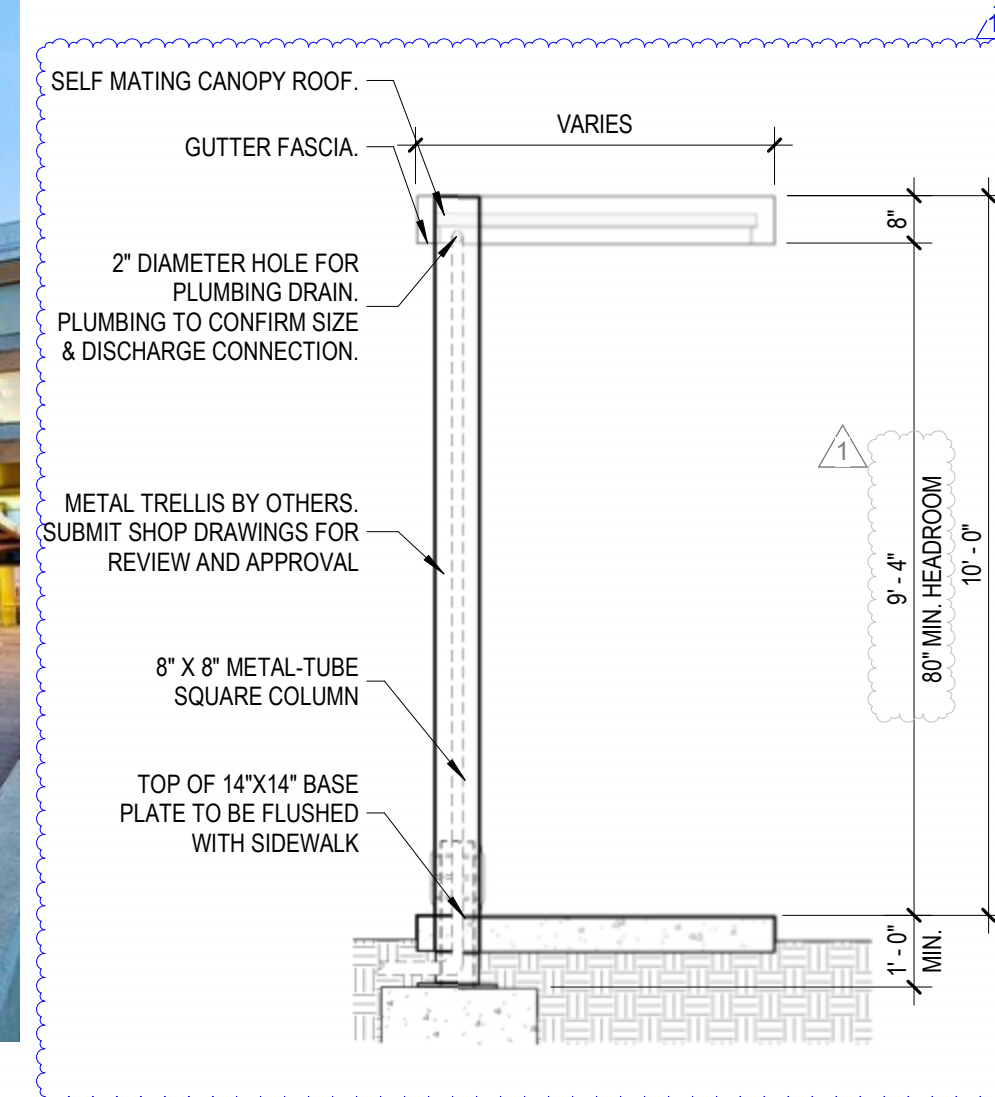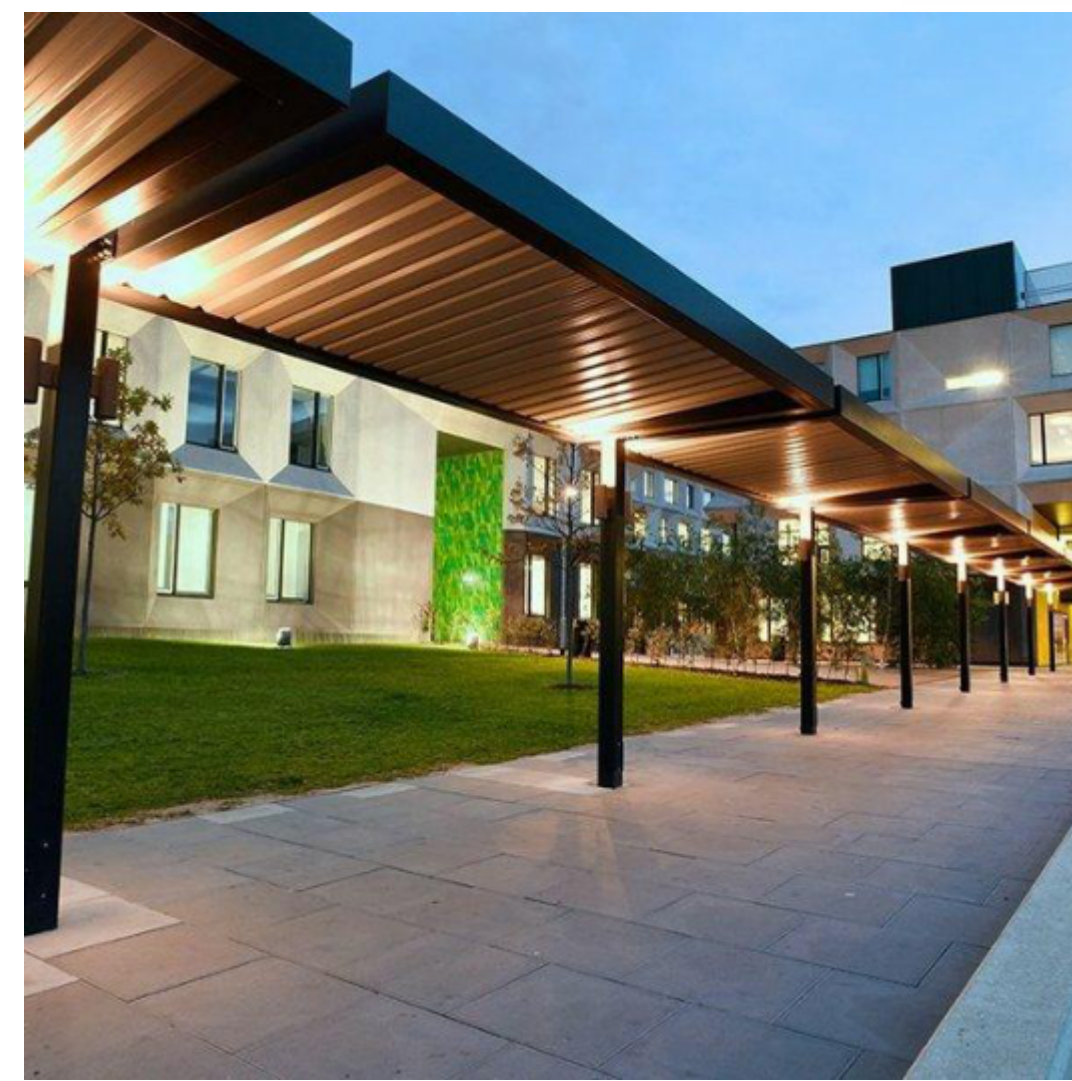

7 TRELLIS DETAIL SECTION
SCALE: 3/8" = 1'-0"

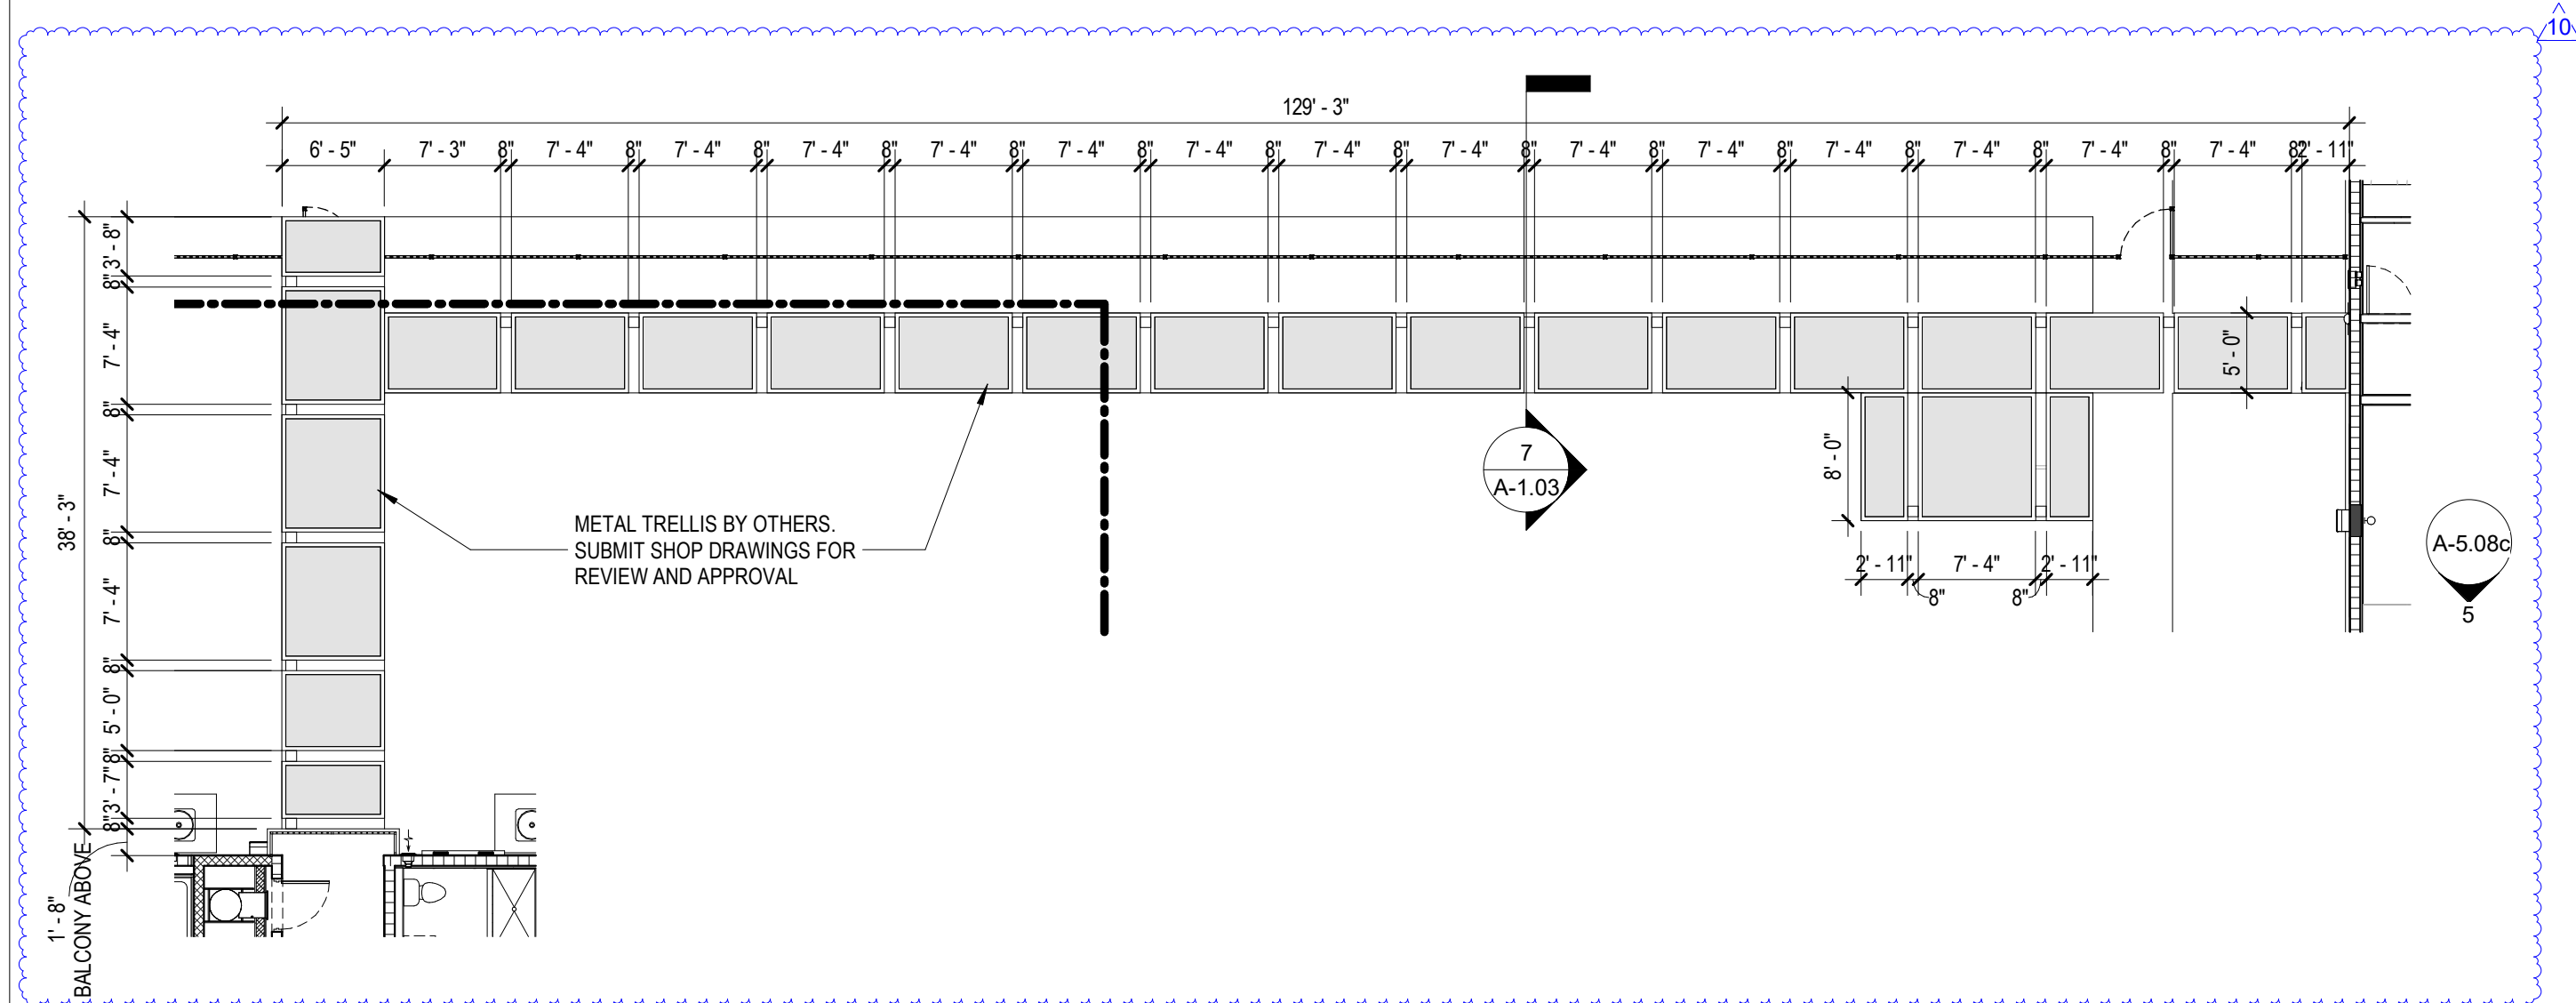

5 ENLARGED TRELLIS DETAIL
SCALE: 3/32" = 1'-0"

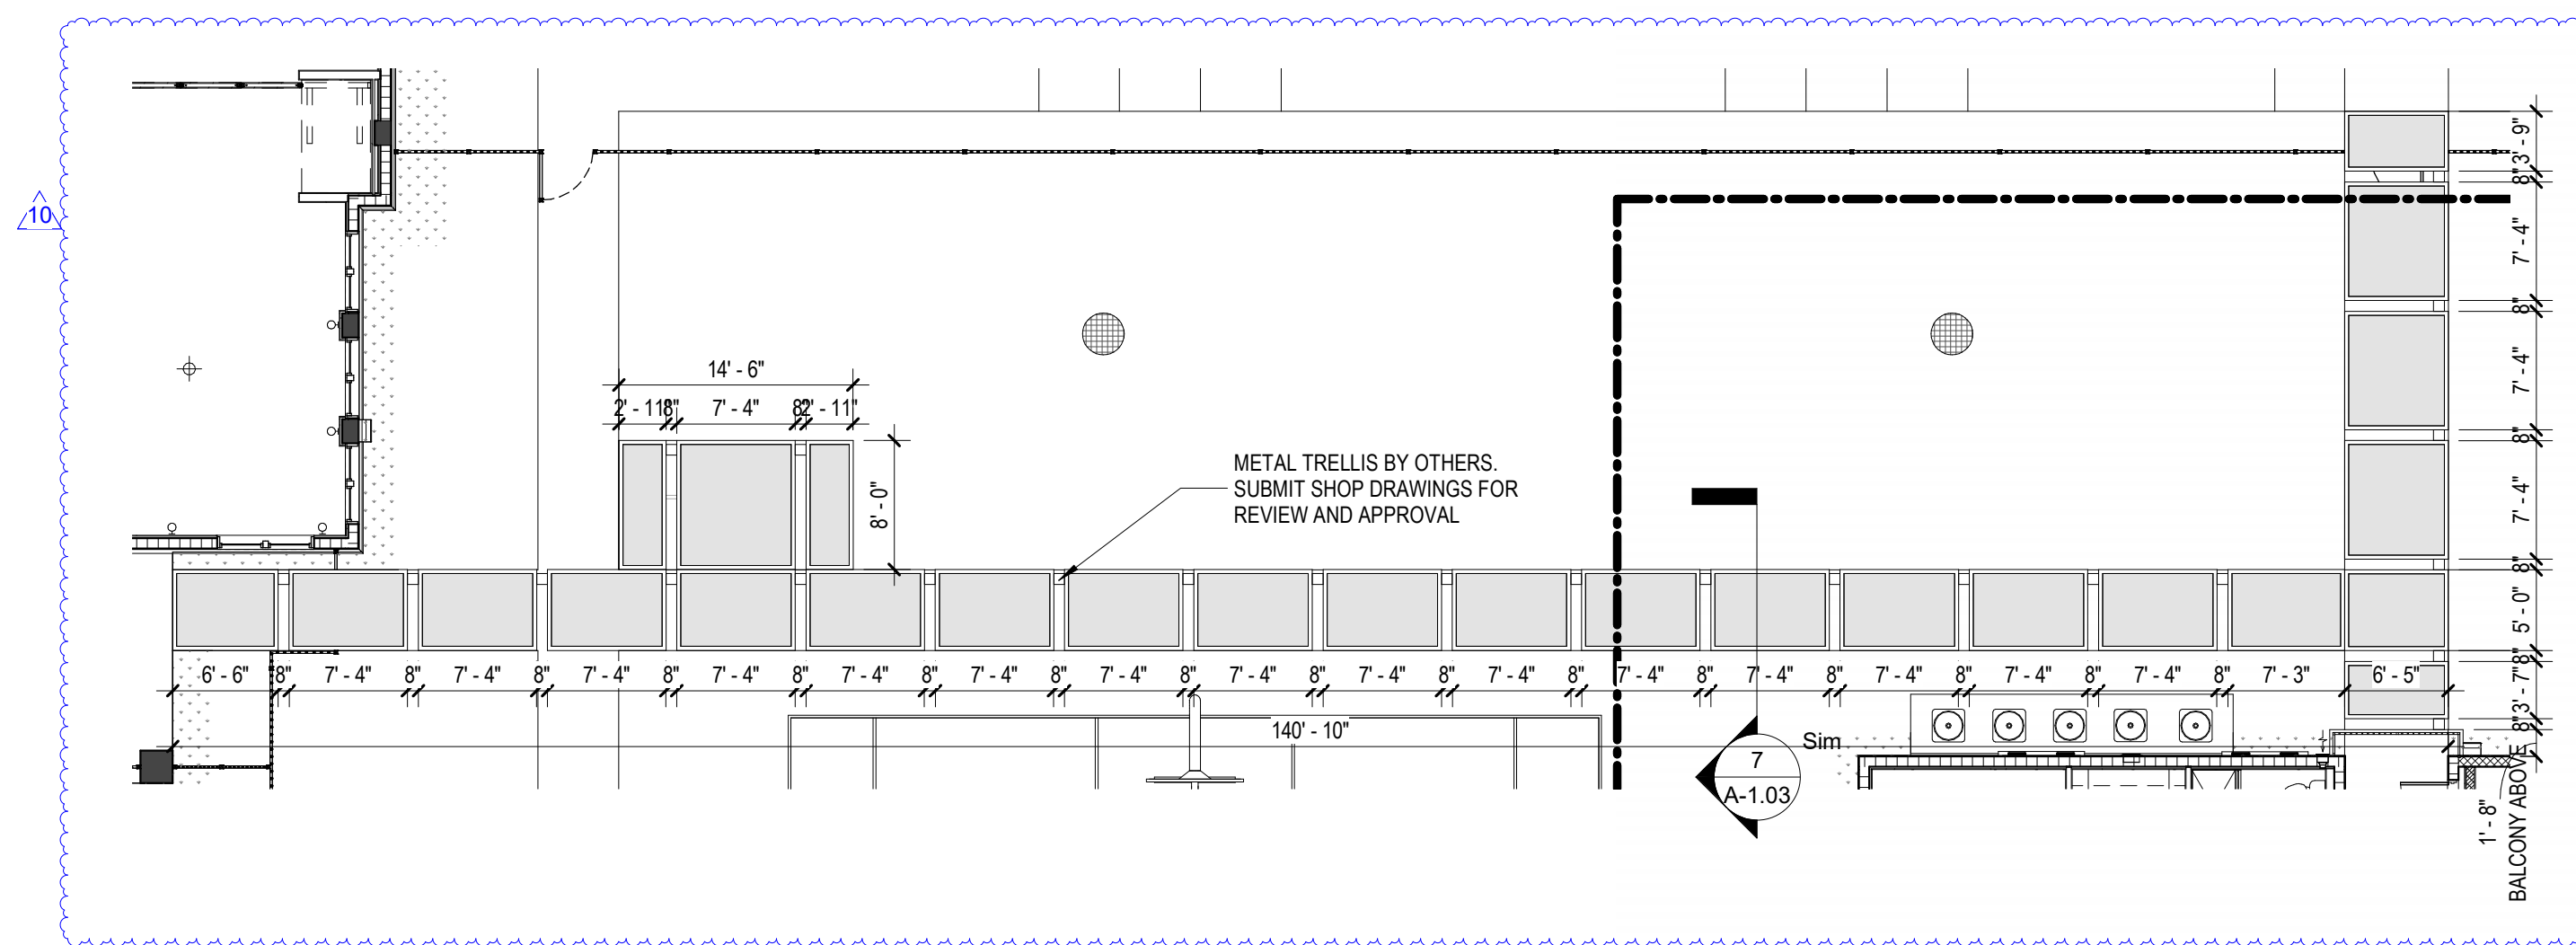

6 ENLARGED TRELLIS DETAIL
SCALE: 3/32" = 1'-0"



CORWILARCHITECTS
4210 LAGUNA ST. CORAL GABLES FL 33146
LIC. NO. AA-C002151 T.305.448.7383

PROJECT:



Casa Familia
Exceptional Housing for Exceptional People
10951 SW 84th ST,
MIAMI-DADE, FLORIDA 33173

OWNER:



161 NW 6th ST, Ste. 1020
Miami, Florida 33136

PHASE:


PERMIT SET

SITE DETAILS

REVISIONS

Rev #	Revision Description	Date
1	Bldg Review Cmt	09/30/20
5	County Comments/ Owner VE	04/03/23
7	Pre-con RFIs/Coord.	05/03/24
10	Coord./Bulletin #6	09/20/24

SEAL:

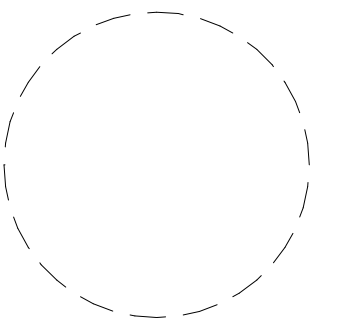

THIS DRAWING IS THE PROPERTY OF CORWIL ARCHITECTS INC.
UNLESS OTHERWISE PROVIDED FOR BY CONTRACT, THE
CONTENTS OF THIS DRAWING ARE CONFIDENTIAL AND
SHALL NOT BE TRANSMITTED TO ANY OTHER PARTY
EXCEPT AS AGREED TO BY THE ARCHITECT/ENGINEERS.

DATE: 5-18-2020
JOB No.: 2019-20
DRAWN BY: MA, CM, JM, JW, FG
APPR BY: AMC
PRINTED: 11/13/2024

A-1.03