



CORWIL ARCHITECTS
4210 LAGUNA ST. CORAL GABLES FL 33146
LIC. NO. AA-C002151 T.305.448.7383

PROJECT:



10951 SW 84th ST,
MIAMI-DADE, FLORIDA 33173

OWNER:



161 NW 6th ST, Ste. 1020
Miami, Florida 33136


PHASE:

PERMIT SET

TYPICAL WALL SECTIONS

REVISIONS		
Rev #	Revision Description	Date
5	County Comments/ Owner VE	04/03/23
7	Pre-con RFIs/Coord.	05/03/24
10	Coord./Bulletin #6	09/20/24


SEAL:

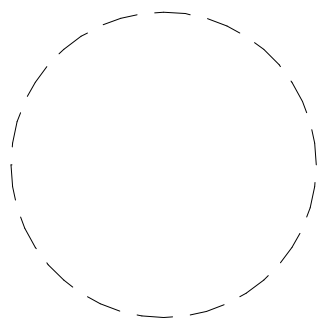

THIS DRAWINGS IS THE PROPERTY OF CORWIL ARCHITECTS INC.
UNLESS OTHERWISE PROVIDED FOR BY CONTRACT, THE
CONTENTS OF THIS DRAWINGS ARE CONFIDENTIAL AND
SHALL NOT BE TRANSMITTED TO ANY OTHER PARTY
EXCEPT AS AGREED TO BY THE ARCHITECT/ENGINEERS.

DATE: 5-18-2020
JOB No.: 2019-20
DRAWN BY: MA, CM, JM, JW, FG
APPR BY: AMC
PRINTED: 11/13/2024

A-4.04

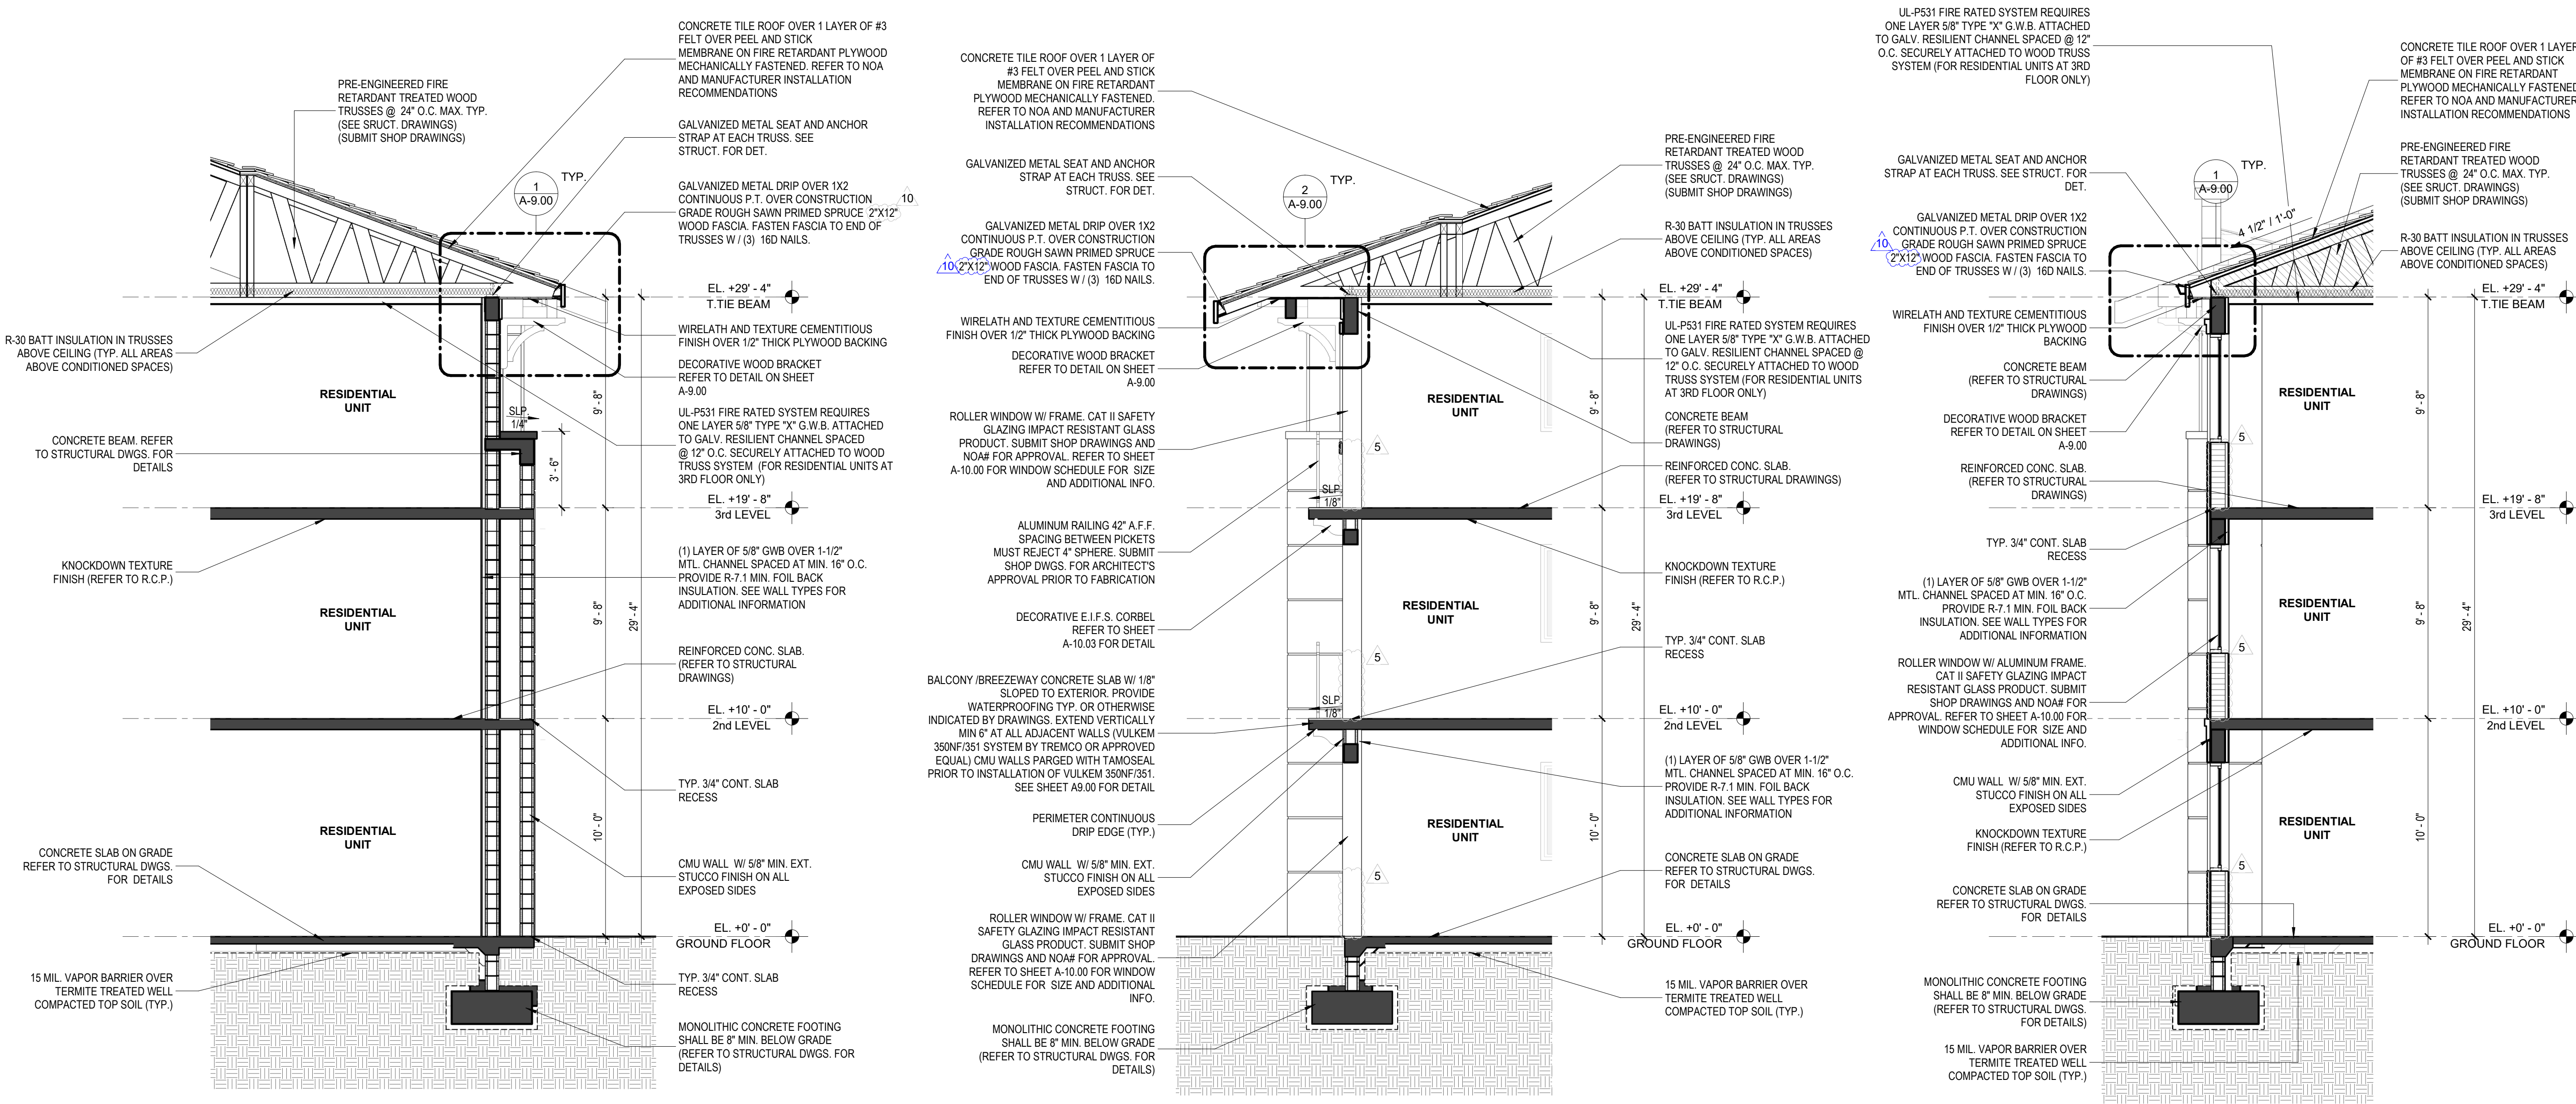

1 TYP. WALL SECTION
SCALE: 1/4" = 1'-0"

2 TYP. WALL SECTION
SCALE: 1/4" = 1'-0"

3 WALL SECTION 3
SCALE: 1/4" = 1'-0"

