

POOL EQUIPMENT NOTE LEGEND

1.

CHLORINE CONTAINER WITH LOCKABLE LID.
2.

ACID CONTAINER WITH LOCKABLE LID.
3.


SPA COLLECTOR TANK.
4.

POOL HEATERS.
5.


SPA HEATER.
6.

AQUAWORX POOL EQUIPMENT SET. REFER TO POOL DRAWINGS FOR DETAILS.
7.


AQUAWORX SPA POOL EQUIPMENT SET. REFER TO POOL DRAWINGS FOR DETAILS.

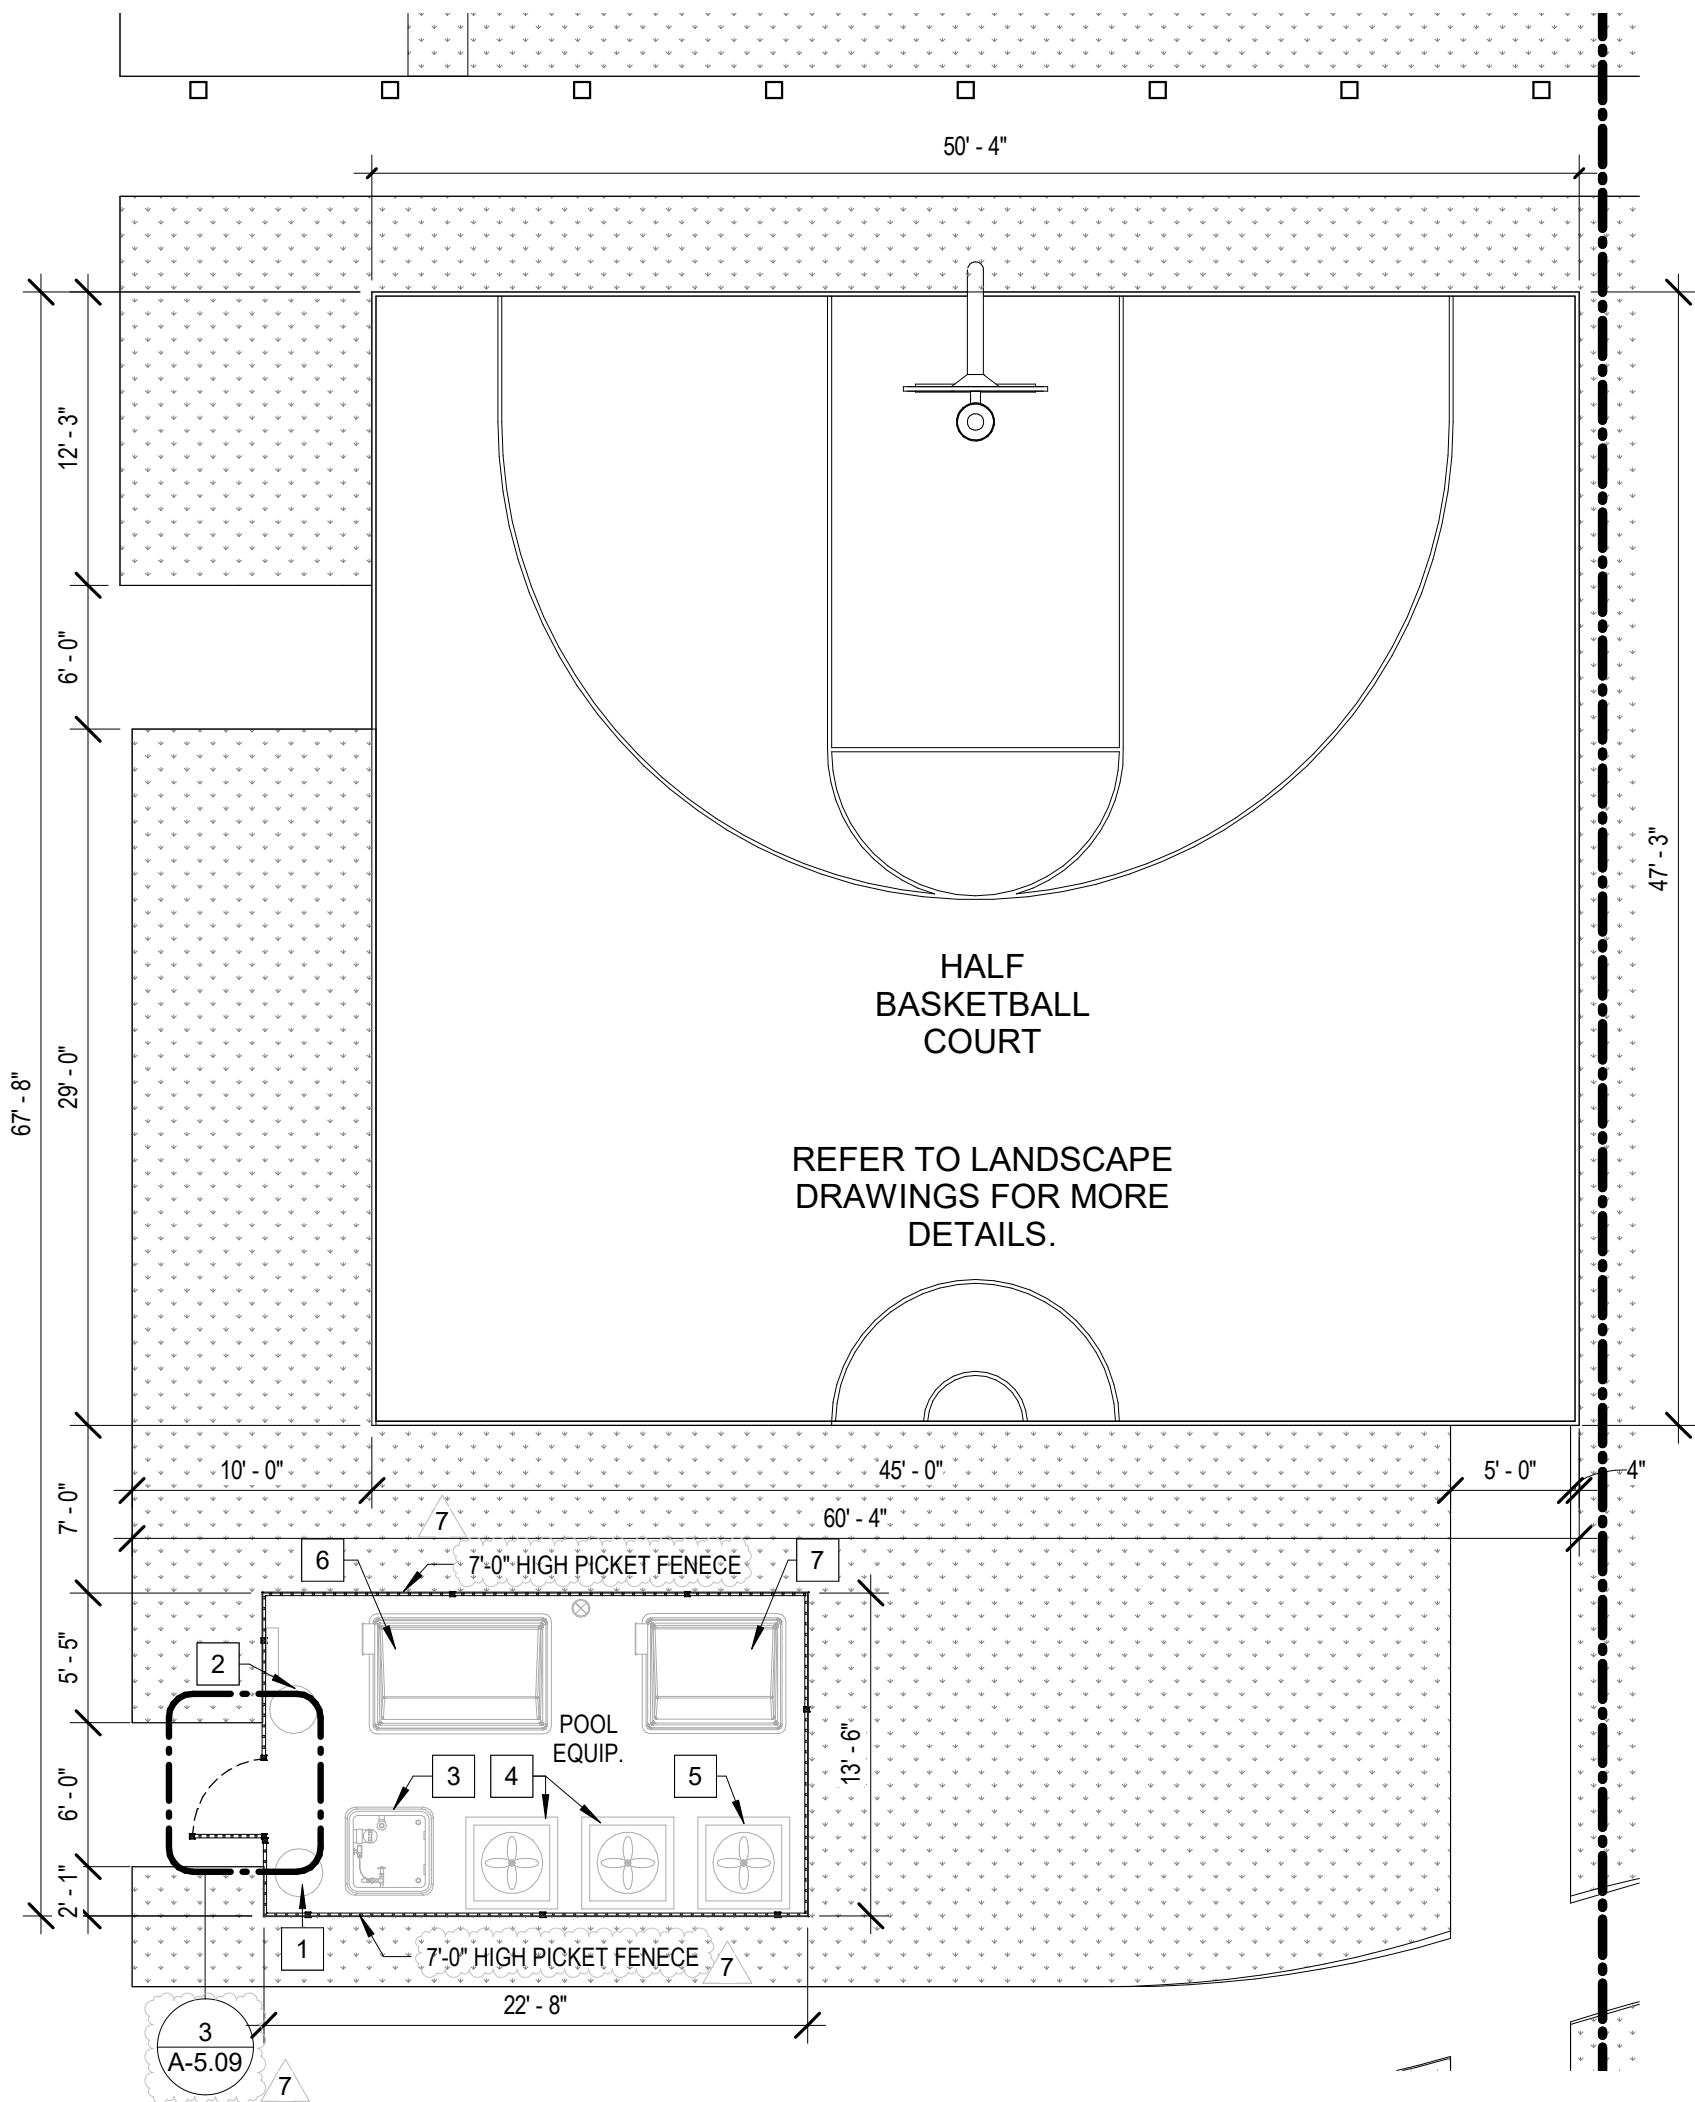

1 HALF BASKETBALL COURT- FLOOR PLAN
SCALE: 1/8" = 1'-0"

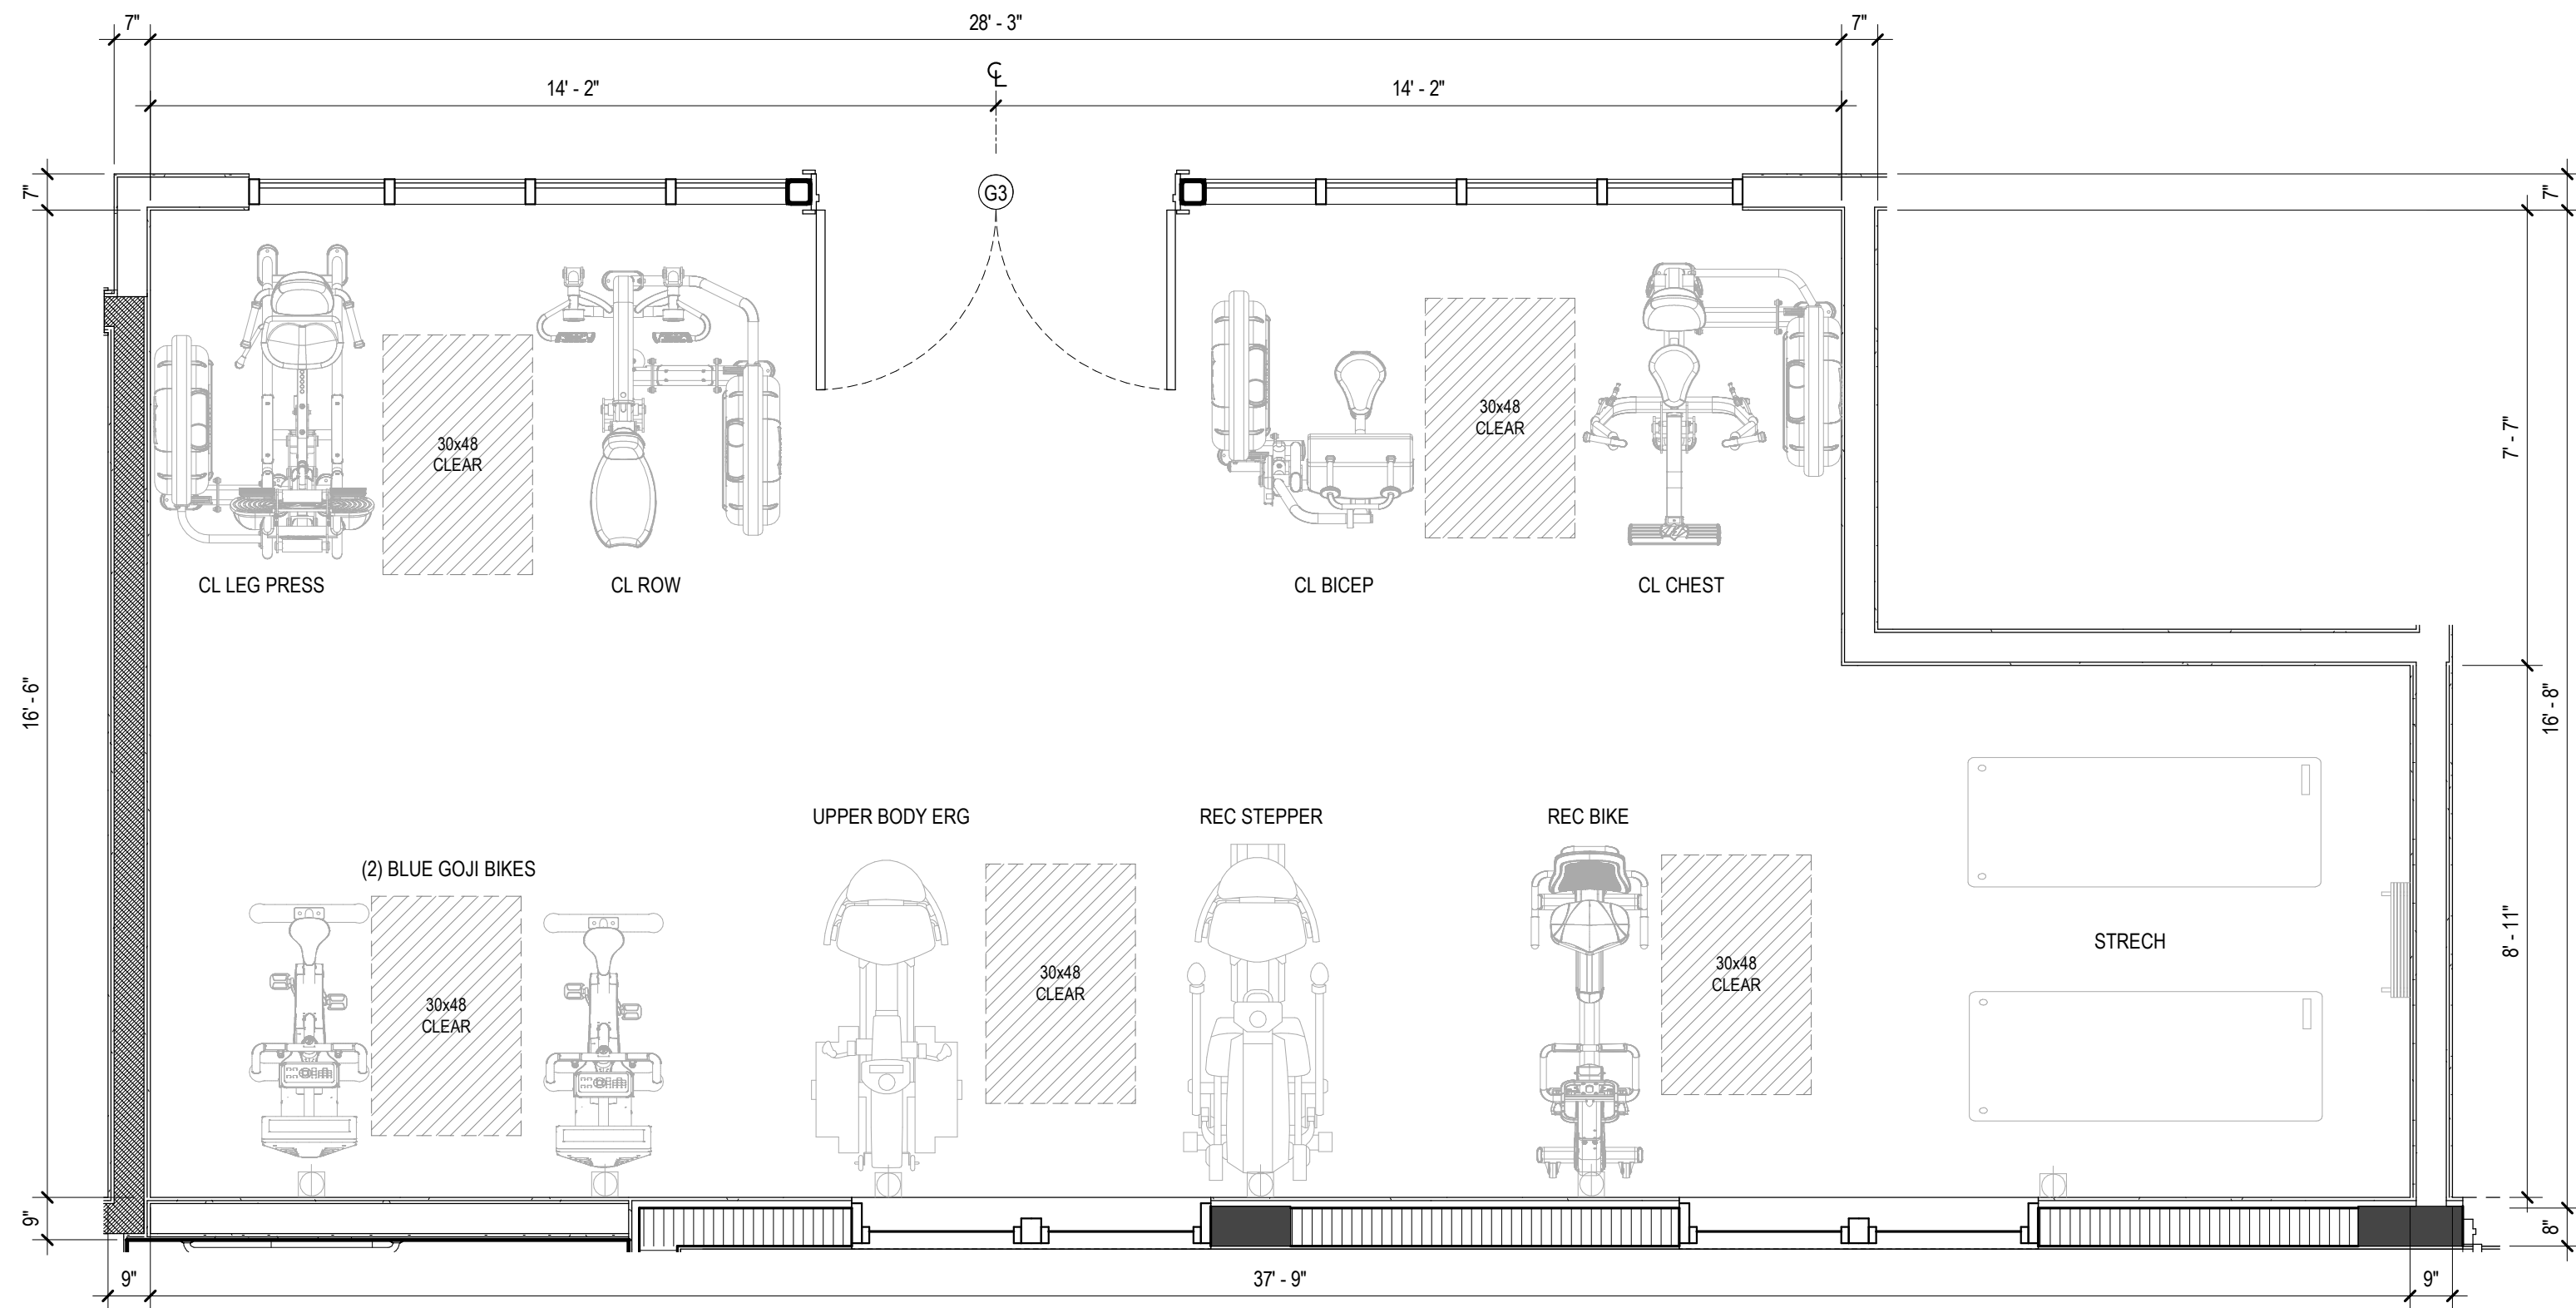

2 COMMUNITY CENTER GYM - FLOOR PLAN
SCALE: 3/8" = 1'-0"

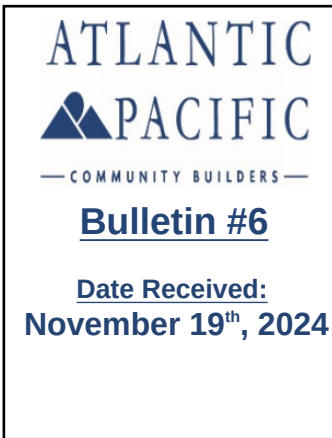

CORWILARCHITECTS
4210 LAGUNA ST. CORAL GABLES FL 33146
LIC.NO. AA-C002151 T.305.448.7383

PROJECT:



10951 SW 84th ST,
MIAMI-DADE, FLORIDA 33173

OWNER:



161 NW 6th ST, Ste. 1020
Miami, Florida 33136


PHASE:

PERMIT SET

ENLARGED BASKETBALL COURT
& GYM FLOOR PLAN

REVISIONS		
Rev #	Revision Description	Date
4	County Comments	03/22/21
7	Pre-con RFIs/Coord.	05/03/24
10	Coordin./Bulletin #6	09/20/24

SEAL:

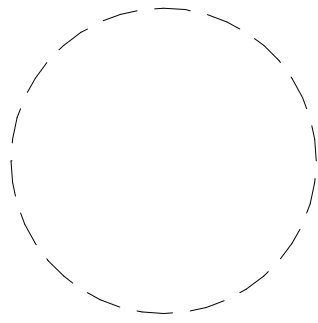

THIS DRAWINGS IS THE PROPERTY OF CORWIL ARCHITECTS INC.
UNLESS OTHERWISE PROVIDED FOR BY CONTRACT. THE
CONTENTS OF THIS DRAWINGS ARE CONFIDENTIAL AND
SHALL NOT BE TRANSMITTED TO ANY OTHER PARTY
EXCEPT AS AGREED TO BY THE ARCHITECT/ENGINEERS.

DATE: 5-18-2020
JOB No.: 2019-20
DRAWN BY: CDB
APPR BY: AMC
PRINTED: 11/13/2024