

CASA FAMILIA

KITCHEN | VANITY | LAUNDRY SHOP-DRAWINGS

CASA FAMILIA KITCHEN | VANITY SHOP-DWGS

FINISH:

- K019 SILVER LIBERTY ELM

APPLIANCES:

REGULAR UNITS:

28" REFRIGERATOR GE MODEL GTE18GSNRSS

24" DISHWASHER GE MODEL GDT535PSRSS

30" RANGE GE MODEL GRF400PV

30" MICROWAVE GE MODEL JVM3160RFSS

ADA UNITS:

28" REFRIGERATOR GE MODEL GTE18GSNRSS

24" DISHWASHER GE MODEL GDT225SSLSS (ADA)

30" RANGE GE MODEL GRS500PVSS (ADA)

30" MICROWAVE GE MODEL JES1145SHSS

30" HOOD GE MODEL J VX3300SJSS

GENERAL NOTES:

*ALL DIMENSIONS ARE FROM FINISHED WALL TO FINISHED WALL

*ALL DIMENSIONS ARE FROM FINISHED FLOOR TO FINISHED CEILING

*NOT INCLUDED: APPLIANCES, FIXTURES, PLUMBING, AND COUNTER TOPS

*IT'S ARCHITECT'S RESPONSIBILITY TO CONFIRM KITCHEN & VANITY CABINETS COMPLY WITH BUILDING FHA & ADA CODES.

REVISION LOG			
REV.	DATE	BY	DESCRIPTION
1.0	10/06/2023	V.U	
2.0	07/18/2024	A.C	
3.0	09/18/2024	A.C	
4.0	10/30/2024	A.C	
5.0	11/05/2024	A.C	

COVER

SHEET NUMBER

DATE:

REV:

DIMENSION

DRAWN BY:

PROJECT #:

CASA FAMILIA

KITCHEN | VANITIES

ITALIAN KITCHEN AND BATH

kitchen | bath | tile | closet

1777 NW 72TH AVE. MIAMI FL, 33126

T. 305.599.9000 F. 305.599.9870

CASA FAMILIA

MATRIX

CASA FAMILIA

MATRIX


UNIT NAME	QTY TOTAL	VANITY TYPE				KITCHEN TYPE	KITCHEN TYPE QTY	
		V1	V2	V3	V4			
BUILDING TYPE A								
UNIT A1	14	1				K1	K1	32
UNIT A2 FA	3		1			K2	K2	6
UNIT A3	2			1		K1	K3	6
UNIT B1	3	1			1	K3	K4	6
UNIT B2 FA	3		1		1	K4		
BUILDING TYPE B								
UNIT A1	14	1				K1		
UNIT A2 FA	3		1			K2		
UNIT A3	2			1		K1		
UNIT B1	3	1			1	K3		
UNIT B2 FA	3		1		1	K4		
50								

KITCHEN TOTAL QTY = 50

VANITY TOTAL QTY = 62

MATRIX			
DATE:		SHEET NUMBER:	
PROJECT #:	REV:	DIMENSION:	DRAWN BY:
ITALIAN KITCHEN AND BATH	CASA FAMILIA	KITCHEN VANITIES	
	kitchen bath tile closet		
	1777 NW 72TH AVE. MIAMI FL, 33126		
	T. 305.599.9000 F. 305.599.9870		

KITCHEN TYPE K
UNIT A1

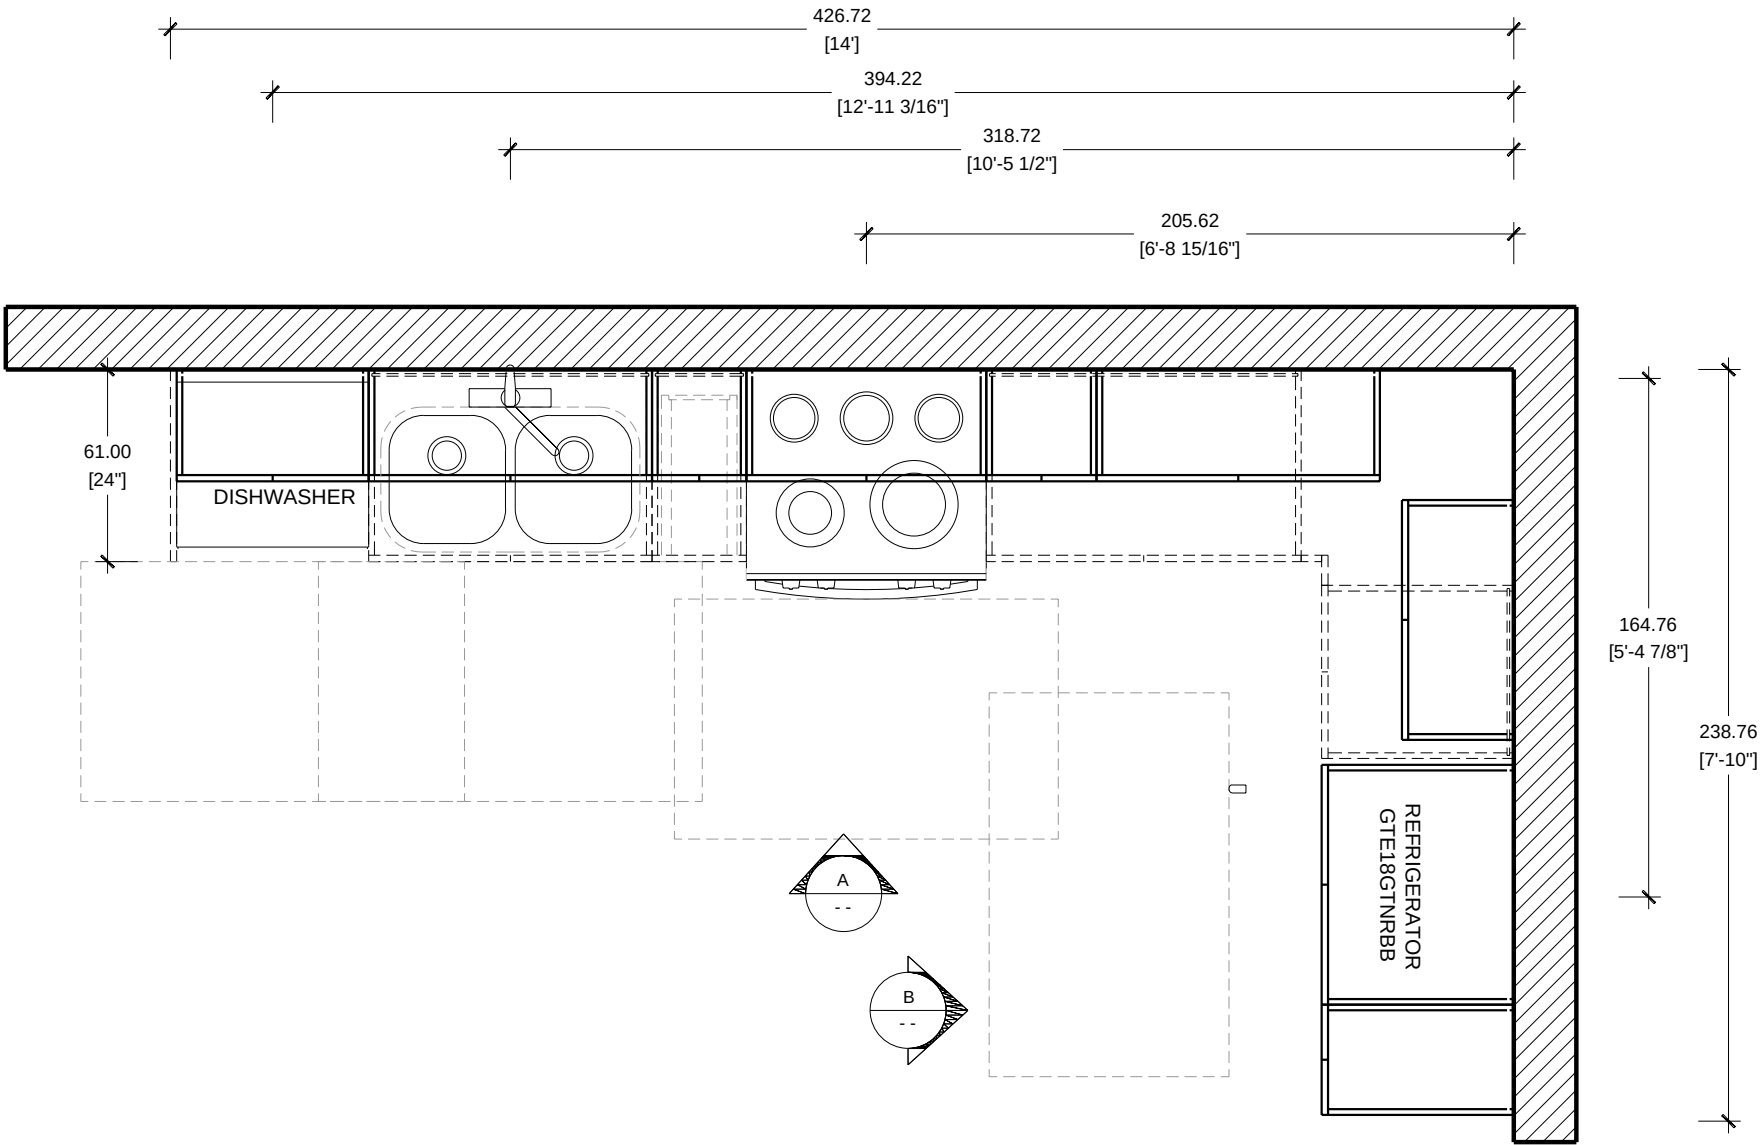

FLOOR PLAN SCALE 1/2"=1'-0"
CASA FAMILIA UNIT A1 / KITCHEN TYPE K1


A.1			
SHEET NUMBER			
DATE:	PROJECT #:	DRAWN BY:	
REV:	CASA FAMILIA	KITCHEN VANITIES	
DIMENSION:			
ITALIAN KITCHEN AND BATH			
Kitchen bath tile closet			
1777 NW 72TH AVE. MIAMI FL, 33126			
T. 305.599.9000 F. 305.599.9870			

KITCHEN TYPE K1


UNIT A1

A.2			
DATE:	REV:	DIMENSION:	DRAWN BY:

ITALIAN KITCHEN AND BATH	
kitchen bath tile closet	
1777 NW 72TH AVE. MIAMI FL. 33126	
T. 305.599.9000 F. 305.599.9870	

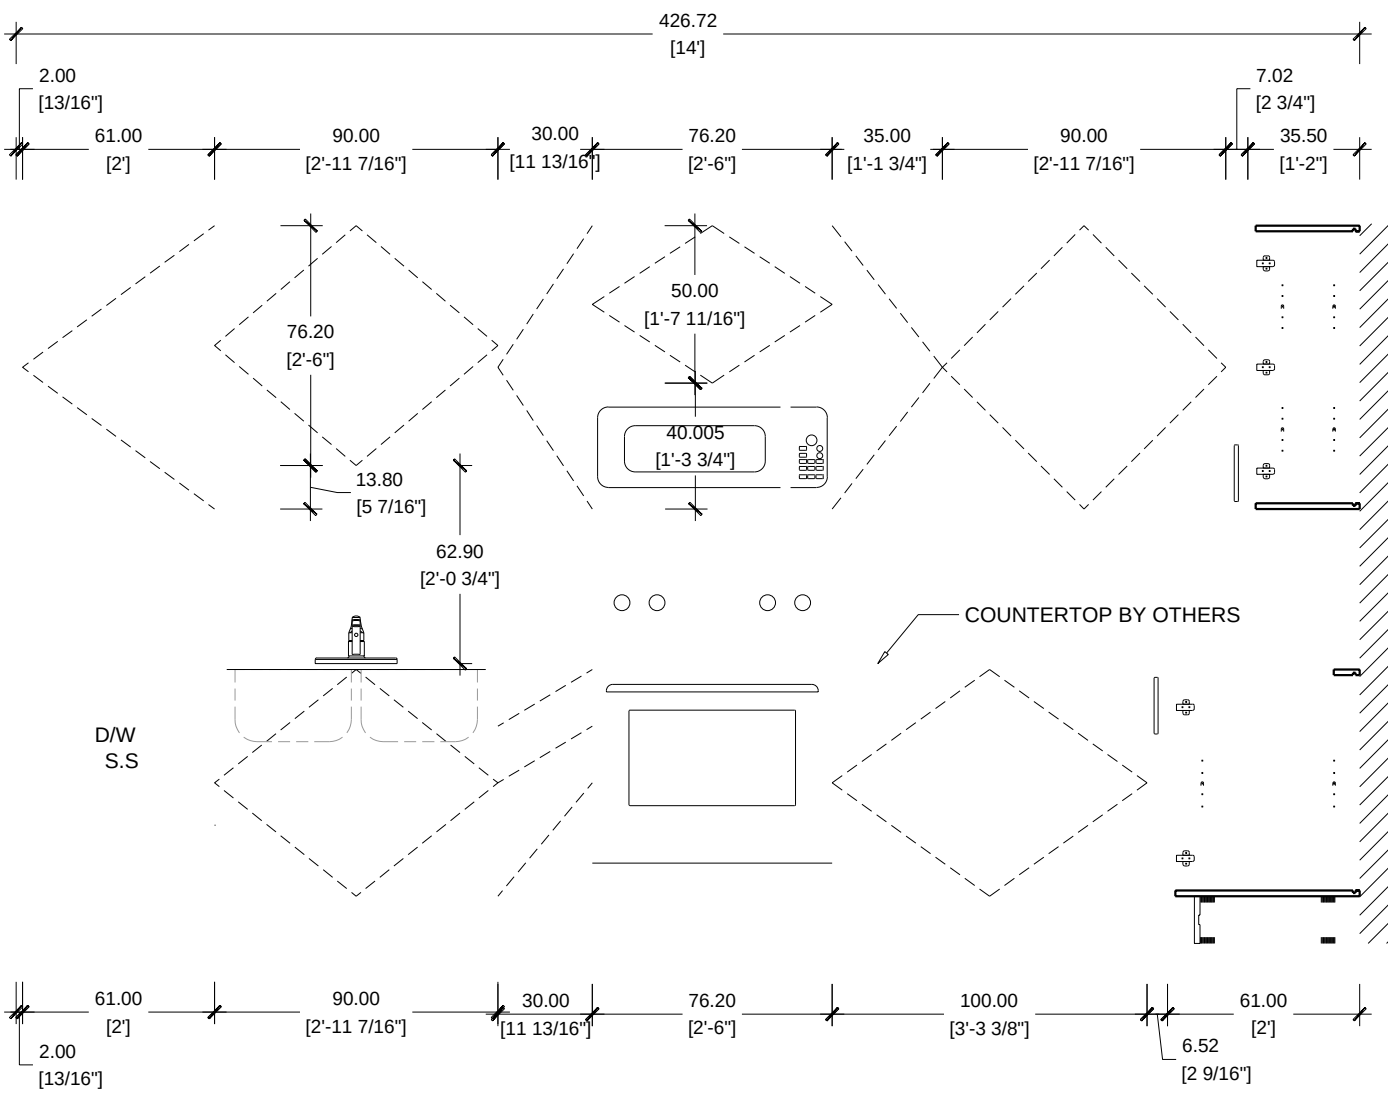


ELEVATION A
CASA FAMILIA UNIT A1 / KITCHEN TYPE K1

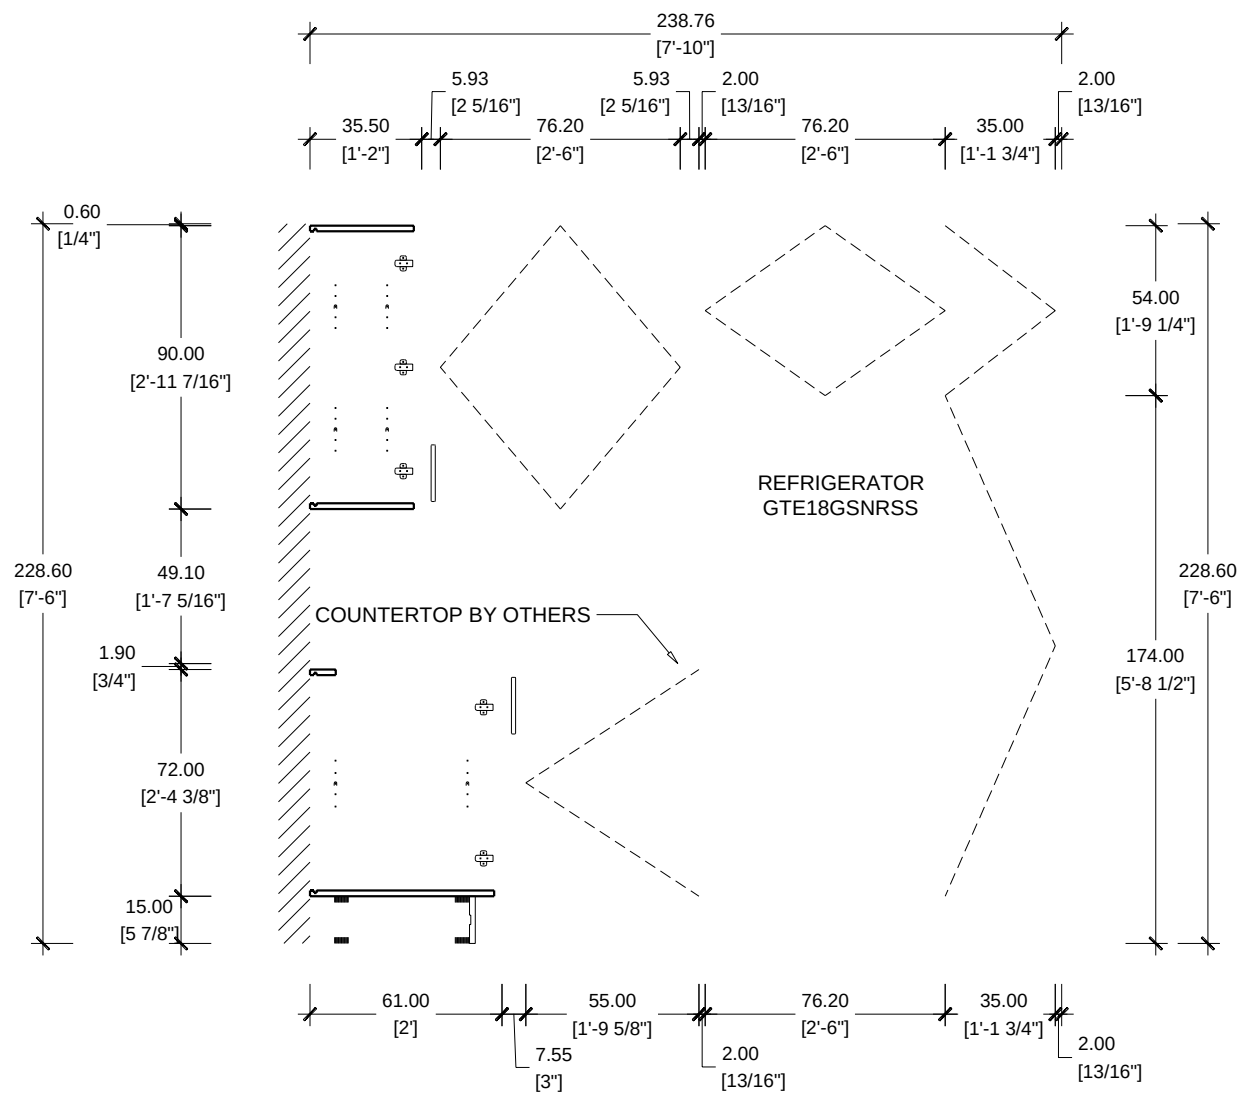


ELEVATION B
CASA FAMILIA UNIT A1 / KITCHEN TYPE K1

VANITY TYPE V
UNIT A1

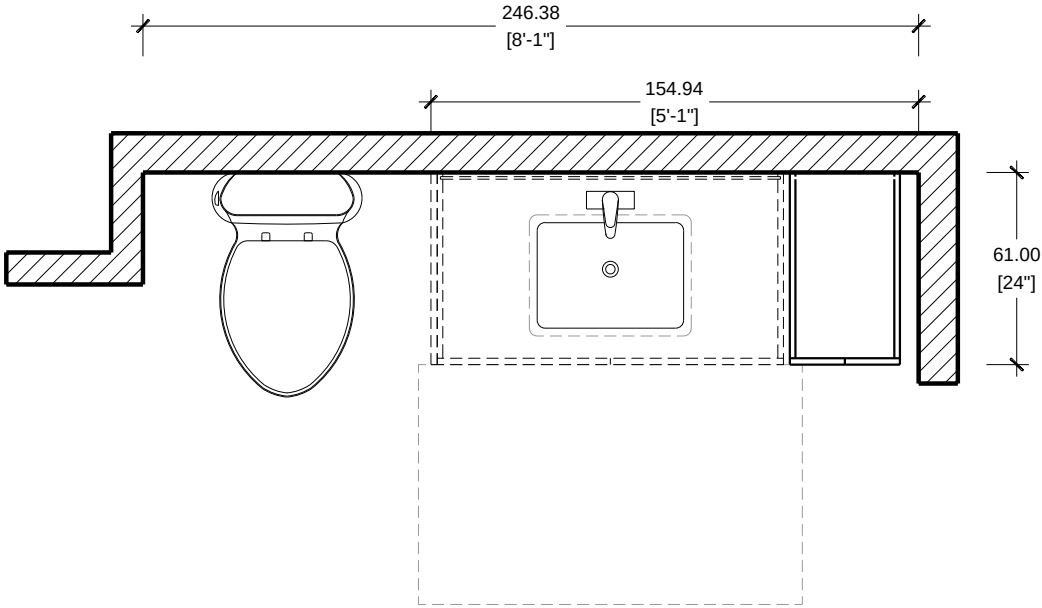


FLOOR PLAN SCALE 1/2"=1'-0"
CASA FAMILIA UNIT A1 /VANITY TYPE V1

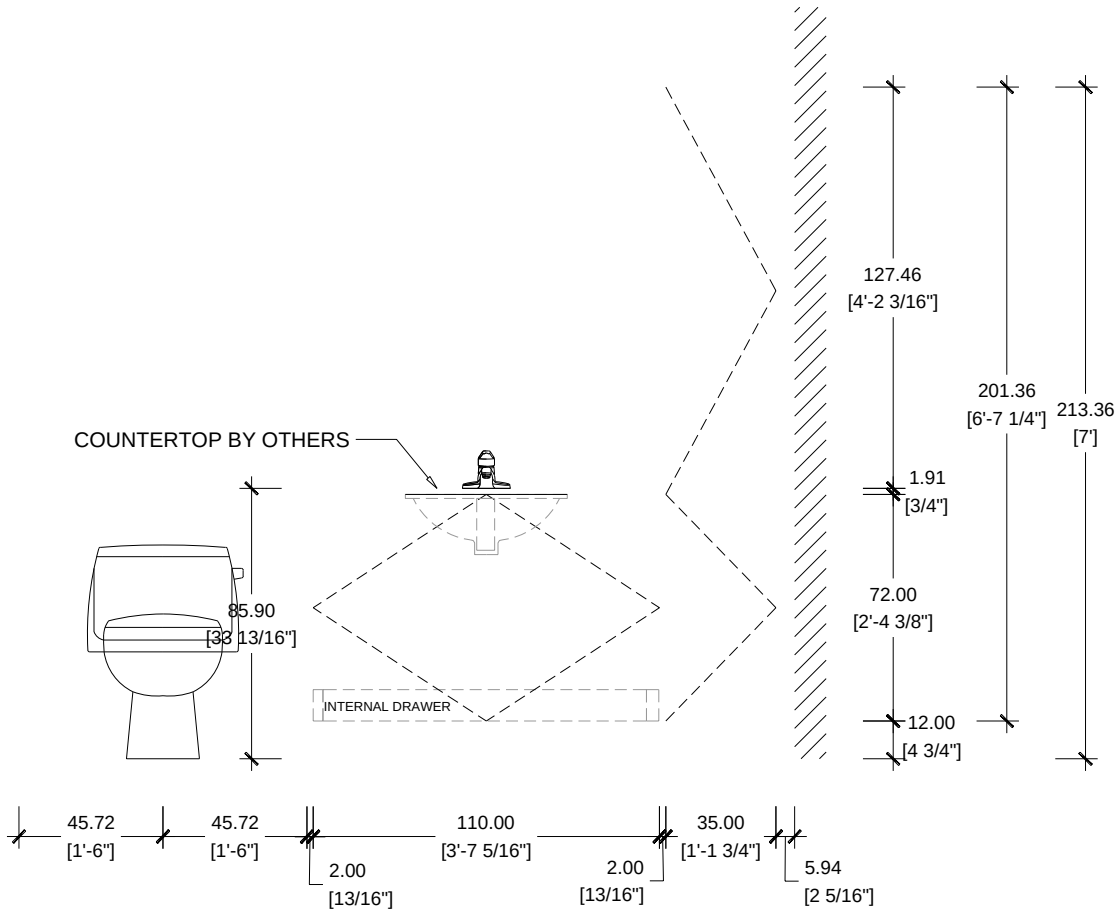

ELEVATION A
CASA FAMILIA UNIT A1 / VANITY TYPE V1

ITALIAN KITCHEN AND BATH			A3	
PROJECT #:	CASA FAMILIA	KITCHEN VANITIES	SHEET NUMBER	
			REV:	
			DIMENSION	
			DRAWN BY:	
kitchen bath tile closet				
1777 NW 72TH AVE. MIAMI FL, 33126				
T. 305.599.9000 F. 305.599.9870				

KITCHEN TYPE K2
UNIT A2 FA



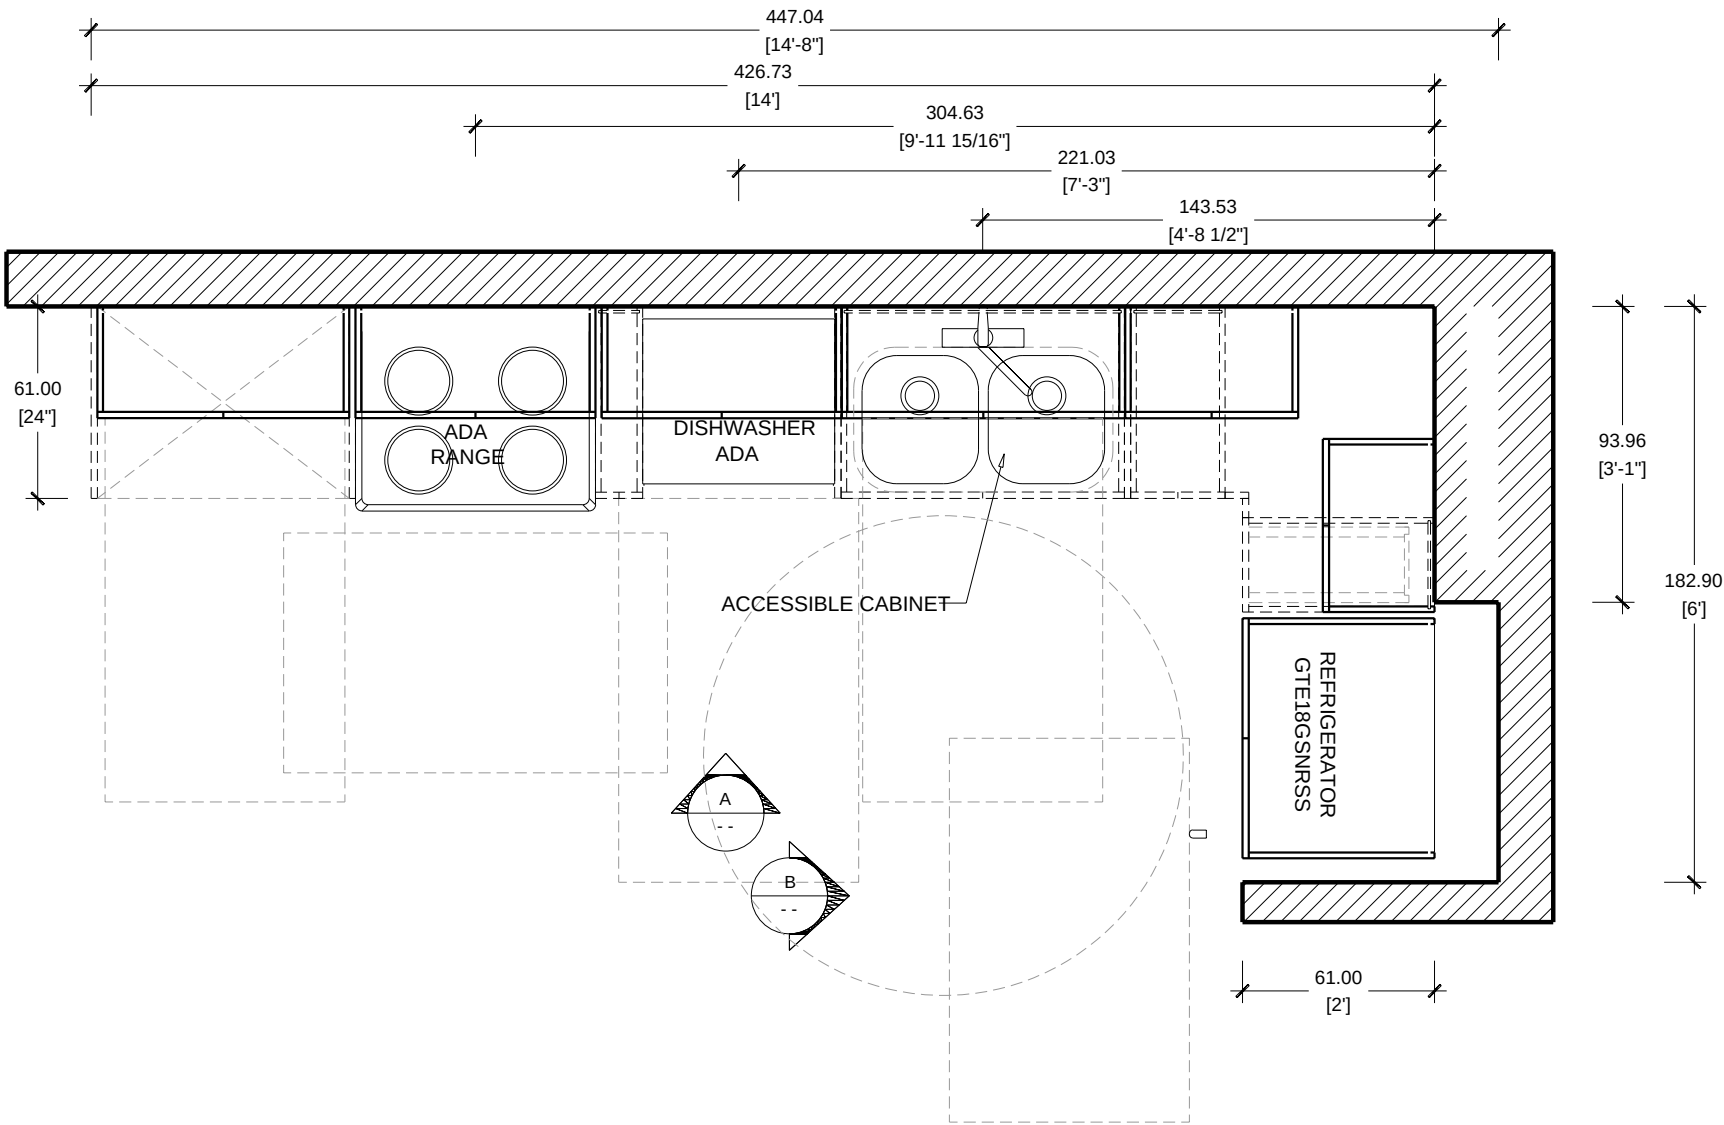


FLOOR PLAN SCALE 1/2"=1'-0"
CASA FAMILIA UNIT A2 FA / KITCHEN TYPE K2 ADA

A.4			
SHEET NUMBER			
DATE:	PROJECT #:	DRAWN BY:	
REV:	CASA FAMILIA		
DIMENSION:	KITCHEN VANITIES		
ITALIAN KITCHEN AND BATH			
Kitchen bath tile closet			
1777 NW 72TH AVE. MIAMI FL, 33126			
T. 305.599.9000 F. 305.599.9870			

KITCHEN TYPE K2
UNIT A2 FA

PROJECT #:		DATE:		SHEET NUMBER		A.5	
CASA FAMILIA		REV:		DIMENSIONS:		DRAWN BY:	
KITCHEN VANITIES							

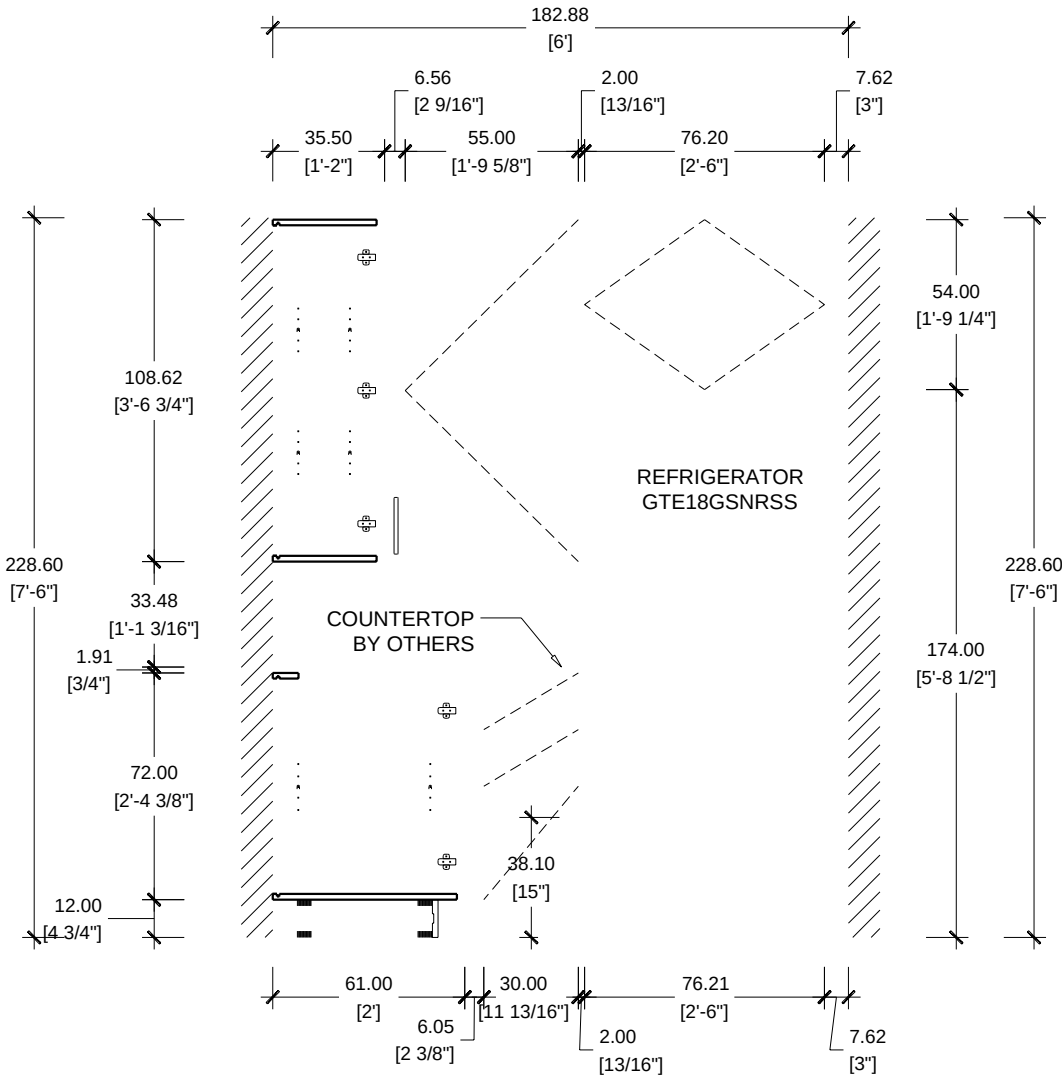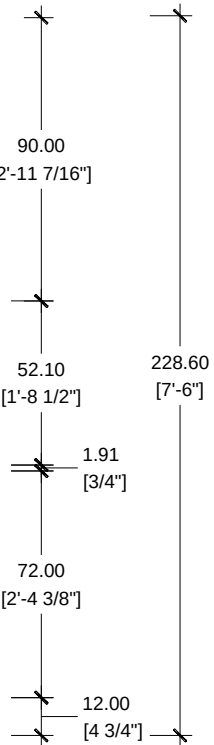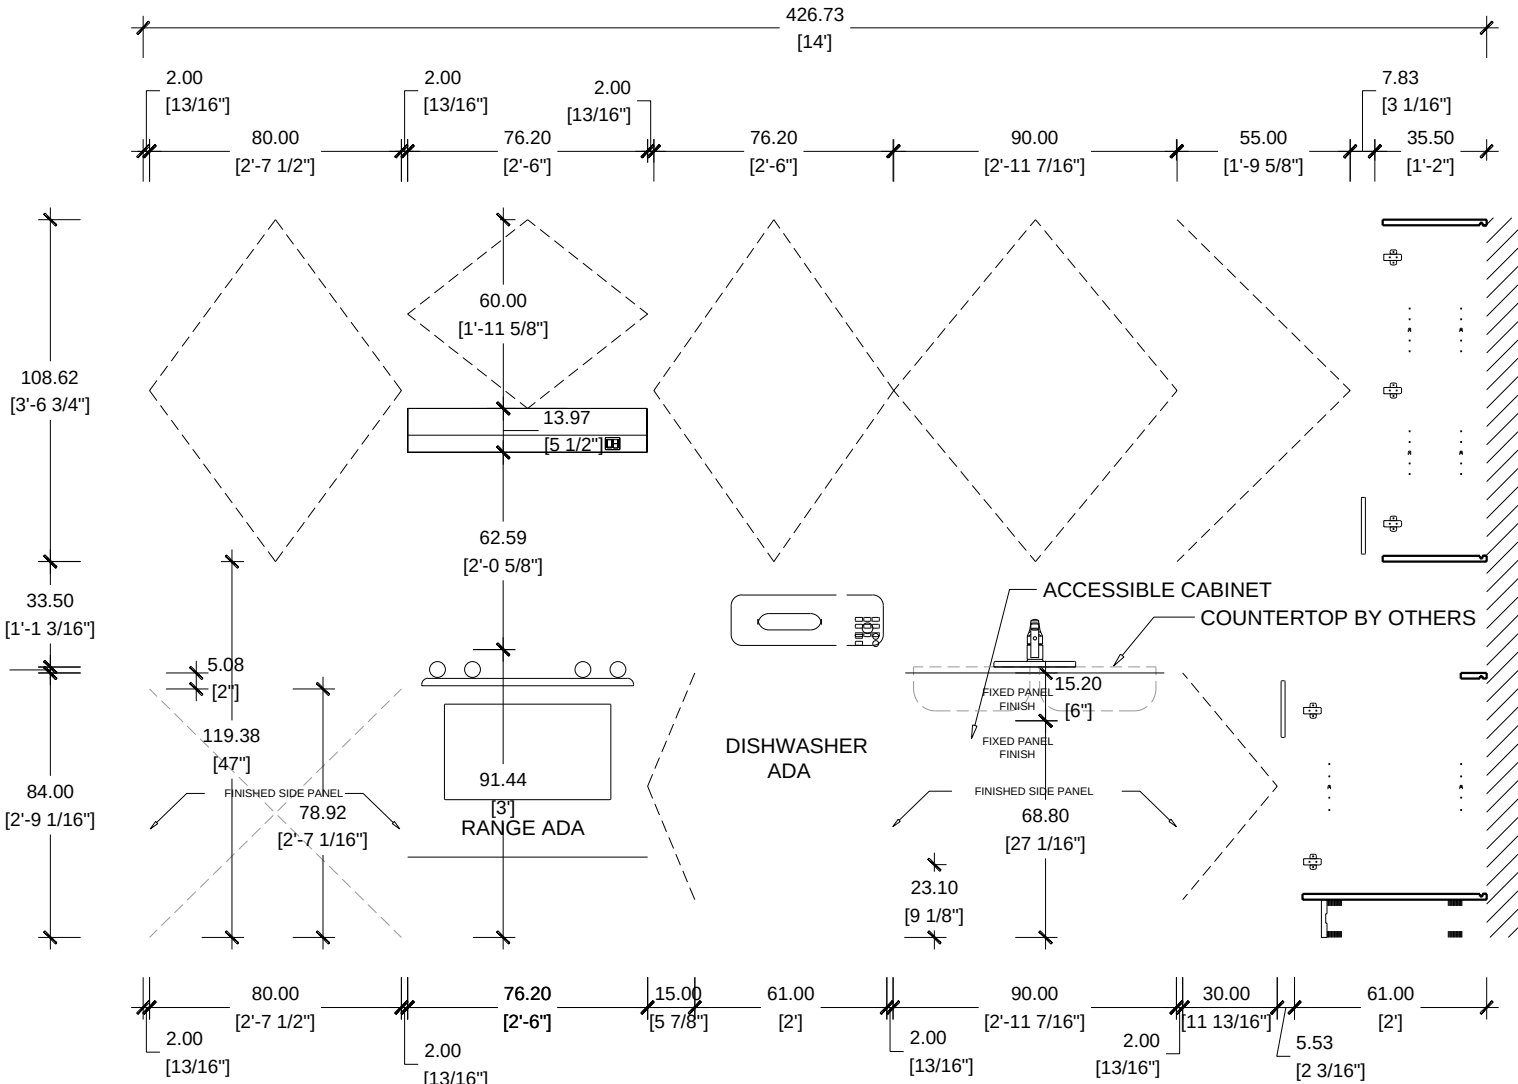


ELEVATION A


CASA FAMILIA UNIT A2 FA / KITCHEN TYPE K2 ADA

ELEVATION B


CASA FAMILIA UNIT A2 FA / KITCHEN TYPE K2 ADA

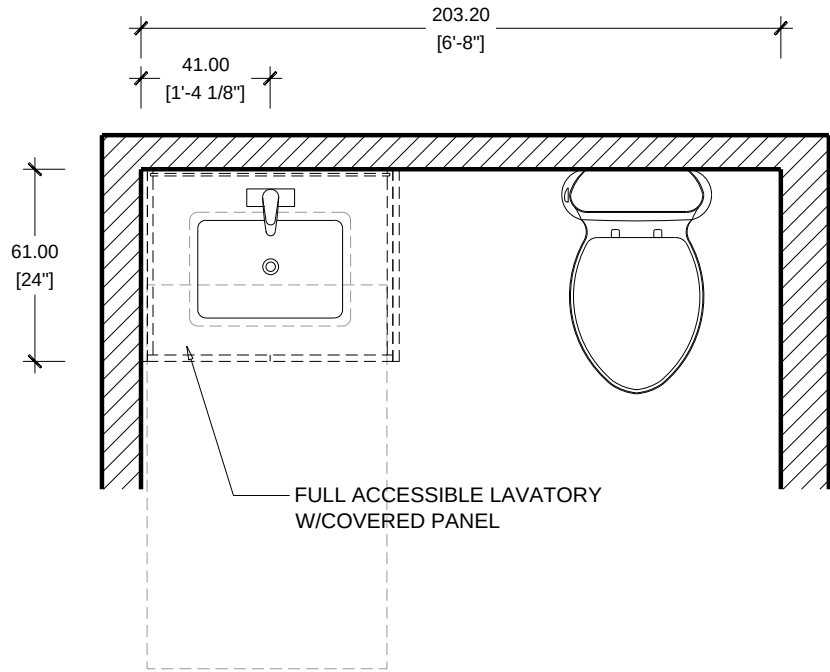


FLOOR PLAN SCALE 1/2"=1'-0"
CASA FAMILIA UNIT A2 FA /VANITY TYPE V2

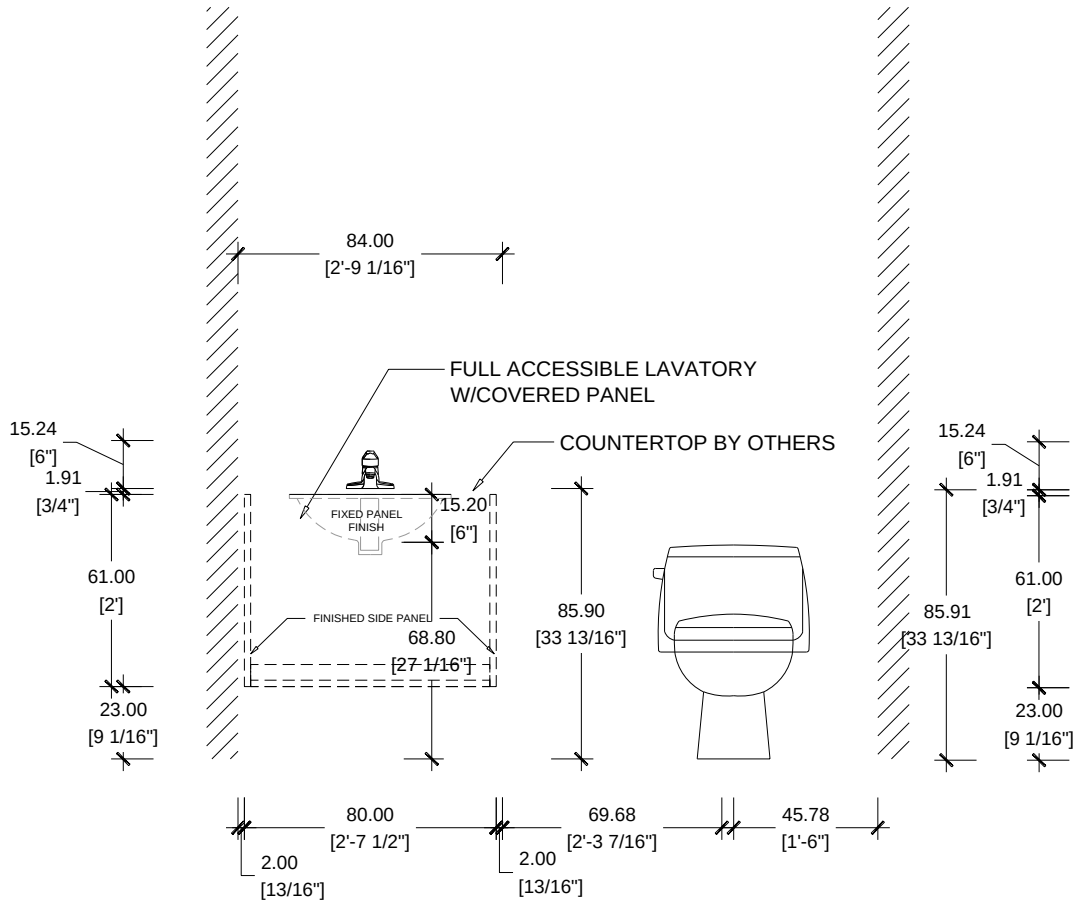

ELEVATION A
CASA FAMILIA UNIT A2 FA / VANITY TYPE V2

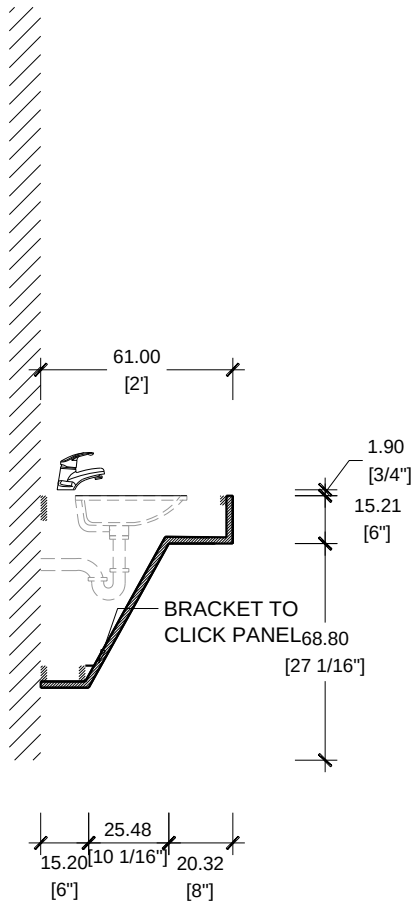

SECTION SCALE 1/2"=1'-0"
CASA FAMILIA UNIT A2 FA/ VANITY TYPE V2

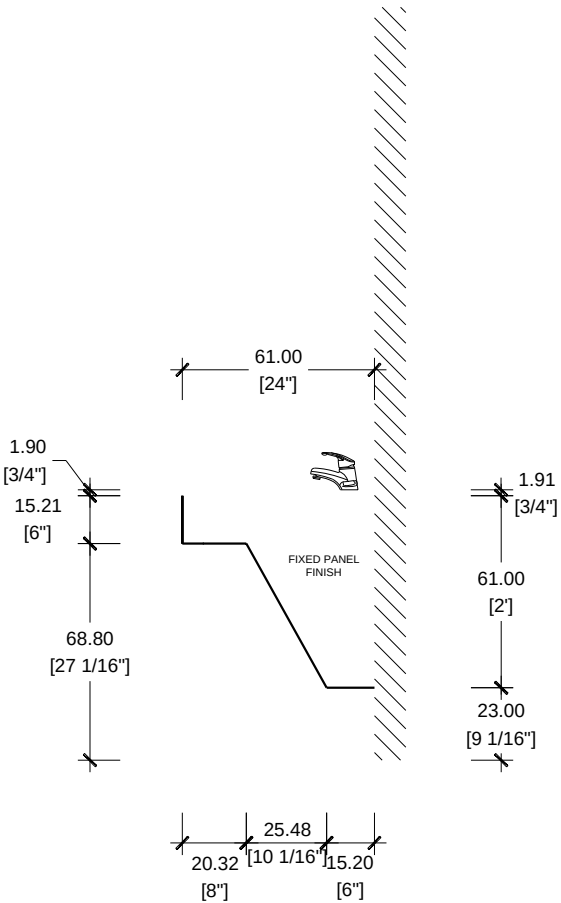


SIDE VIEW SCALE 1/2"=1'-0"
CASA FAMILIA / VANITY TYPE V2

VANITY TYPE V2

UNIT A2 FA

A.6			
DATE:	REV:	DIMENSIONS:	DRAWN BY:
PROJECT #:			
CASA FAMILIA			
KITCHEN VANITIES			
ITALIAN KITCHEN AND BATH			
Kitchen bath tile closet			
1777 NW 72TH AVE. MIAMI FL, 33126			
T. 305.599.9000 F. 305.599.9870			

KITCHEN TYPE K1
UNIT A3

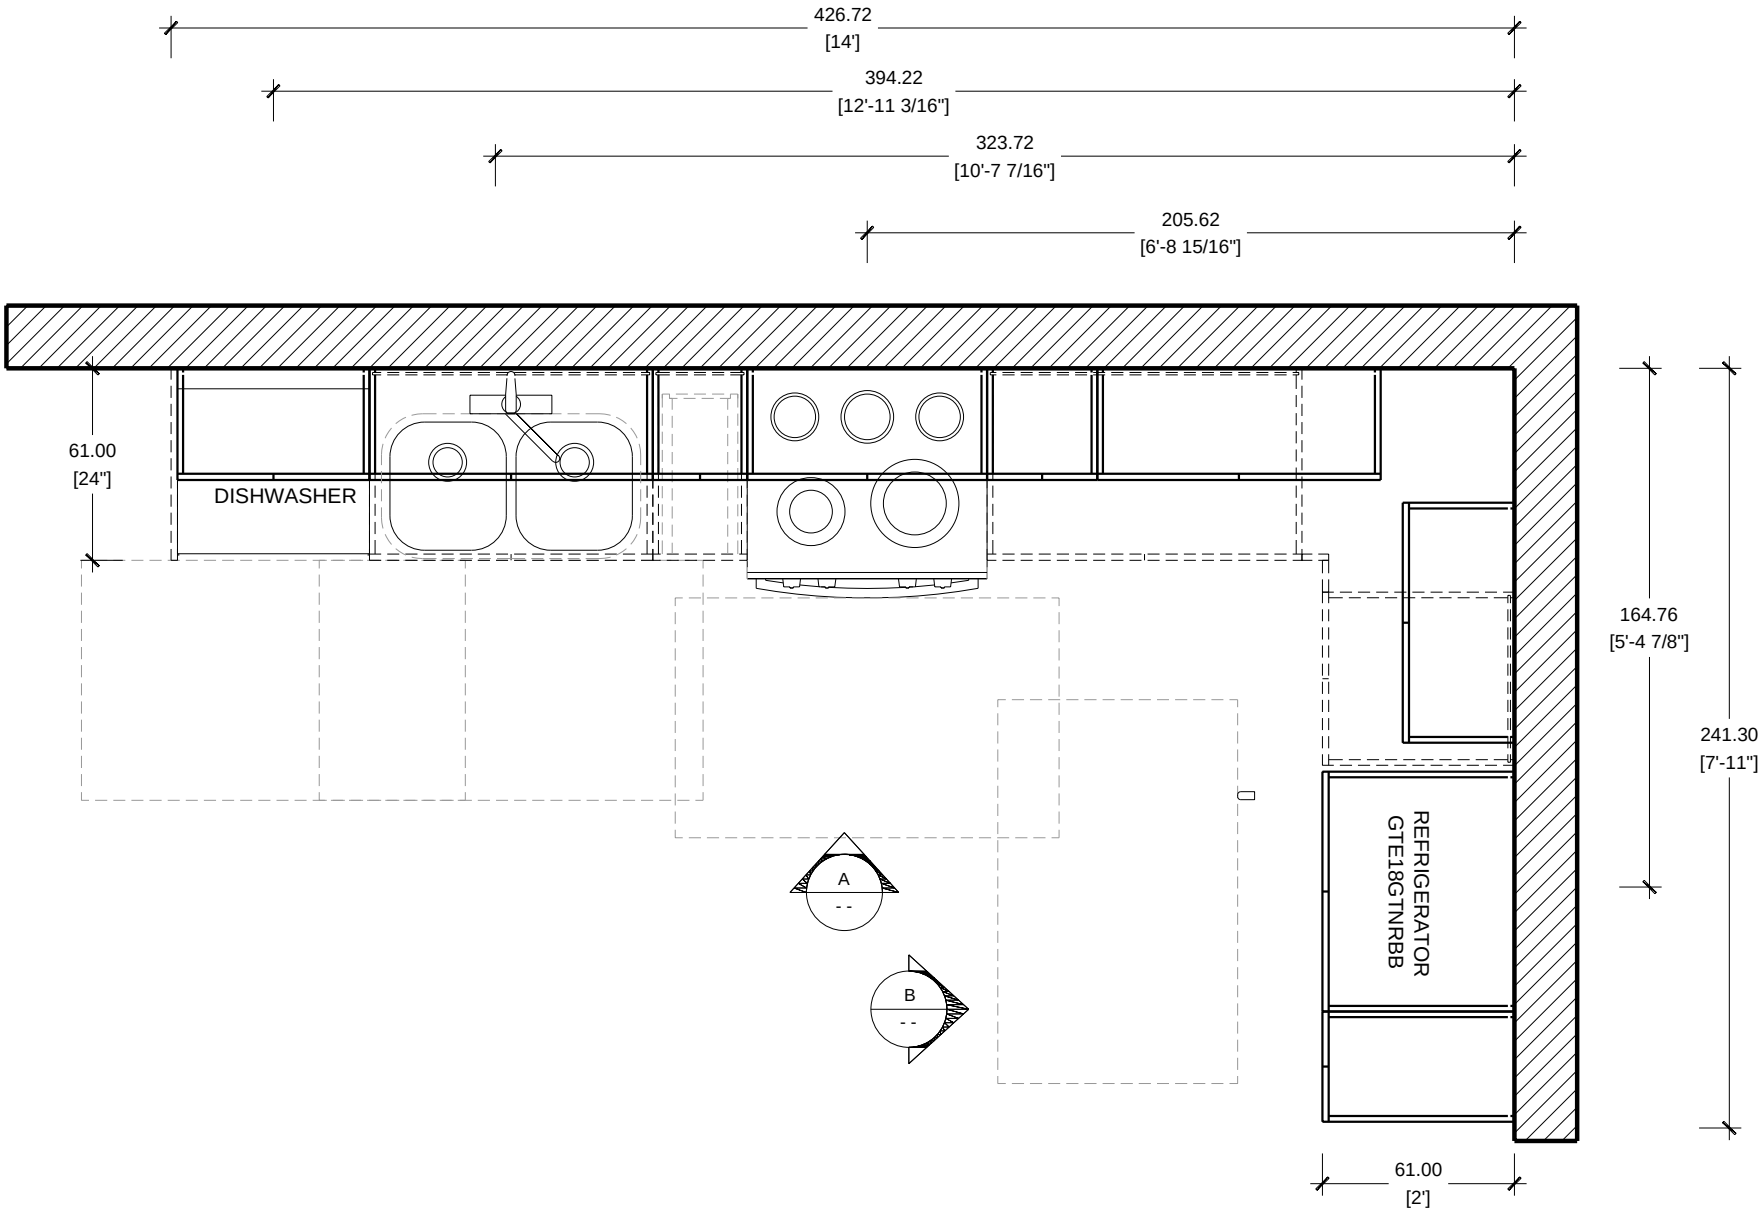


FLOOR PLAN SCALE 1/2"=1'-0"
CASA FAMILIA UNIT A3/ KITCHEN TYPE K1


PROJECT #:		DATE:	SHEET NUMBER: A.7	
CASA FAMILIA		REV:	DRAWN BY:	
KITCHEN VANITIES		DIMENSION:		

KITCHEN TYPE K1
UNIT A3

A.8			
SHEET NUMBER			
DATE:	REV:	DIMENSION:	DRAWN BY:
PROJECT #:		CASA FAMILIA	KITCHEN VANITIES
ITALIAN KITCHEN AND BATH			
Kitchen bath tile closet			
1777 NW 72TH AVE. MIAMI FL. 33126			
T. 305.599.9000 F. 305.599.9870			

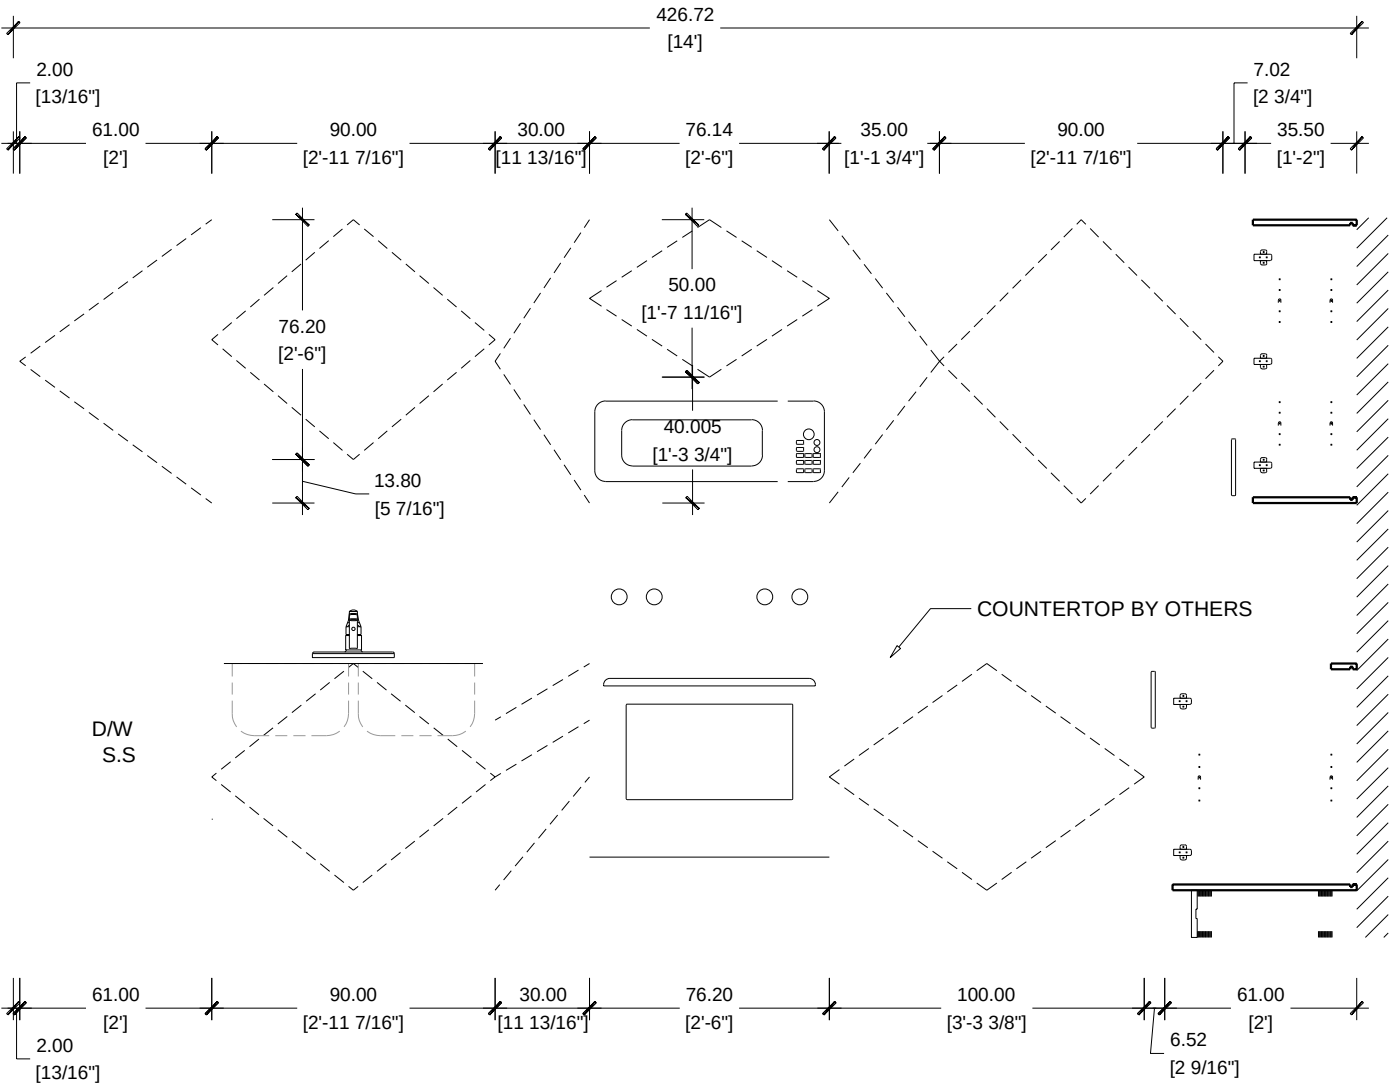


ELEVATION A
CASA FAMILIA UNIT A3 / KITCHEN TYPE K1

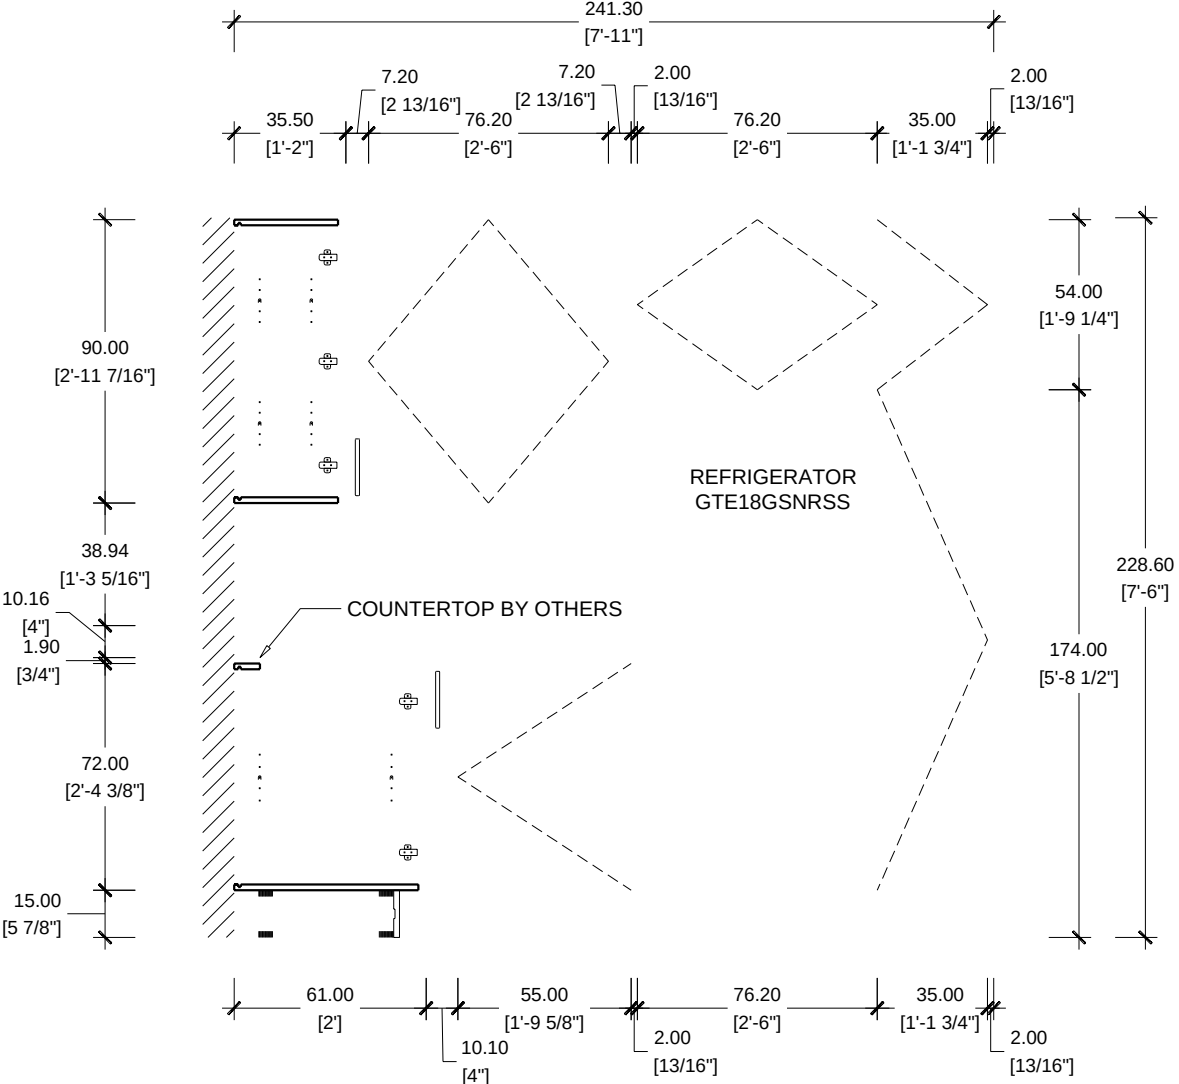


ELEVATION B
CASA FAMILIA UNIT A3 / KITCHEN TYPE K1

VANITY TYPE V3
UNIT A3

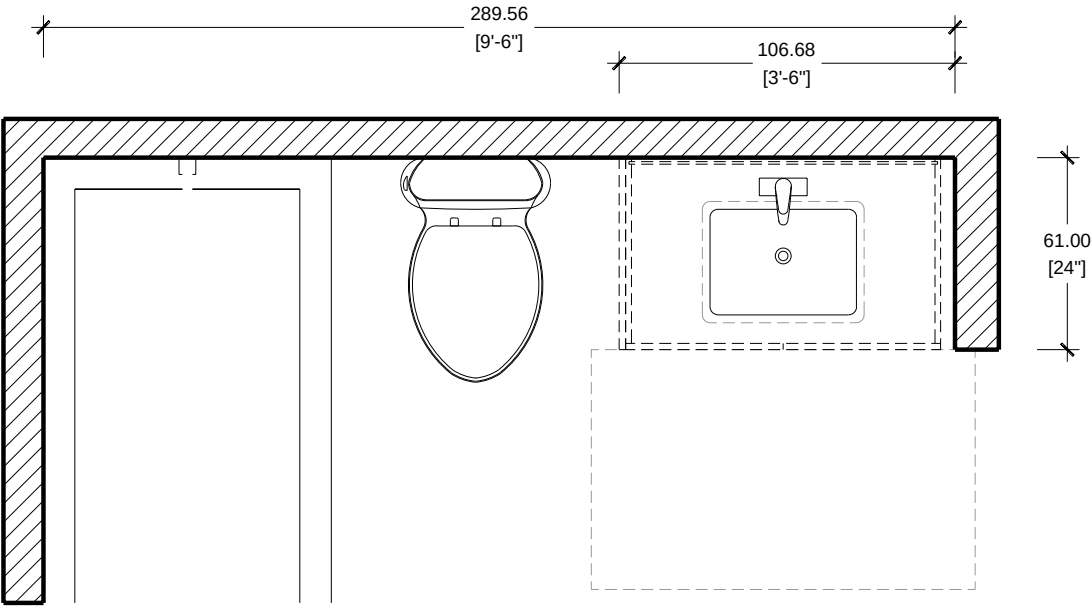


FLOOR PLAN SCALE 1/2"=1'-0"
CASA FAMILIA /VANITY TYPE V3

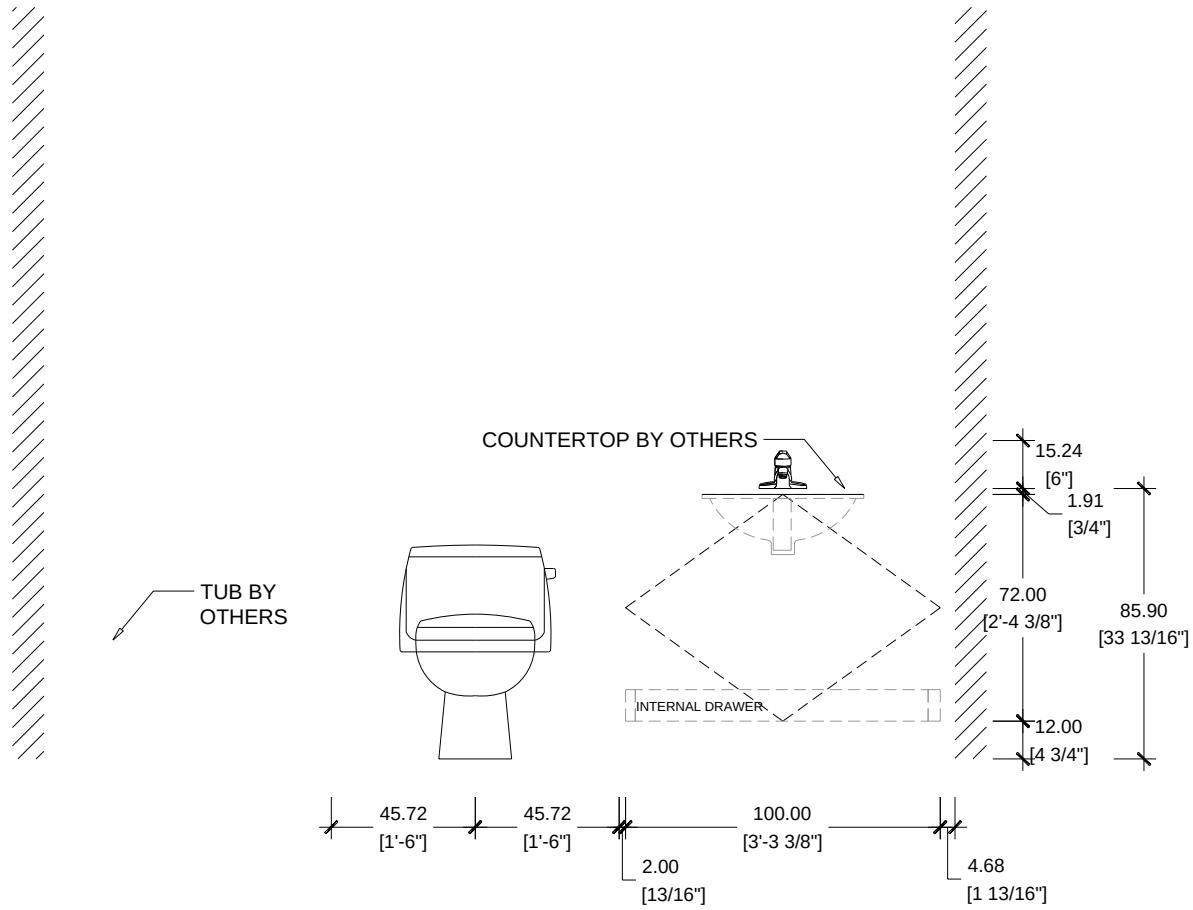

ELEVATION A
CASA FAMILIA UNIT A3 / VANITY TYPE V3

A.9			
DATE:	REV:	DIMENSION:	DRAWN BY:
PROJECT #:			
CASA FAMILIA			
KITCHEN VANITIES			
ITALIAN KITCHEN AND BATH			
Kitchen bath tile closet			
1777 NW 72TH AVE. MIAMI FL, 33126			
T. 305.599.9000 F. 305.599.9870			

KITCHEN TYPE K3
UNIT B1

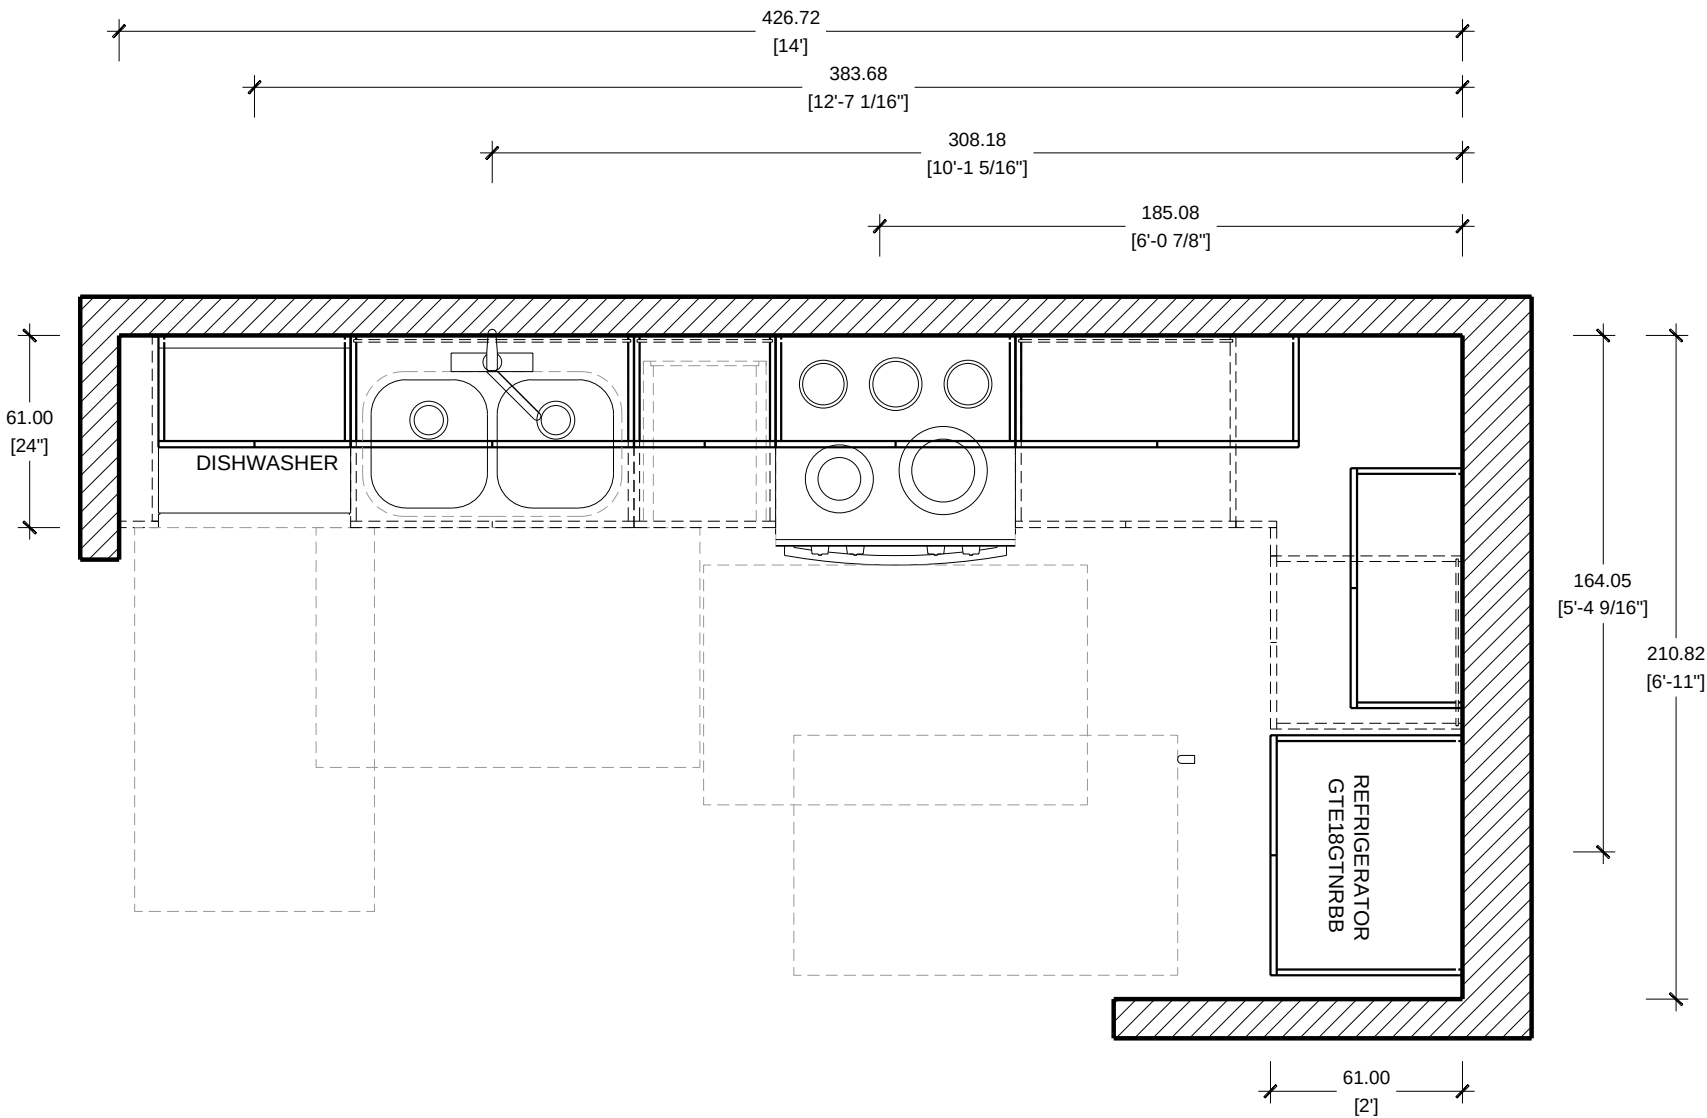


FLOOR PLAN SCALE 1/2"=1'-0"
CASA FAMILIA UNIT B1/ KITCHEN TYPE K3

A.10		SHEET NUMBER	
DATE:	PROJECT #:		
REV:	CASA FAMILIA		
DIMENSION:	KITCHEN VANITIES		
DRAWN BY:			
ITALIAN KITCHEN AND BATH			
kitchen bath tile closet			
1777 NW 72TH AVE. MIAMI FL, 33126			
T. 305.599.9000 F. 305.599.9870			


KITCHEN TYPE K3
UNIT B1

A.11			
DATE:	REV:	DIMENSION:	DRAWN BY:
SHEET NUMBER:			

PROJECT #:		CASA FAMILIA	
		KITCHEN VANITIES	
ITALIAN KITCHEN AND BATH			
Kitchen bath tile closet			
1.777 NW 72TH AVE. MIAMI FL. 33126			
T. 305.599.9000 F. 305.599.9870			

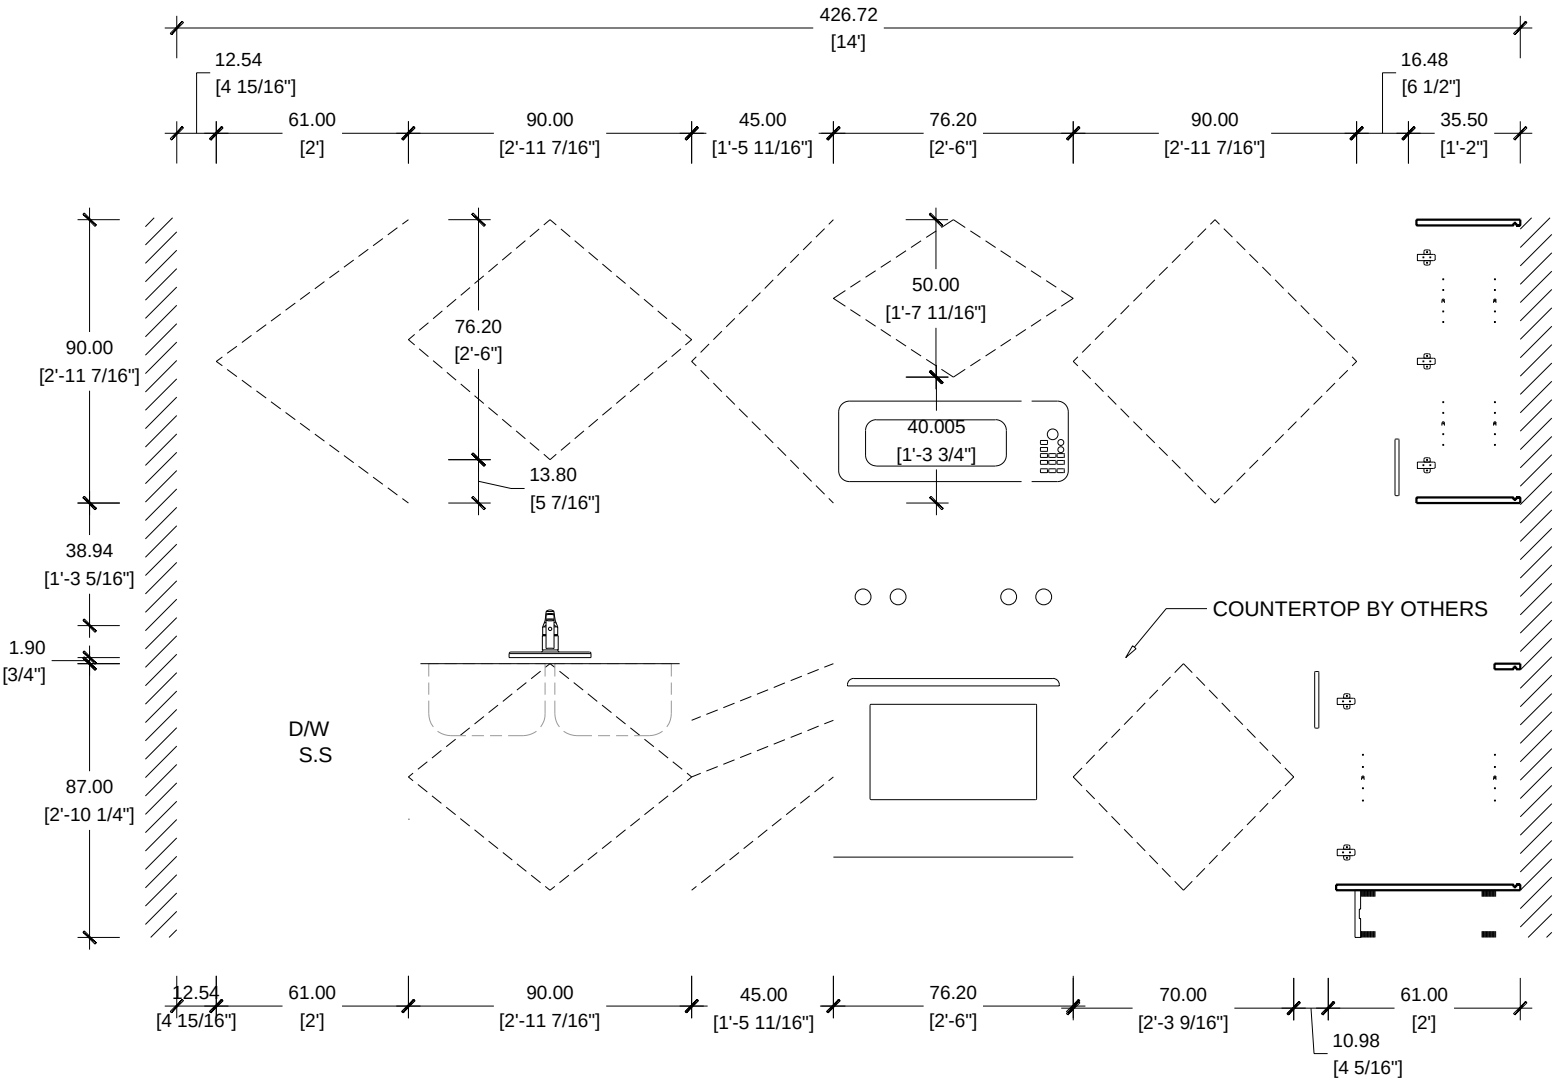


ELEVATION A
CASA FAMILIA UNIT B1 / KITCHEN TYPE K3

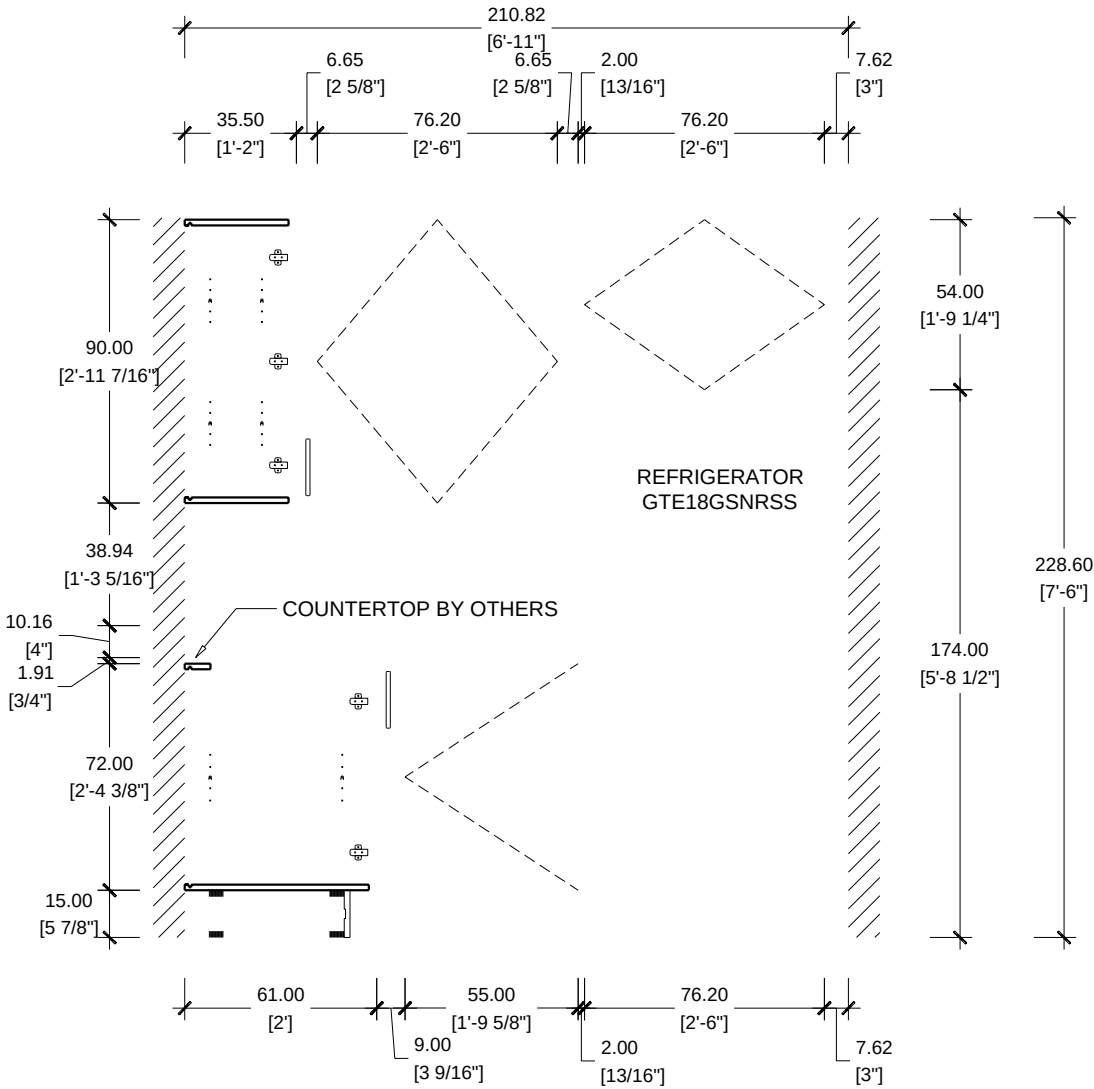

ELEVATION B
CASA FAMILIA UNIT B1 / KITCHEN TYPE K3



KITCHEN TYPE K4
UNIT B2FA

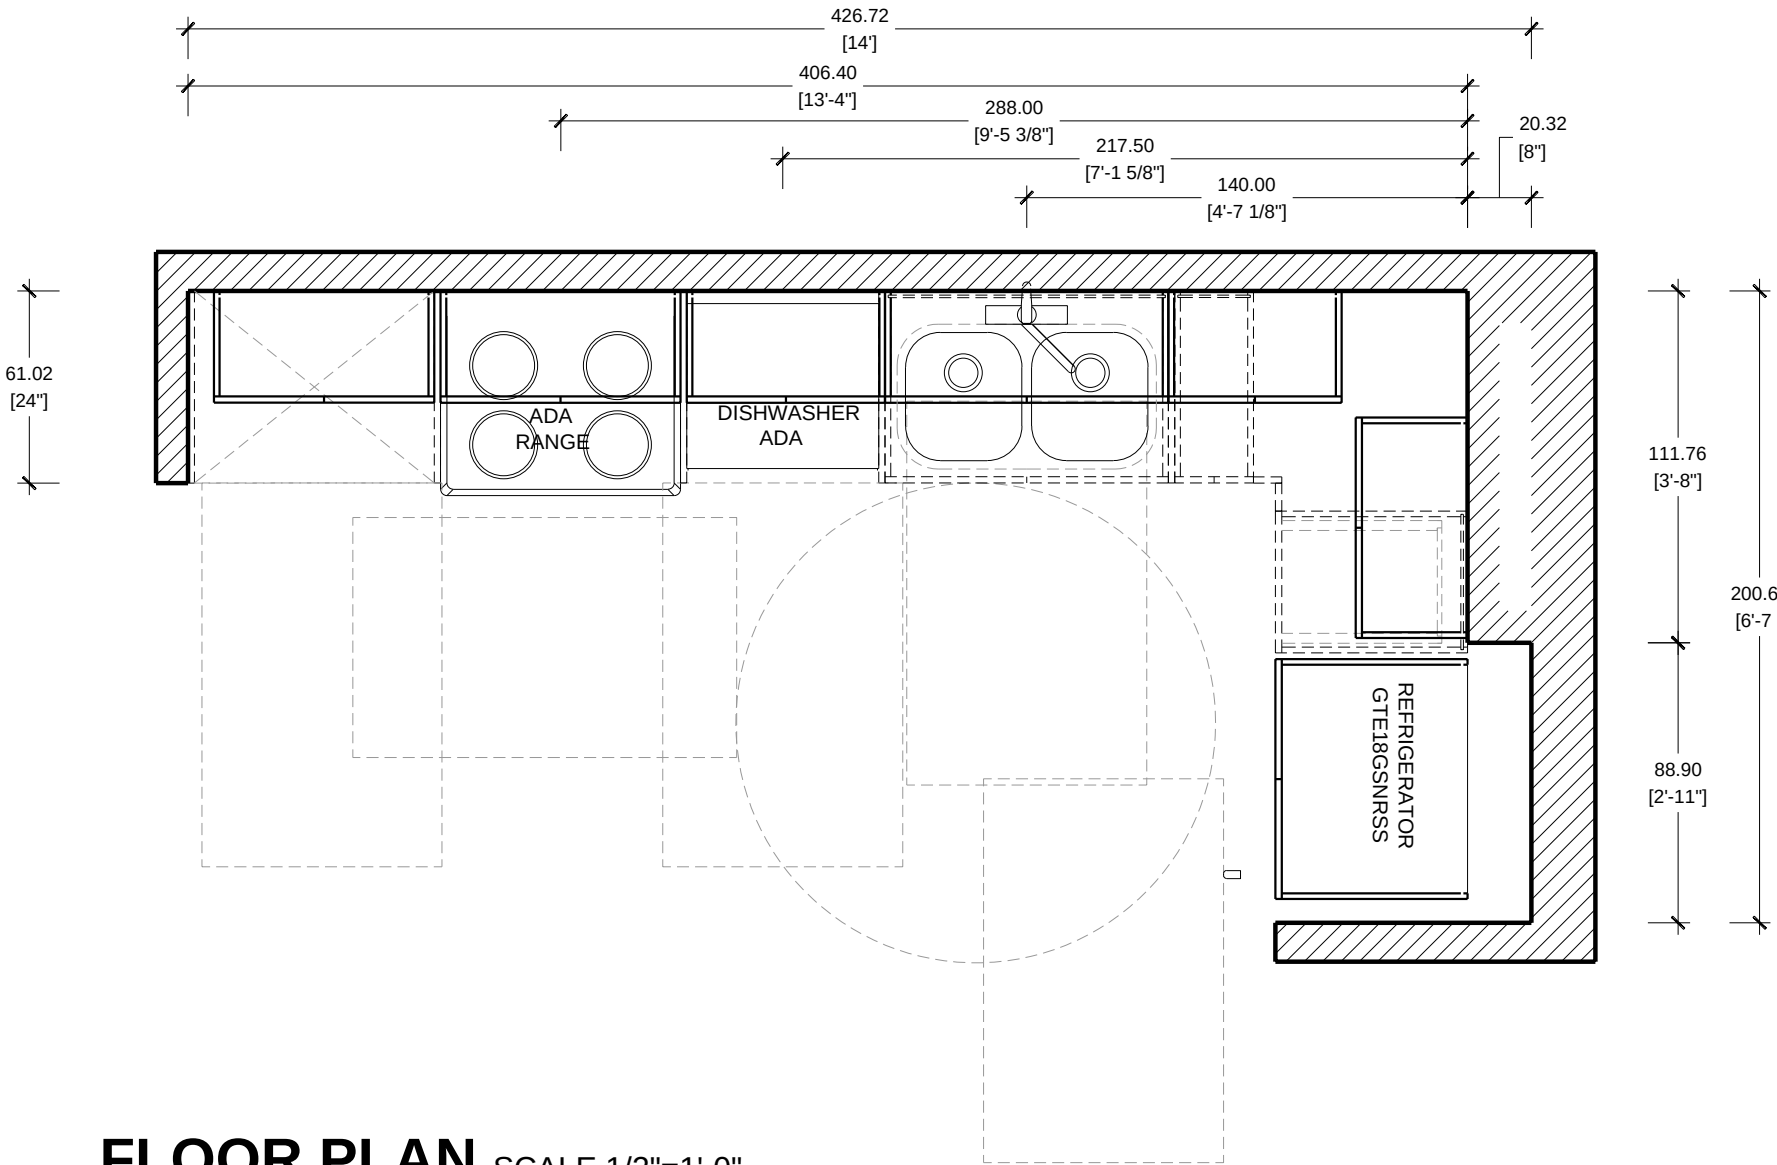


FLOOR PLAN SCALE 1/2"=1'-0"
CASA FAMILIA / KITCHEN TYPE K4 ADA

A.13			
SHEET NUMBER			
DATE:	PROJECT #:	REVISION:	DRAWN BY:
	CASA FAMILIA		
	KITCHEN VANITIES		
ITALIAN KITCHEN AND BATH			
Kitchen bath tile closet			
1777 NW 72TH AVE. MIAMI FL, 33126			
T. 305.599.9000 F. 305.599.9870			


KITCHEN TYPE K4
UNIT B2FA

ITALIAN KITCHEN AND BATH		PROJECT #:	DATE:
kitchen bath tile closet		CASA FAMILIA	REV:
1777 NW 72TH AVE. MIAMI FL. 33126		KITCHEN VANITIES	DIMENSION:
T. 305.599.9000 F. 305.599.9870			DRAWN BY:

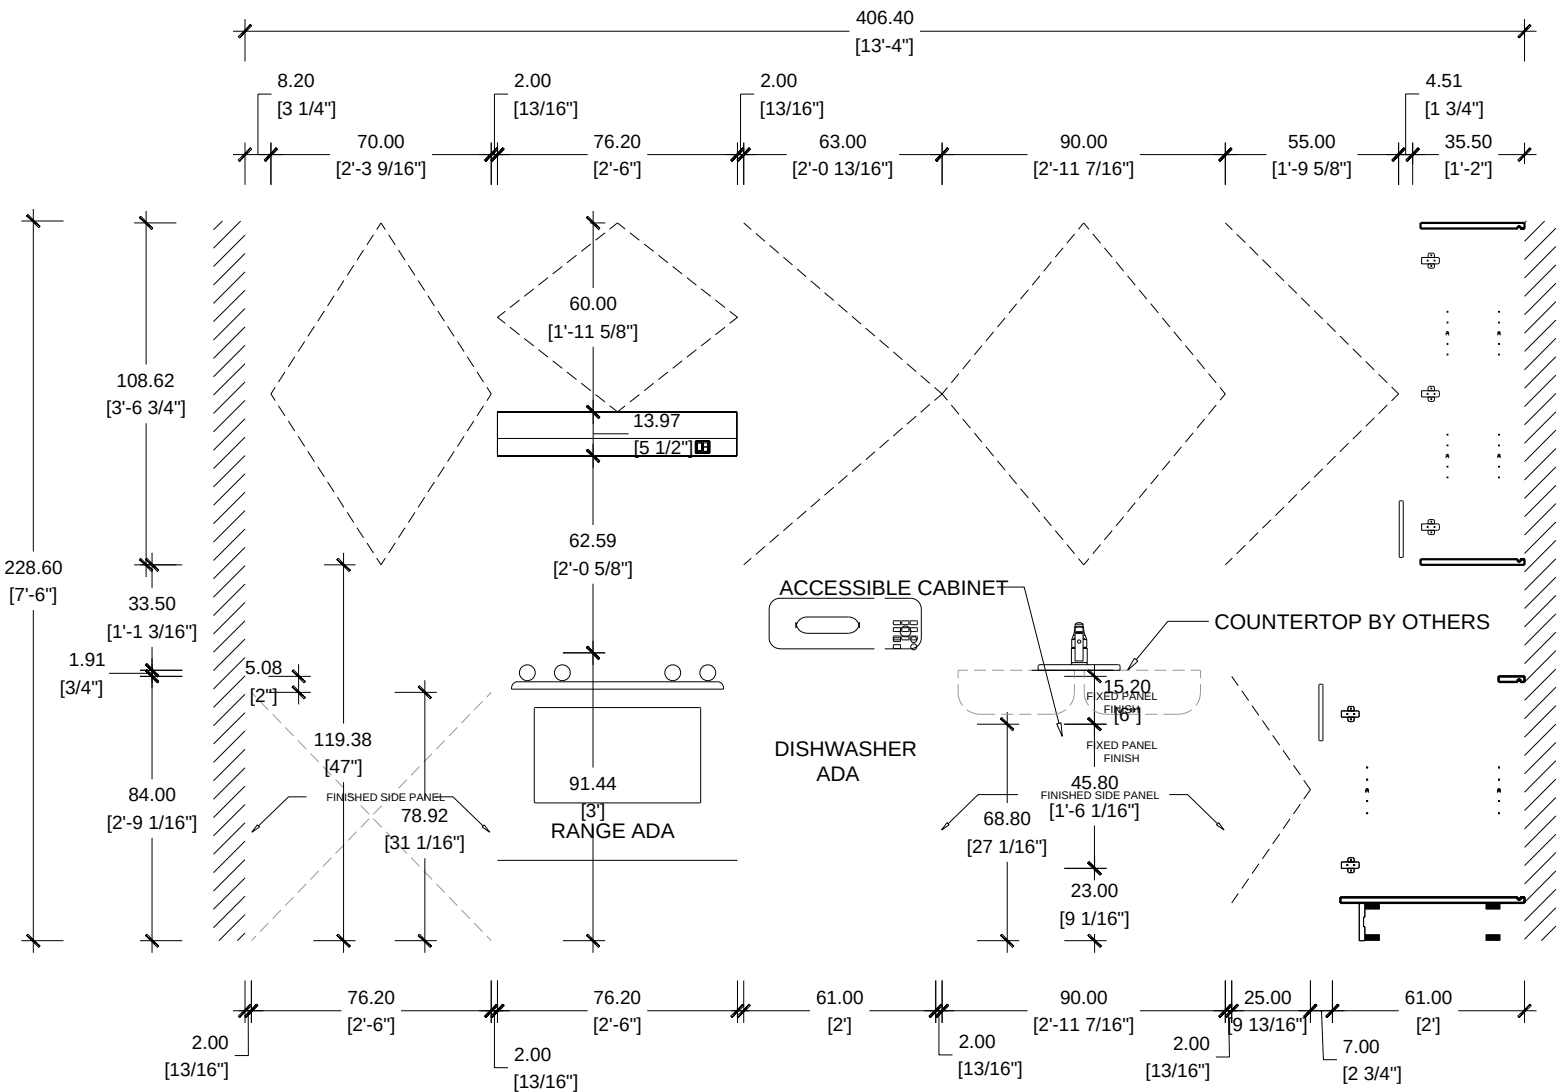


ELEVATION A

CASA FAMILIA UNIT B1 FA / KITCHEN TYPE K4 ADA

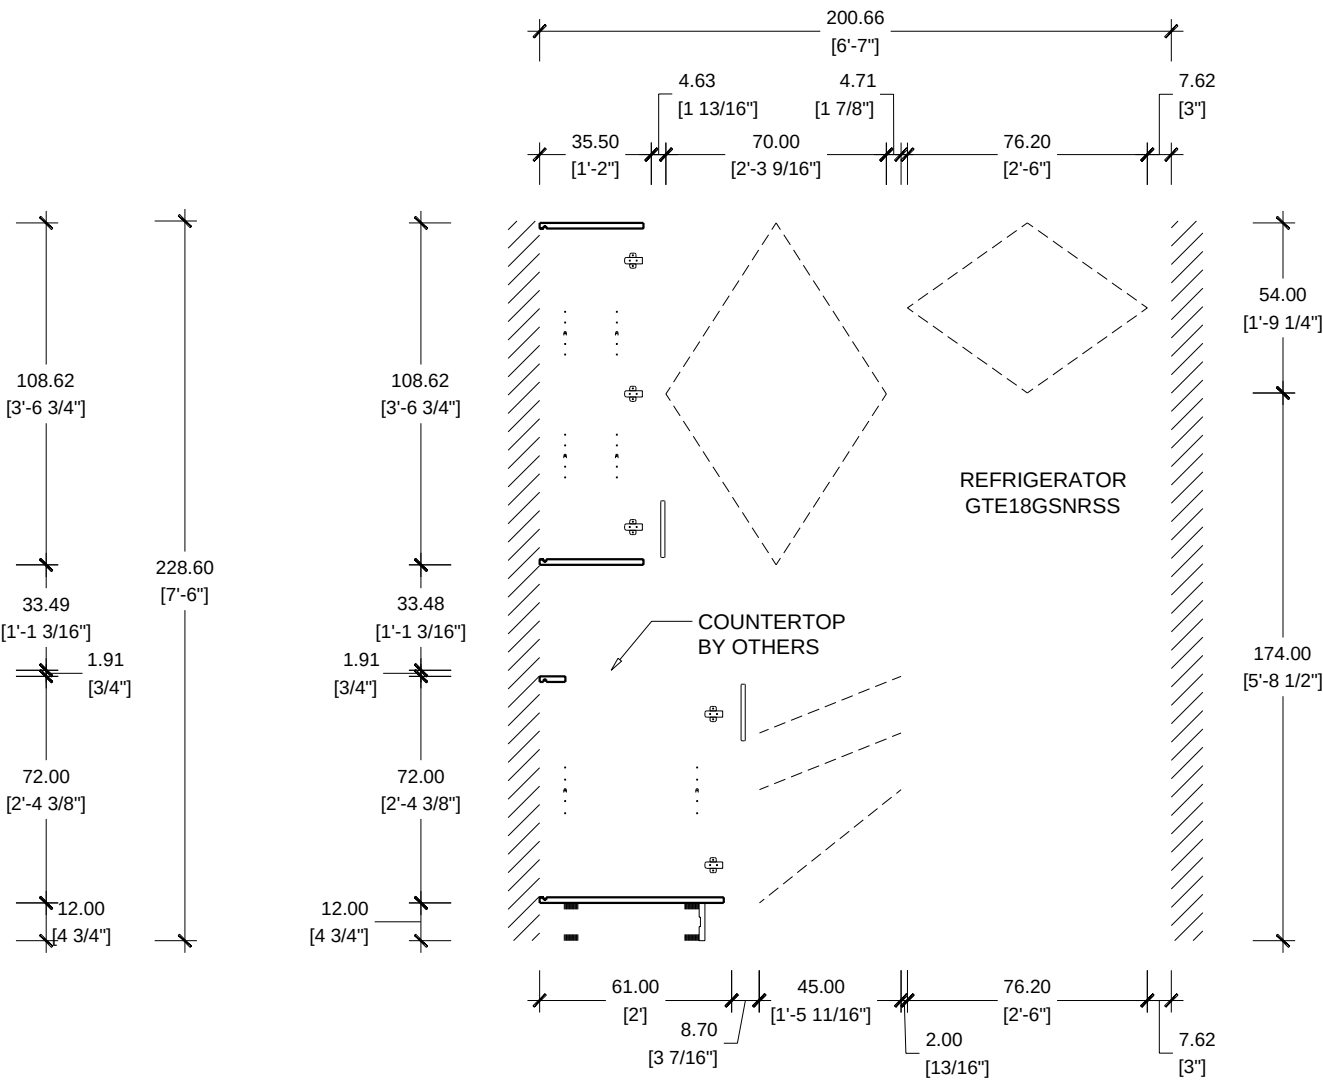


ELEVATION B

CASA FAMILIA UNIT B1 FA / KITCHEN TYPE K4 ADA

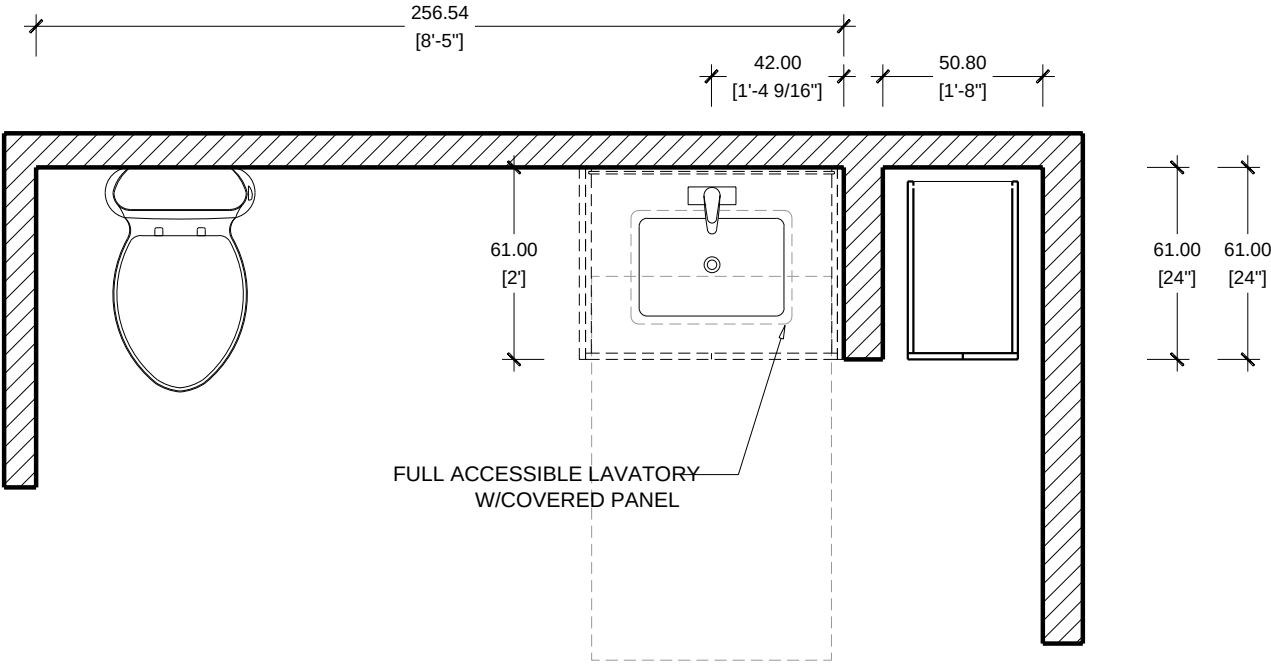


FLOOR PLAN SCALE 1/2"=1'-0"
CASA FAMILIA /VANITY TYPE RV2

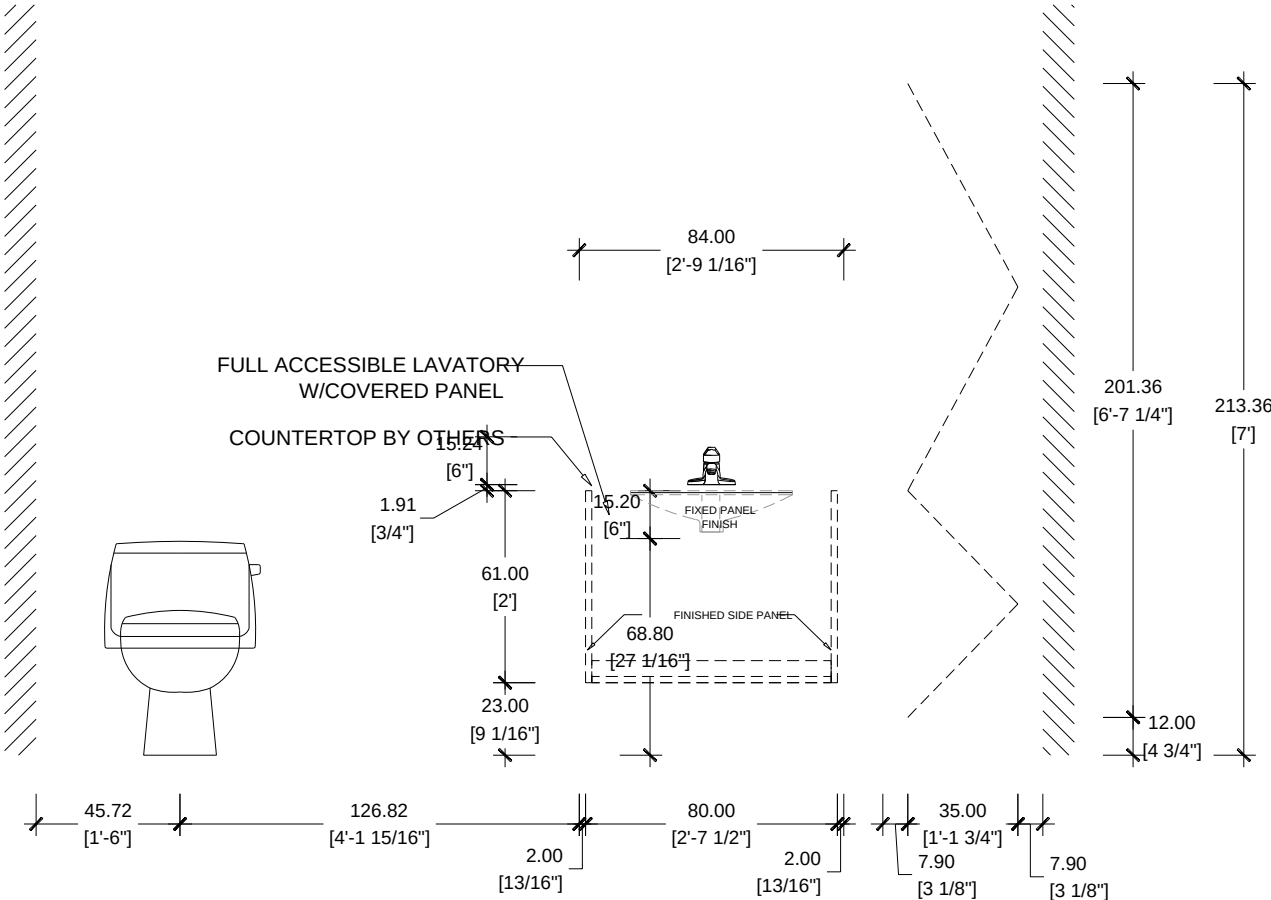

ELEVATION A
CASA FAMILIA / VANITY TYPE RV2

SECTION SCALE 1/2"=1'-0"
CASA FAMILIA / VANITY TYPE RV2

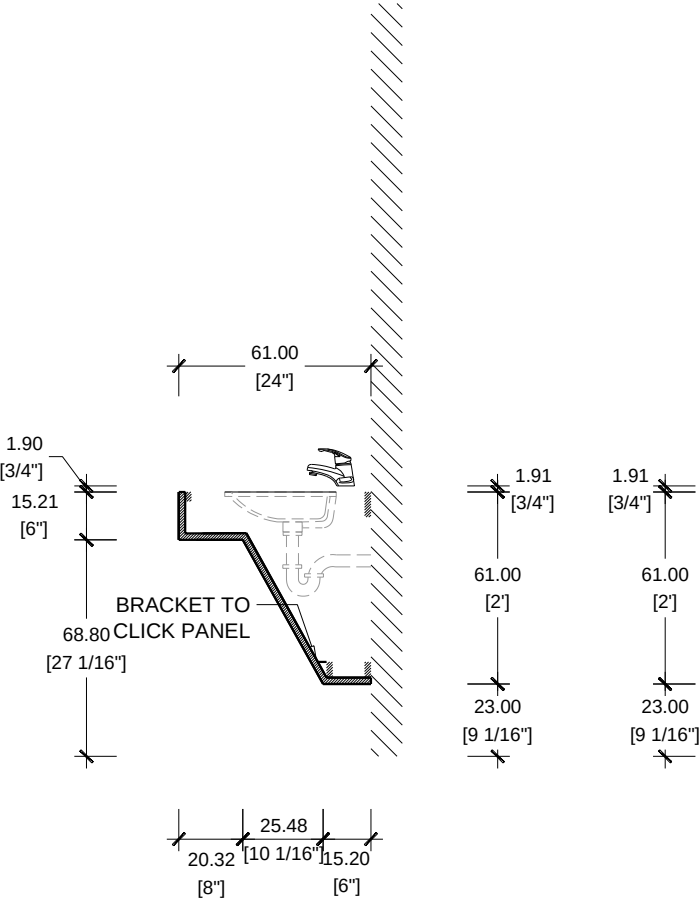


VANITY TYPE RV2

UNIT B2FA


ITALIAN KITCHEN AND BATH			PROJECT #:	DATE:	A.15
kitchen bath tile closet			CASA FAMILIA	REV:	SHEET NUMBER
1777 NW 72TH AVE. MIAMI FL, 33126			KITCHEN VANITIES	DIMENSION:	NUMBER
T. 305.599.9000 F. 305.599.9870				DRAWN BY:	

SIDE VIEW SCALE 1/2"=1'-0"
CASA FAMILIA / VANITY TYPE RV2

VANITY TYPE RV
UNIT B2FA

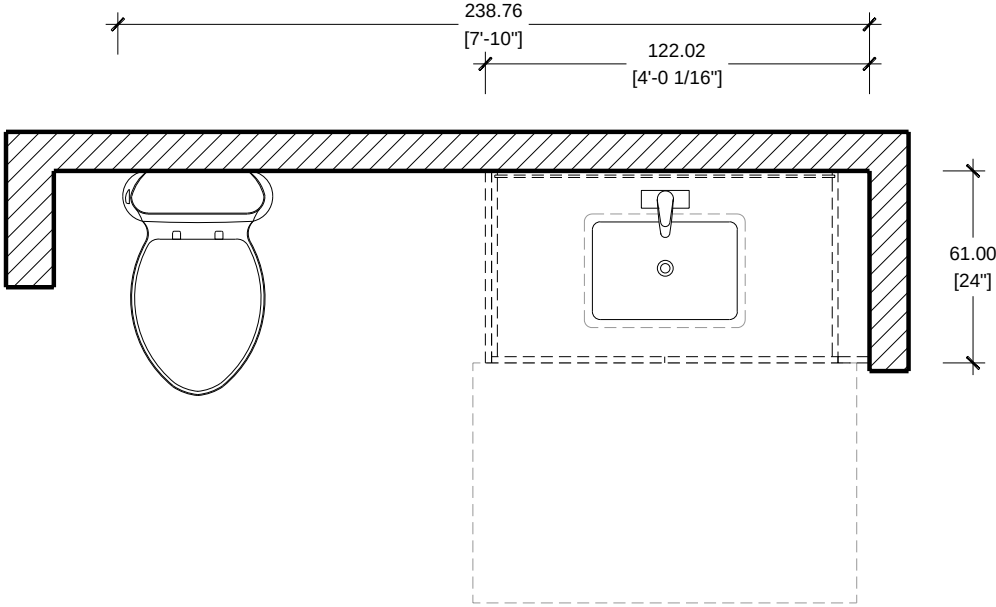


FLOOR PLAN SCALE 1/2"=1'-0"
CASA FAMILIA /VANITY TYPE V4

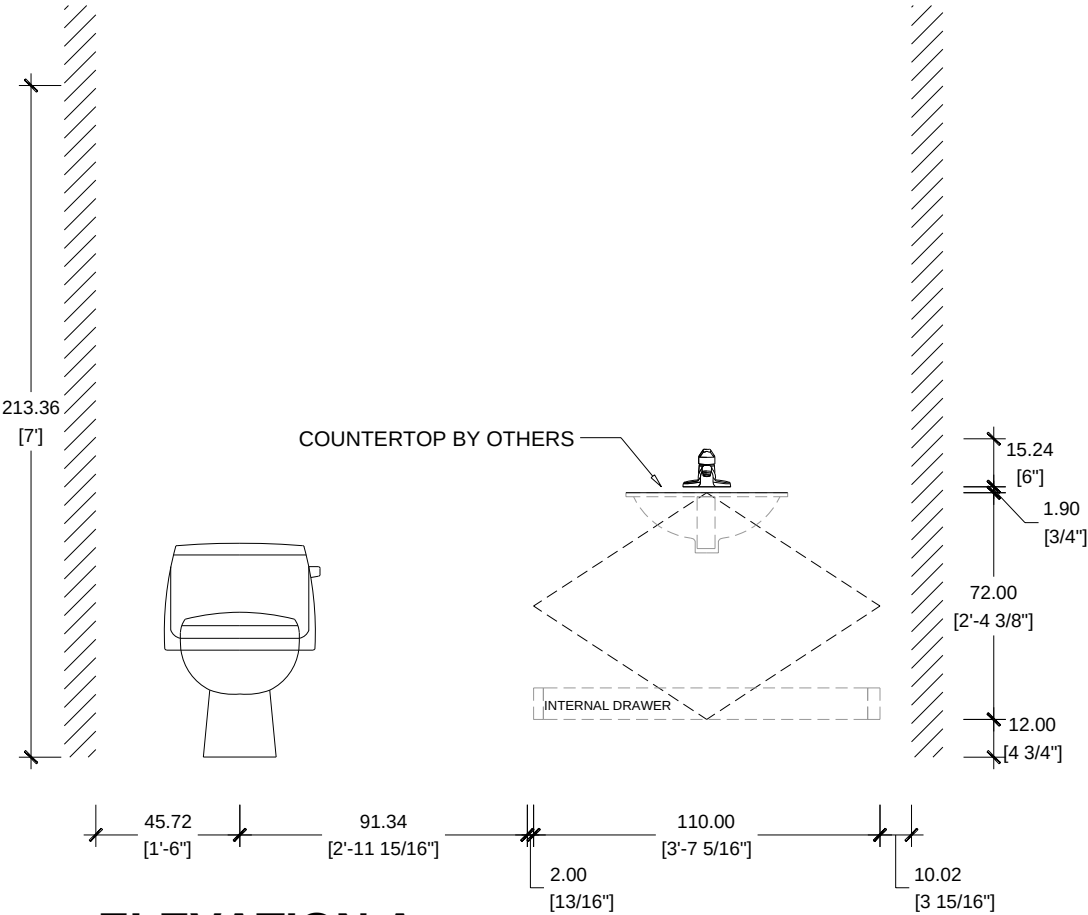


ELEVATION A
CASA FAMILIA UNIT B1 / VANITY TYPE V4


SECTION

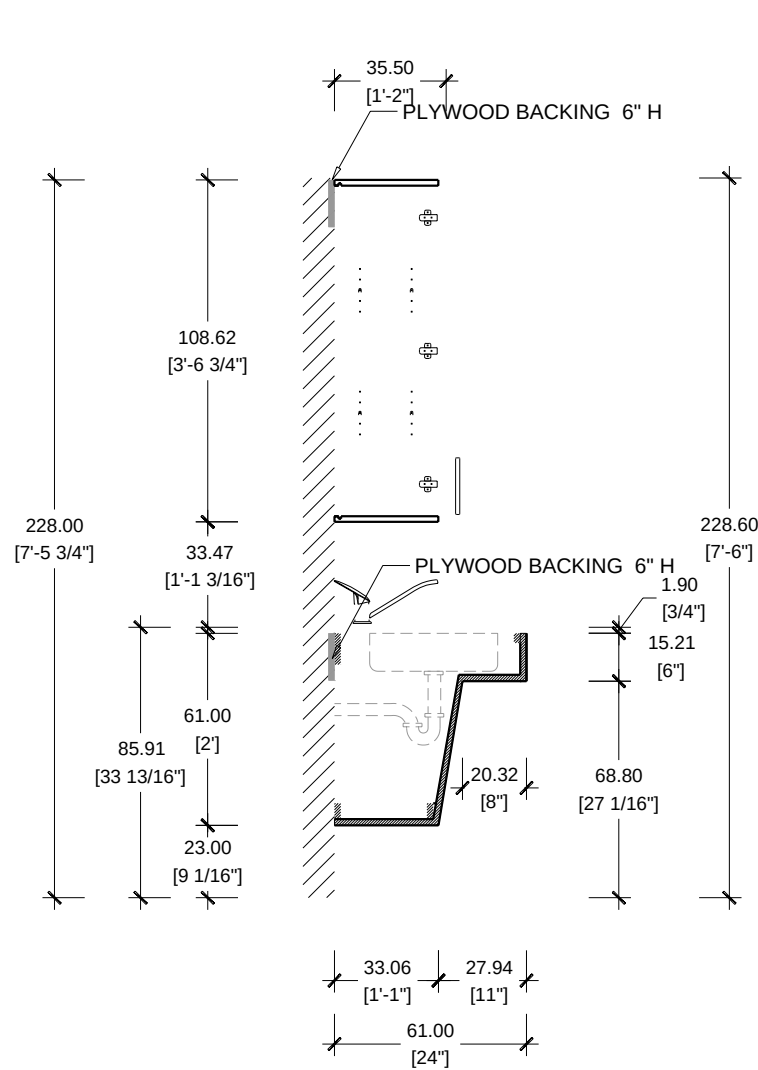


SECTION SCALE 1/2"=1'-0"
KITCHEN ADA

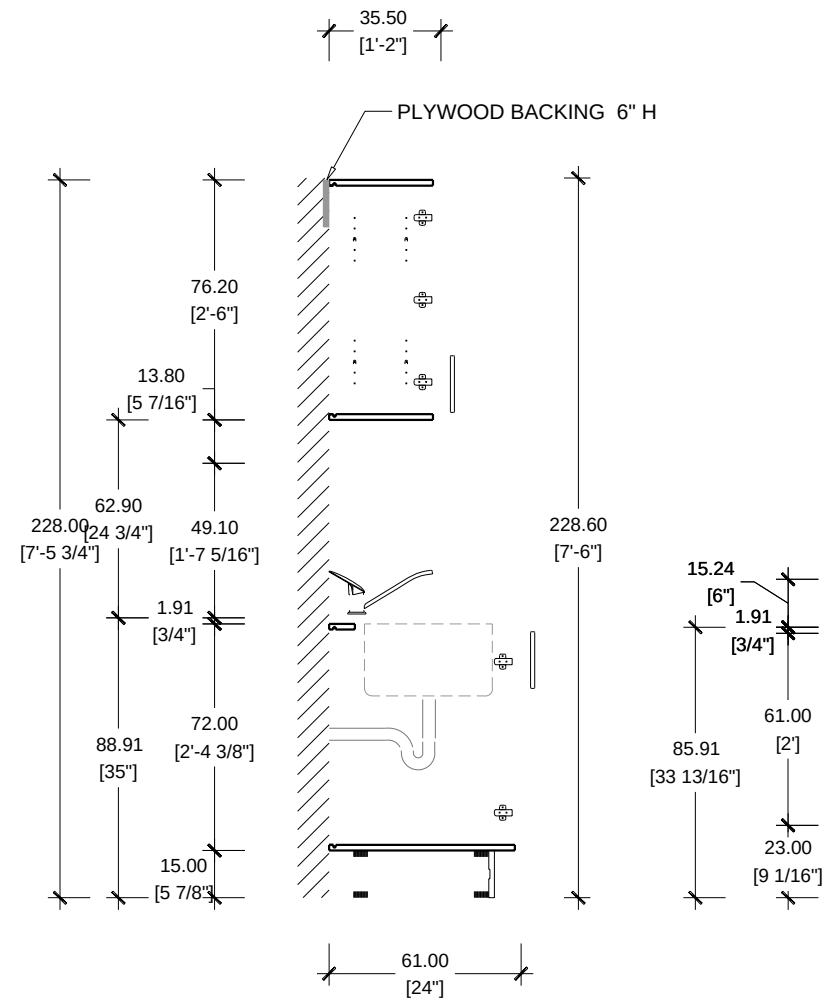

SECTION SCALE 1/2"=1'-0"
KITCHEN

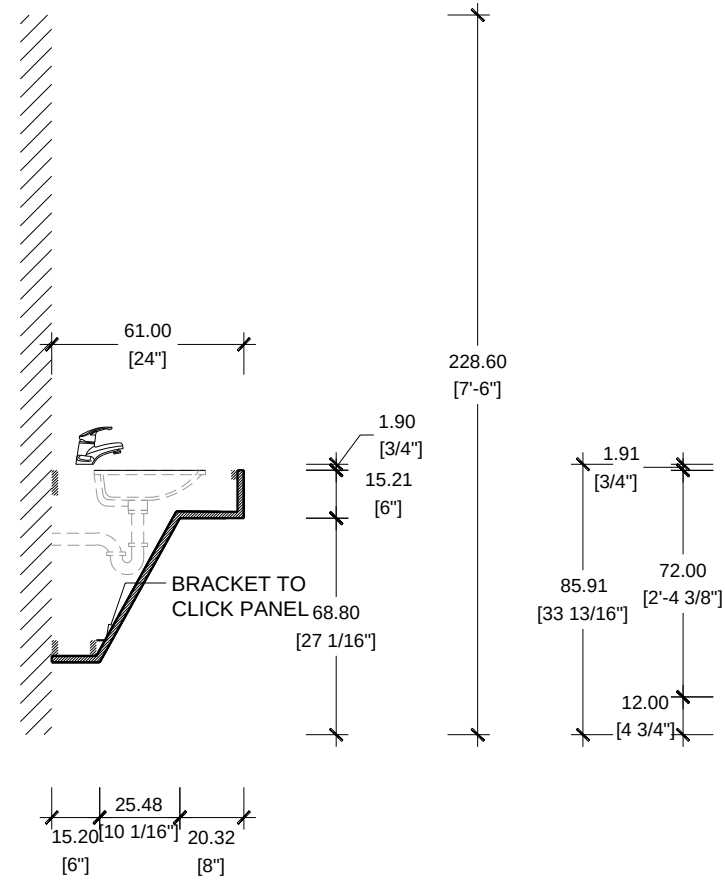

SECTION SCALE 1/2"=1'-0"
VANITY ADA

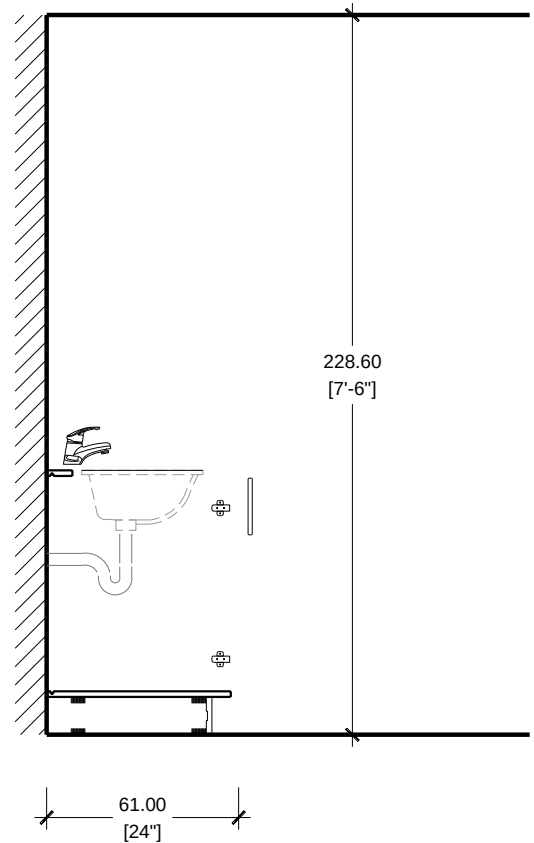


SECTION SCALE 1/2"=1'-0"
VANITY


ITALIAN KITCHEN AND BATH		PROJECT #:	DATE:
kitchen bath tile closet		CASA FAMILIA	REV:
1777 NW 72TH AVE. MIAMI FL, 33126		KITCHEN VANITIES	DIMENSIONS
T. 305.599.9000 F. 305.599.9870			DRAWN BY:

SECTION


PROJECT #:		DATE:	SHEET NUMBER	
CASA FAMILIA		REV:	A.18	
KITCHEN VANITIES		DIMENSION:	SHEET NUMBER	
		DRAWN BY:		
ITALIAN KITCHEN AND BATH				
kitchen bath tile closet				
1777 NW 72TH AVE. MIAMI FL, 33126				
T. 305.599.9000 F. 305.599.9870				

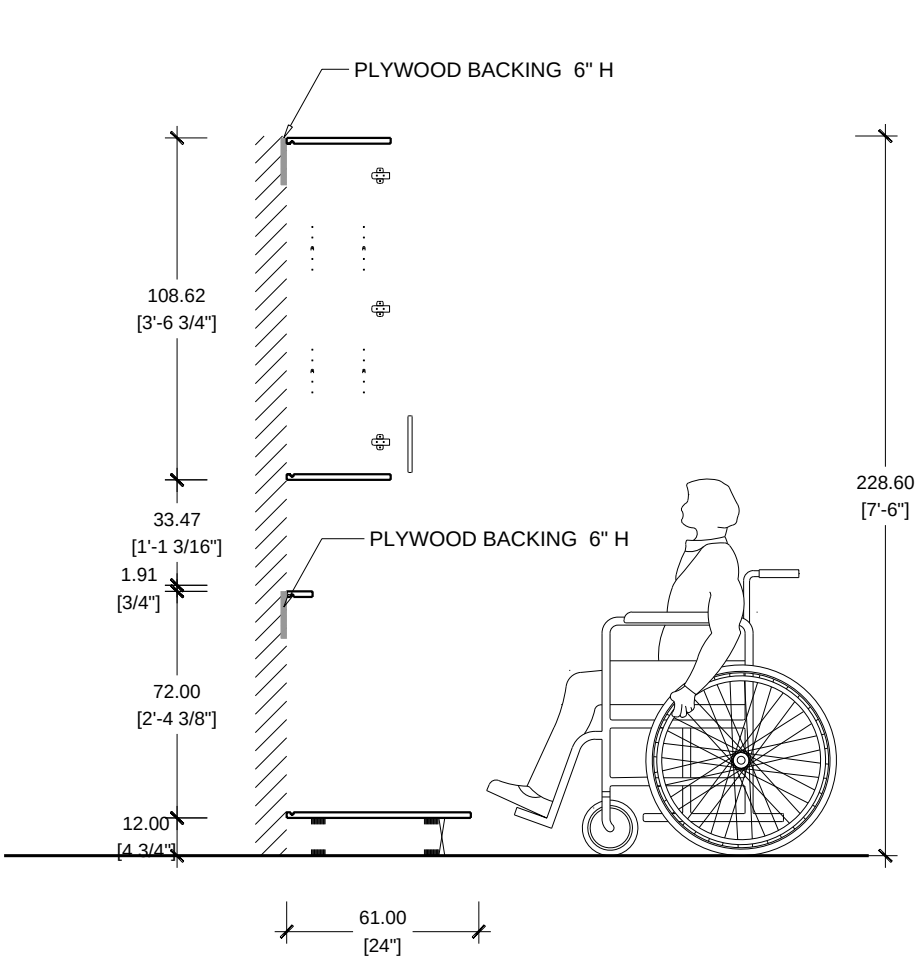


SECTION SCALE 1/2"=1'-0"
KITCHEN ADA DRAWER

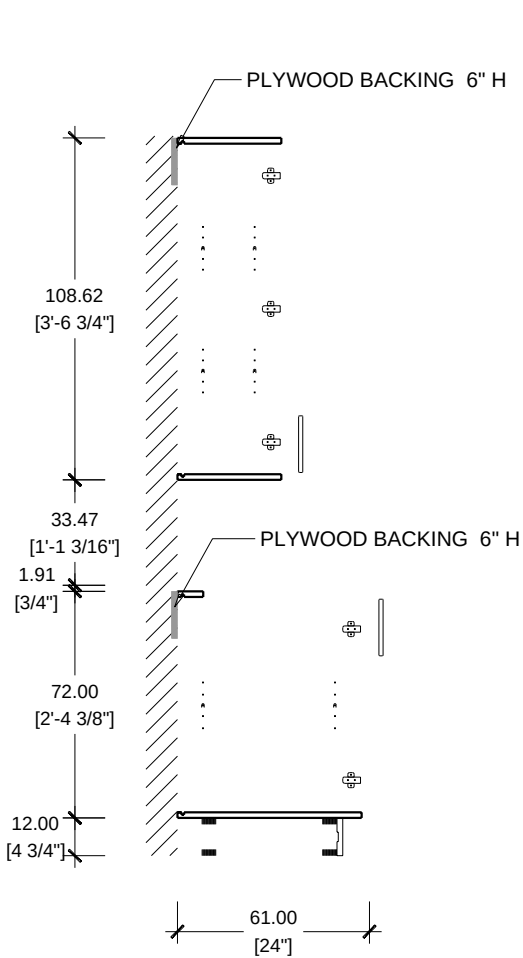

SECTION SCALE 1/2"=1'-0"
KITCHEN ADA

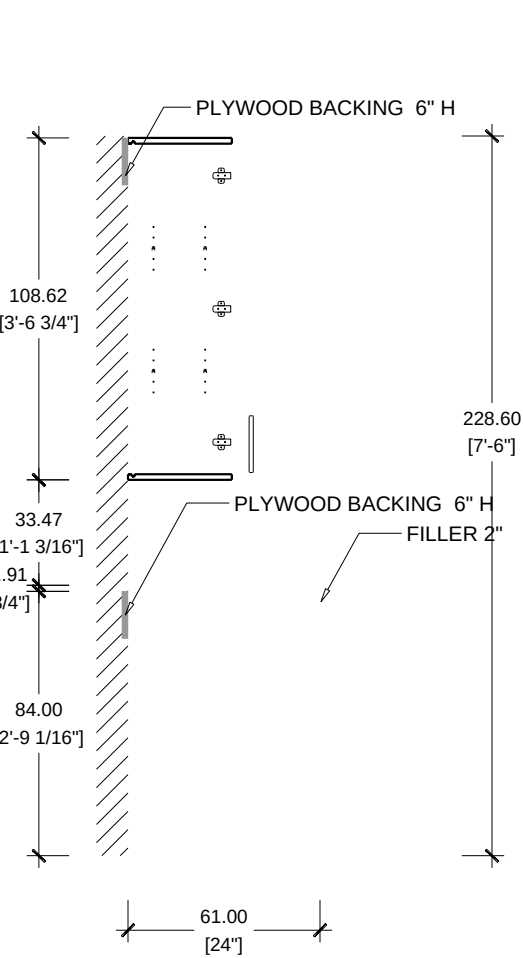


SECTION SCALE 1/2"=1'-0"
KITCHEN ADA

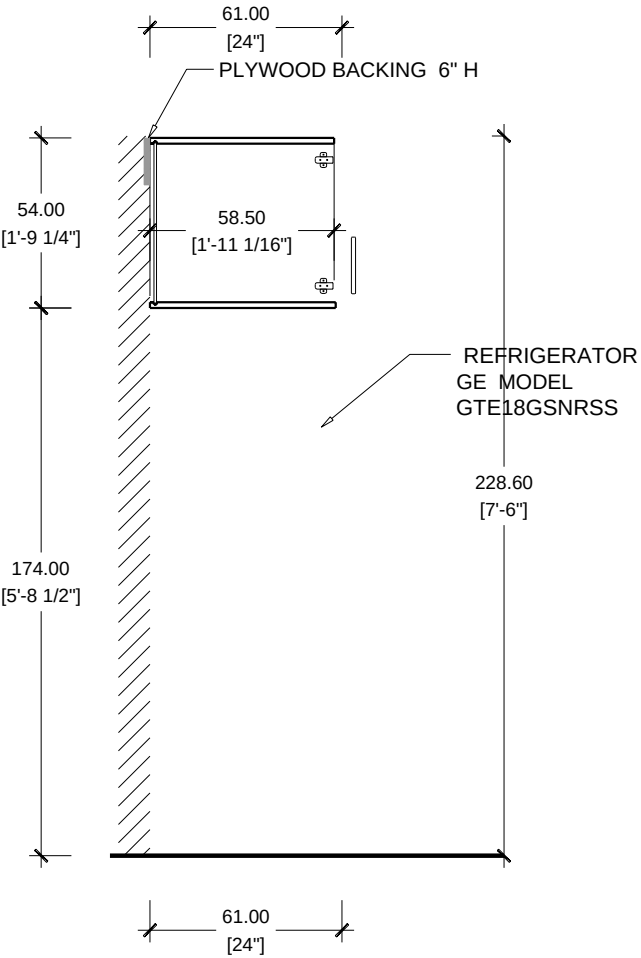

SECTION REFRIGERATOR
SCALE 1/2"=1'-0"
KITCHEN

SECTION

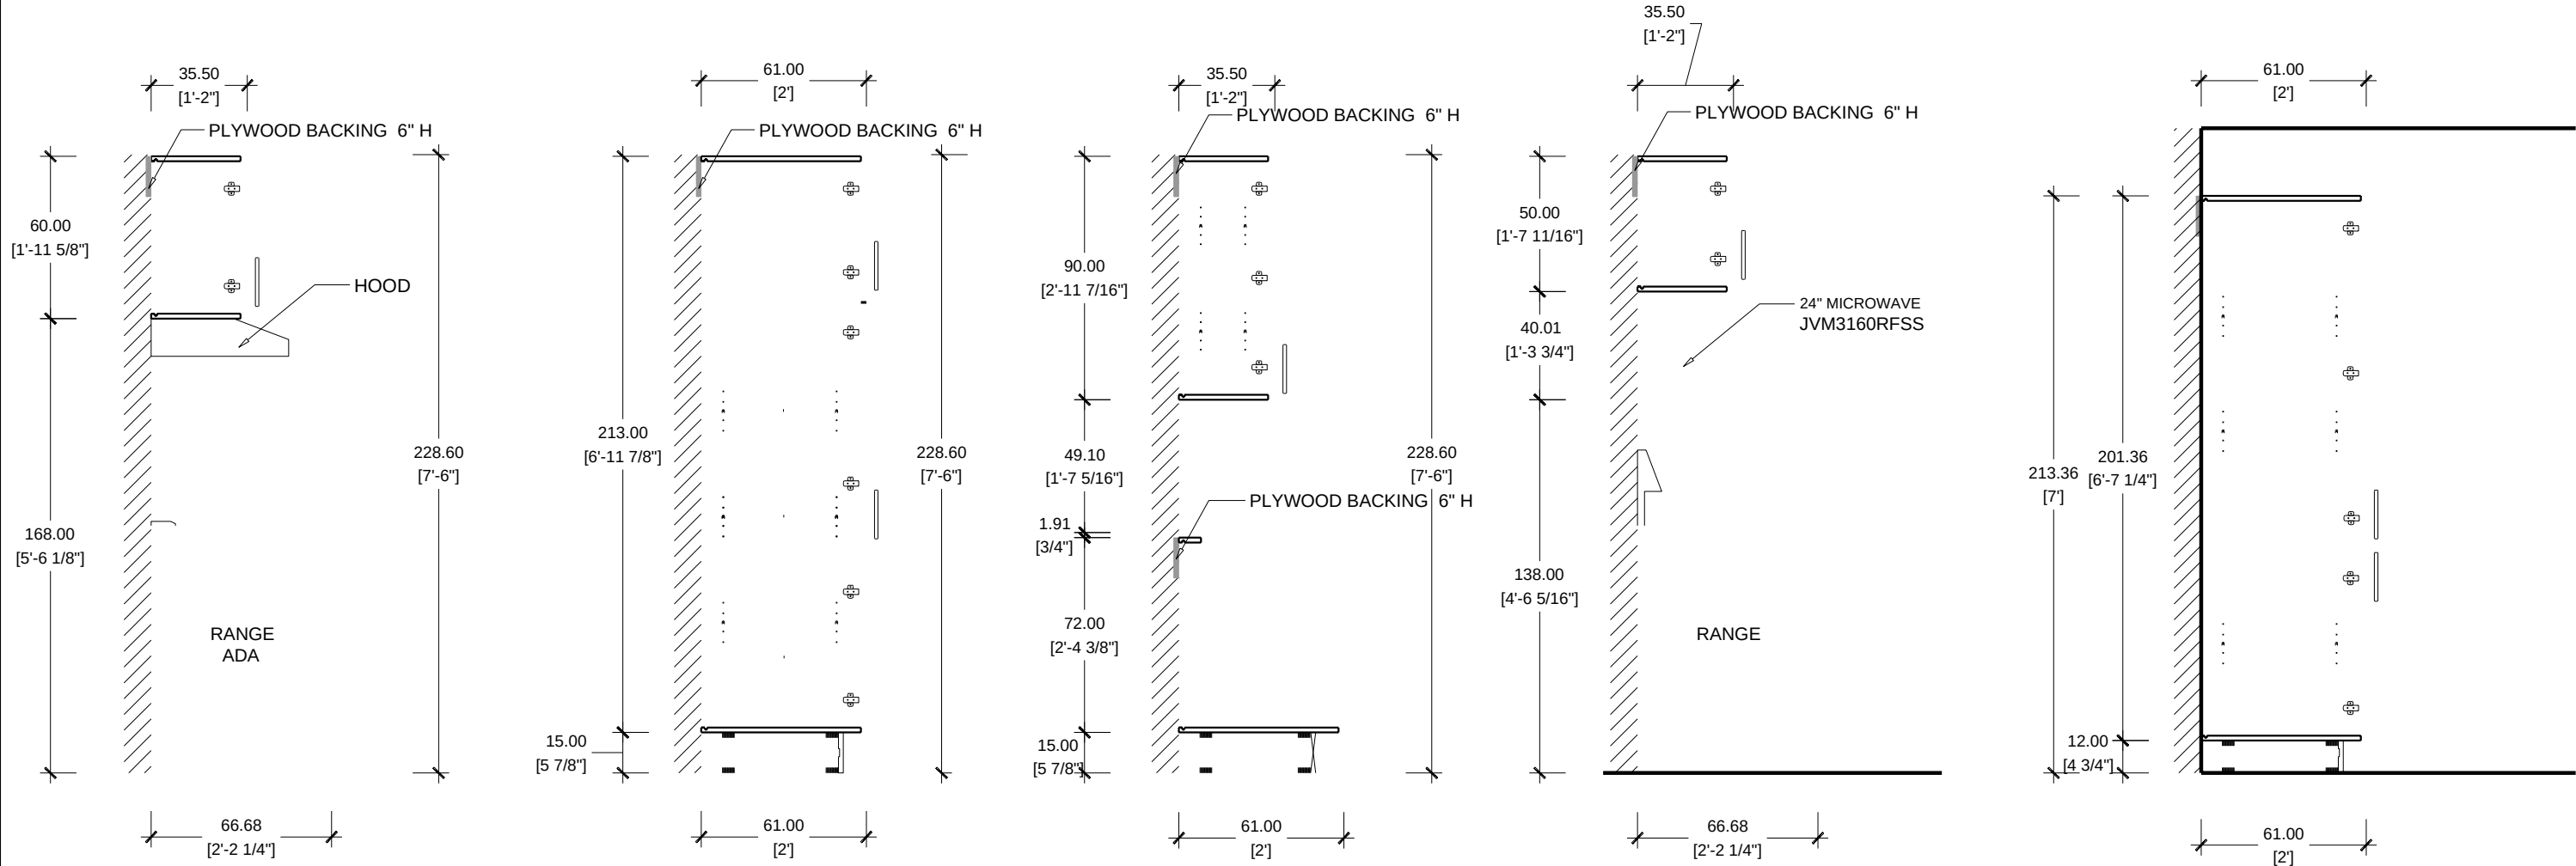

SECTION HOOD KITCHEN ADA SCALE 1/2"=1'-0"

SECTION KITCHEN PANTRY SCALE 1/2"=1'-0"

SECTION KITCHEN DRAWER SCALE 1/2"=1'-0"


SECTION MICROWAVE KITCHEN SCALE 1/2"=1'-0"

SECTION KITCHEN VANITY PANTRY SCALE 1/2"=1'-0"


A.19			
SHEET NUMBER			
DATE:	REY:	DIMENSION:	DRAWN BY:
PROJECT #:			
CASA FAMILIA			
KITCHEN VANITIES			
ITALIAN KITCHEN AND BATH			
Kitchen bath tile closet			
1777 NW 72TH AVE. MIAMI FL, 33126			
T. 305.599.9000 F. 305.599.9870			

KITCHEN


A.20		SHEET NUMBER	
DATE:		REV:	
PROJECT #:		DIMENSION	
CASA FAMILIA		KITCHEN VANITIES	
ITALIAN KITCHEN AND BATH			
kitchen bath tile closet			
1777 NW 72TH AVE. MIAMI FL, 33126			

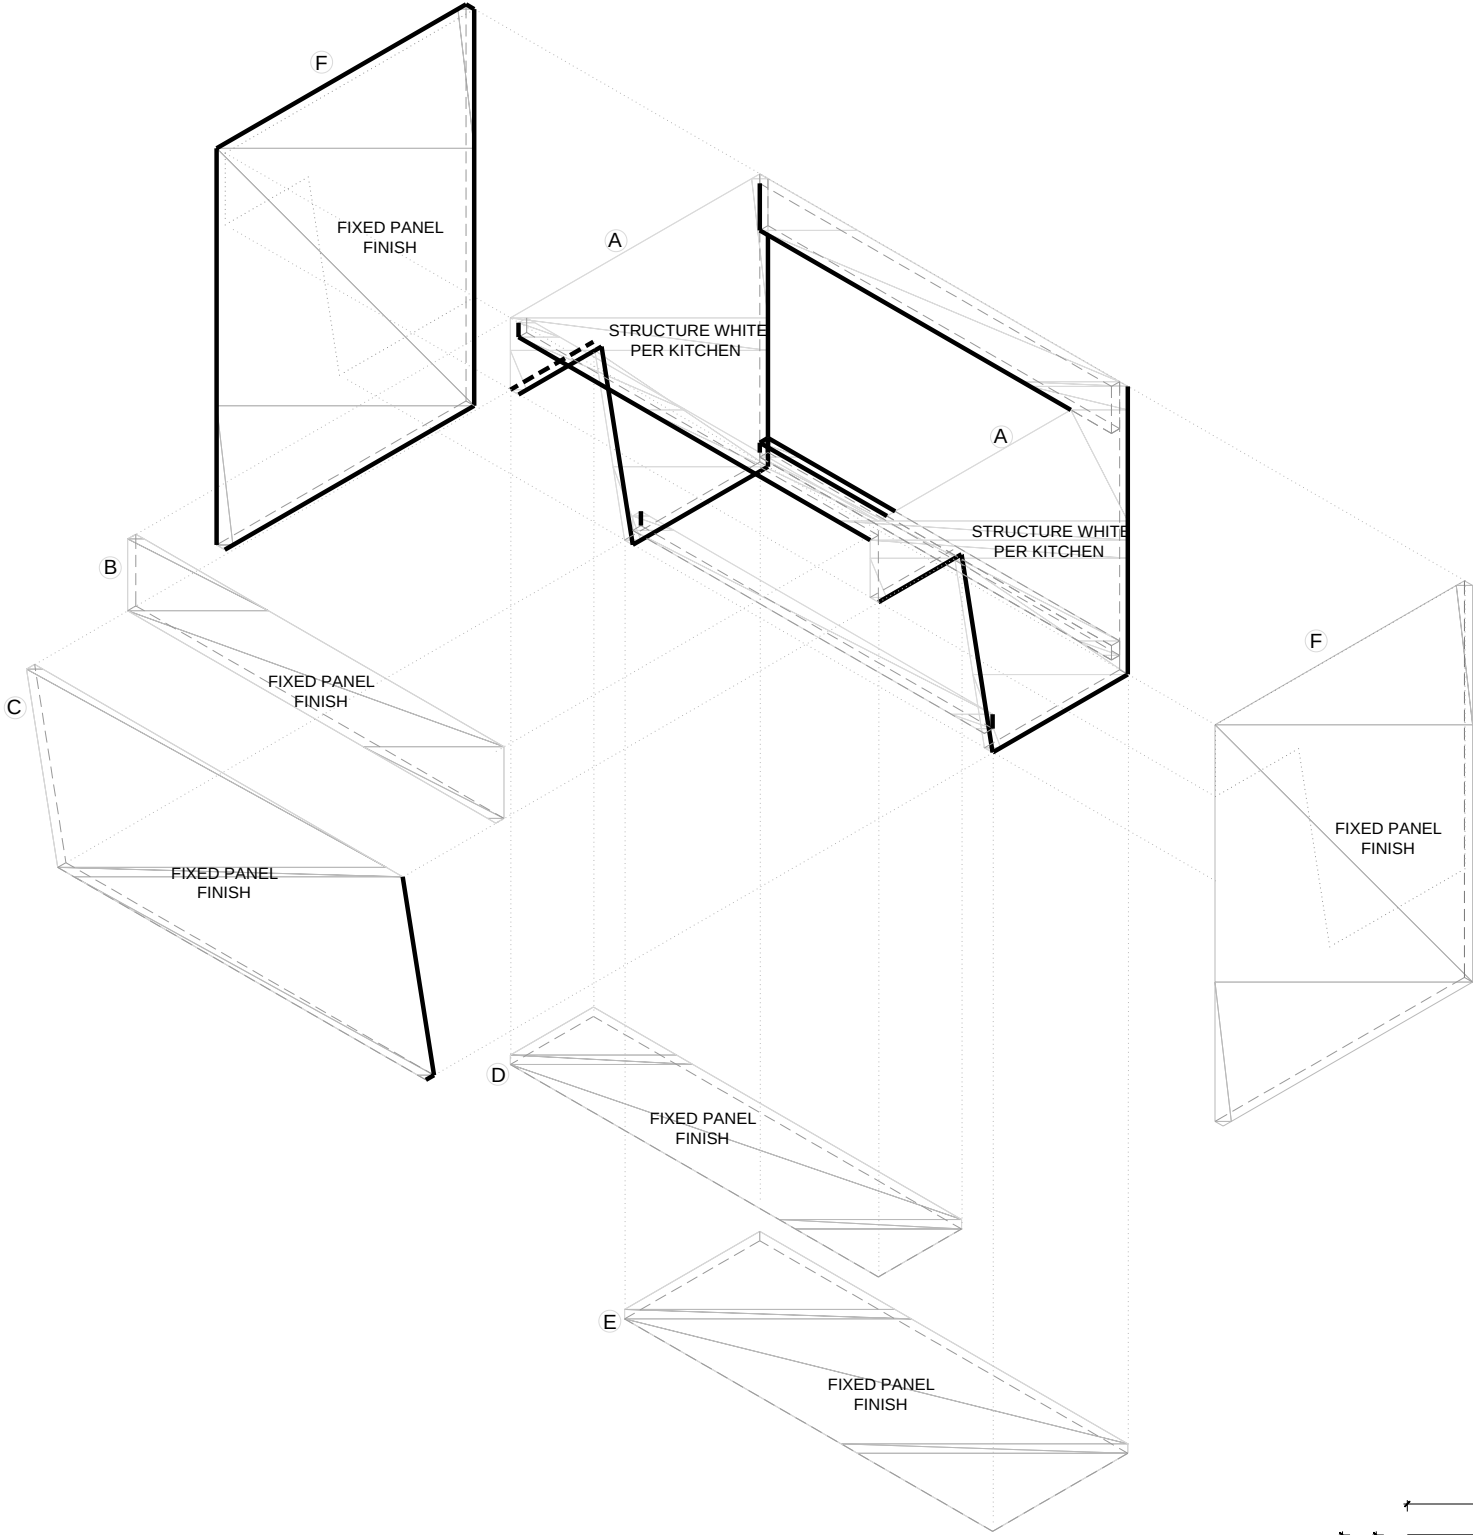


PARTS BY KITCHEN SCALE 1/2"=1'-0"
KITCHEN ADA SINK

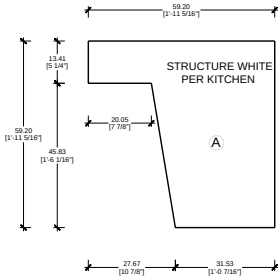



PARTS BY KITCHEN SCALE 1/2"=1'-0"
KITCHEN | BASE 90 CM

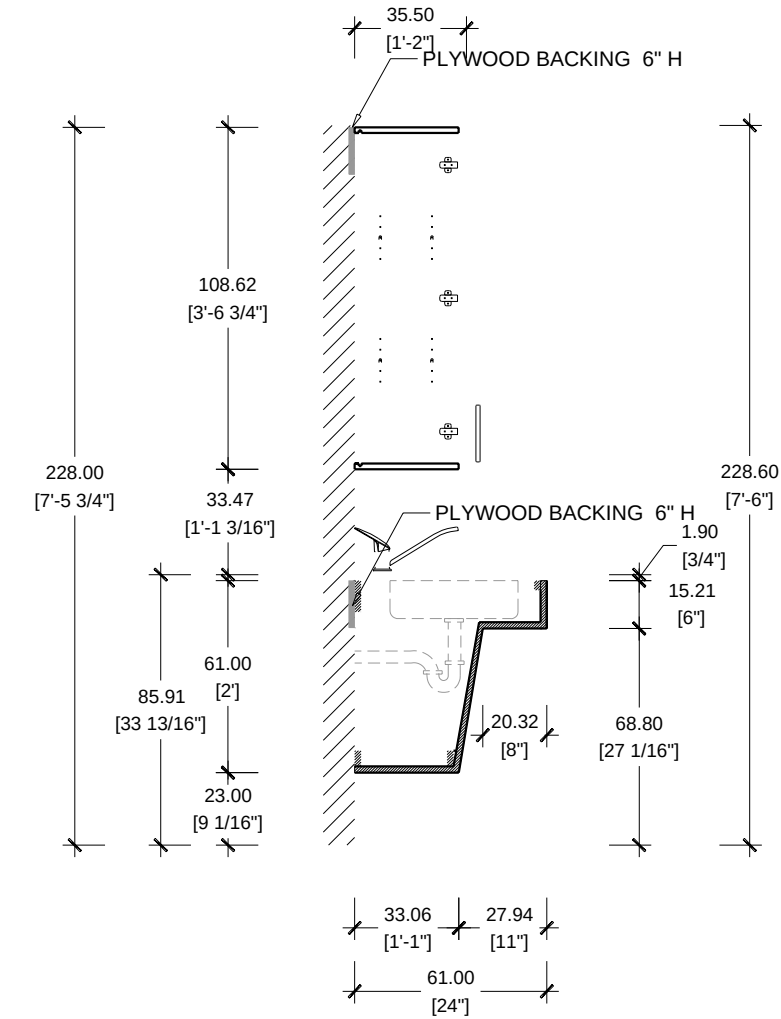

SECTION SCALE 1/2"=1'-0"
KITCHEN ADA

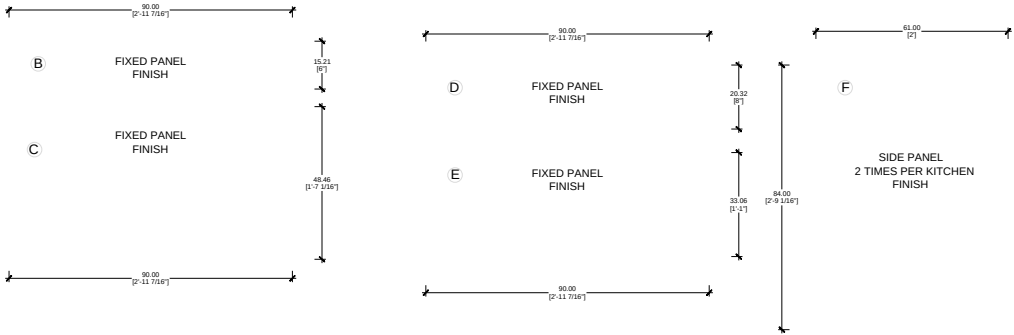

VANITIES

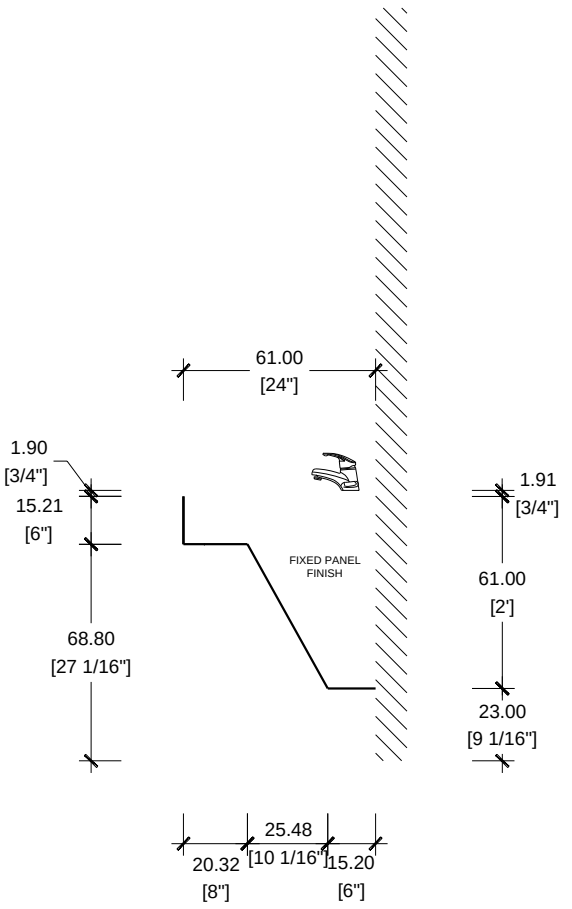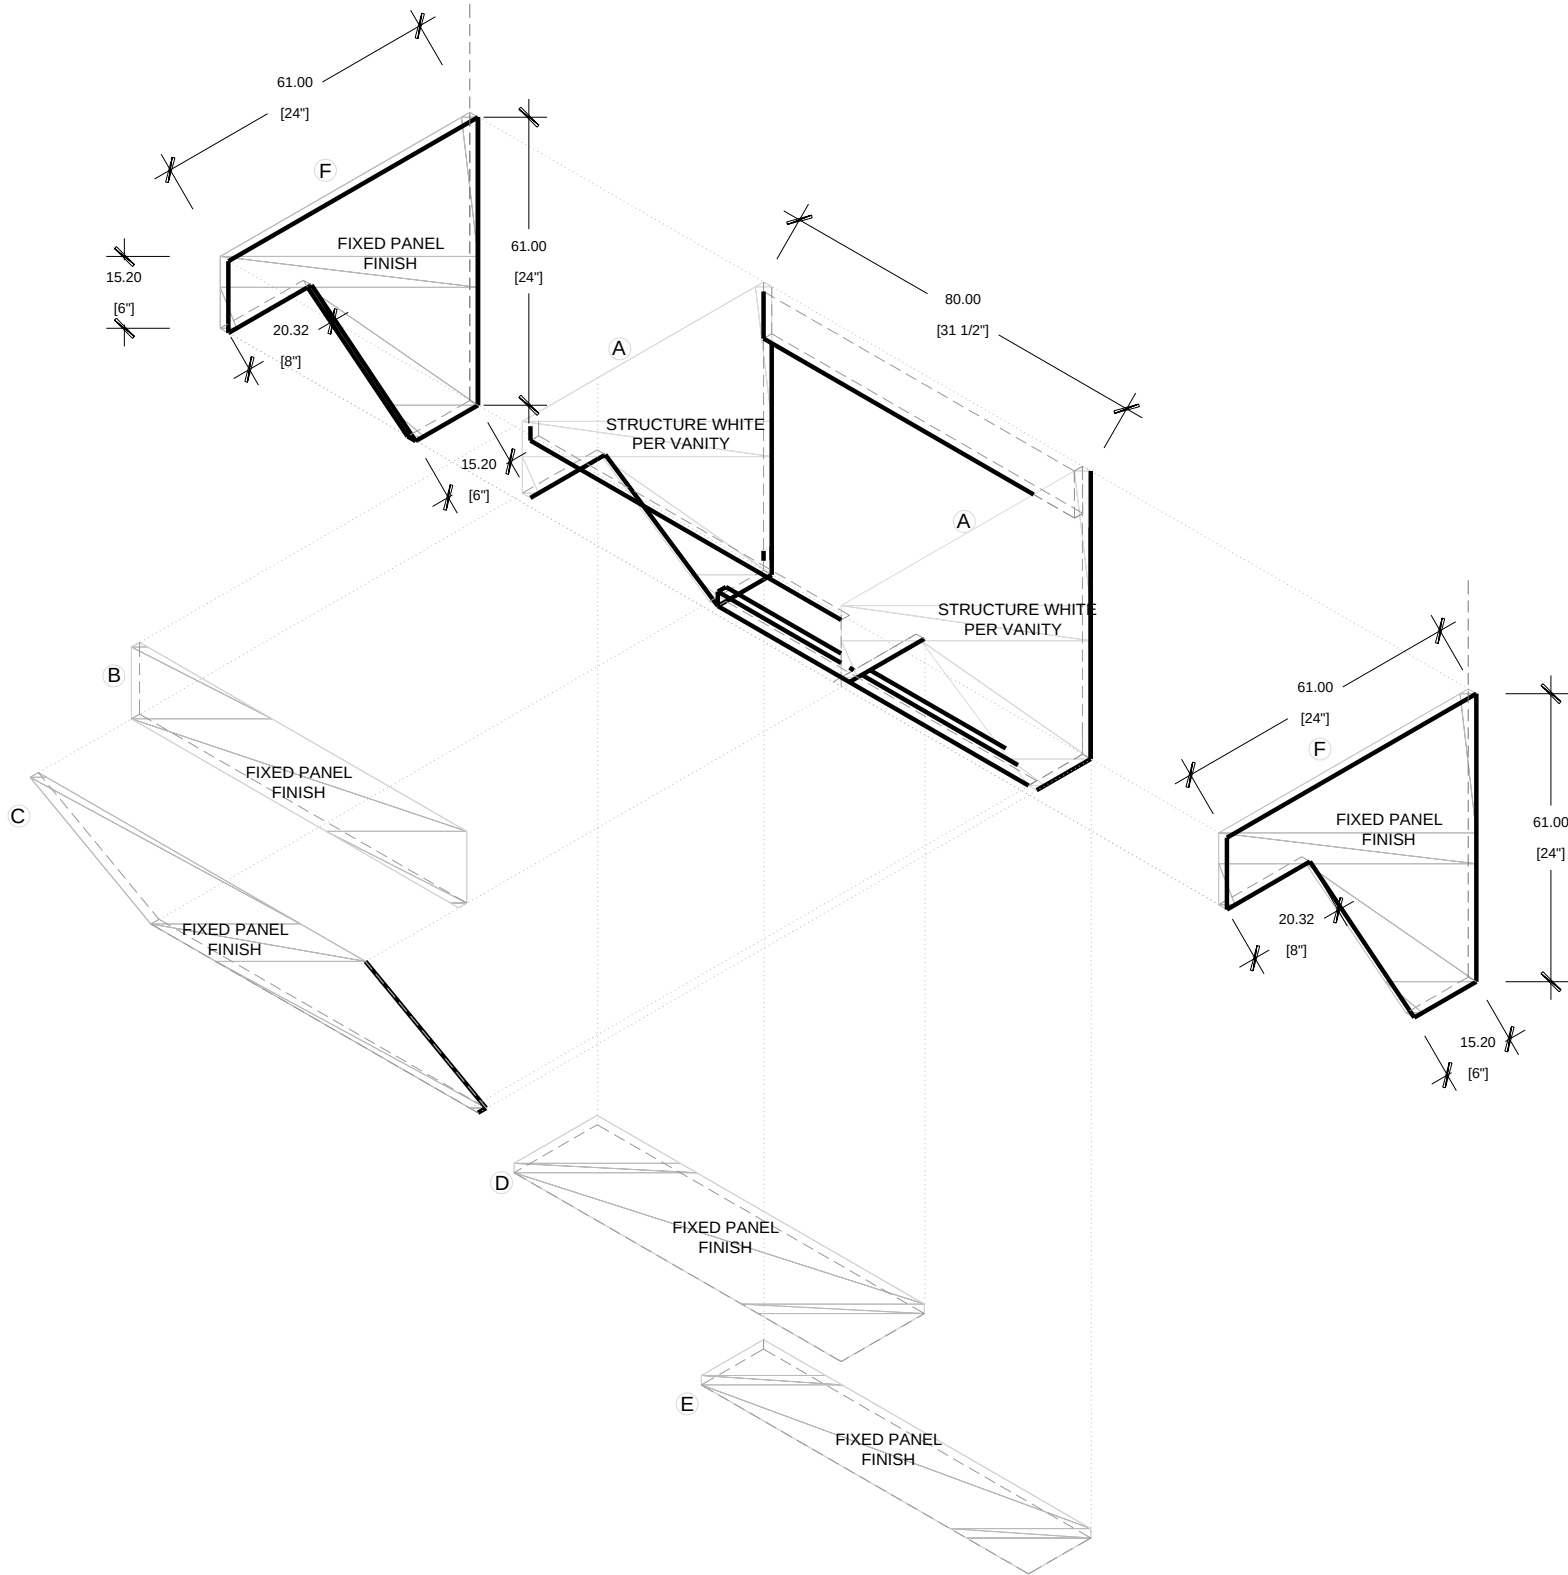

SIDE VIEW SCALE 1/2"=1'-0"
CASA FAMILIA / VANITY TYPE V2

PARTS BY VANITIES SCALE 1/2"=1'-0"
VANITIES ADA SINK

A.21			
SHEET NUMBER			
DATE:	REV:	DIMENSION	DRAWN BY:
PROJECT #:			
CASA FAMILIA			
KITCHEN VANITIES			
ITALIAN KITCHEN AND BATH			
Kitchen bath tile closet			
1777 NW 72TH AVE. MIAMI FL, 33126			
T. 305.599.9000 F. 305.599.9870			